

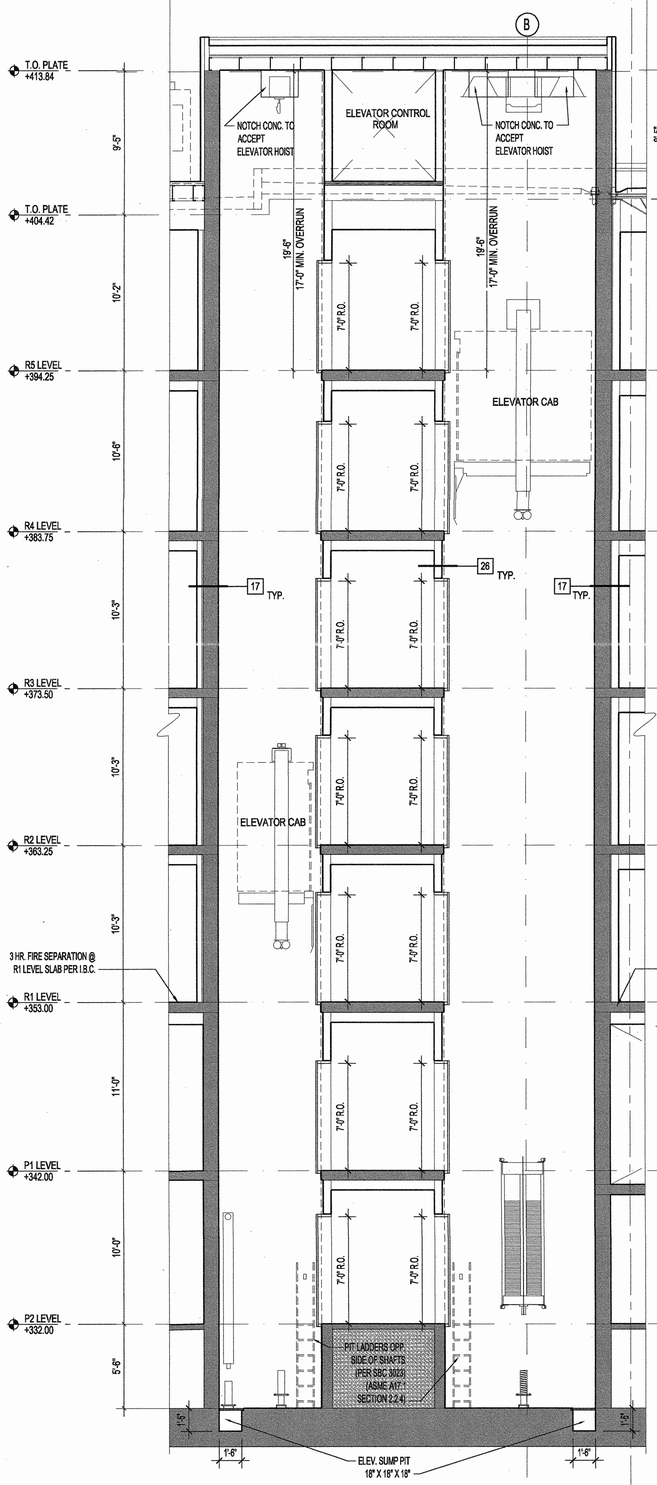


25 ELEVATOR CORE SECTION M1 & M2
1/4" = 1'-0"

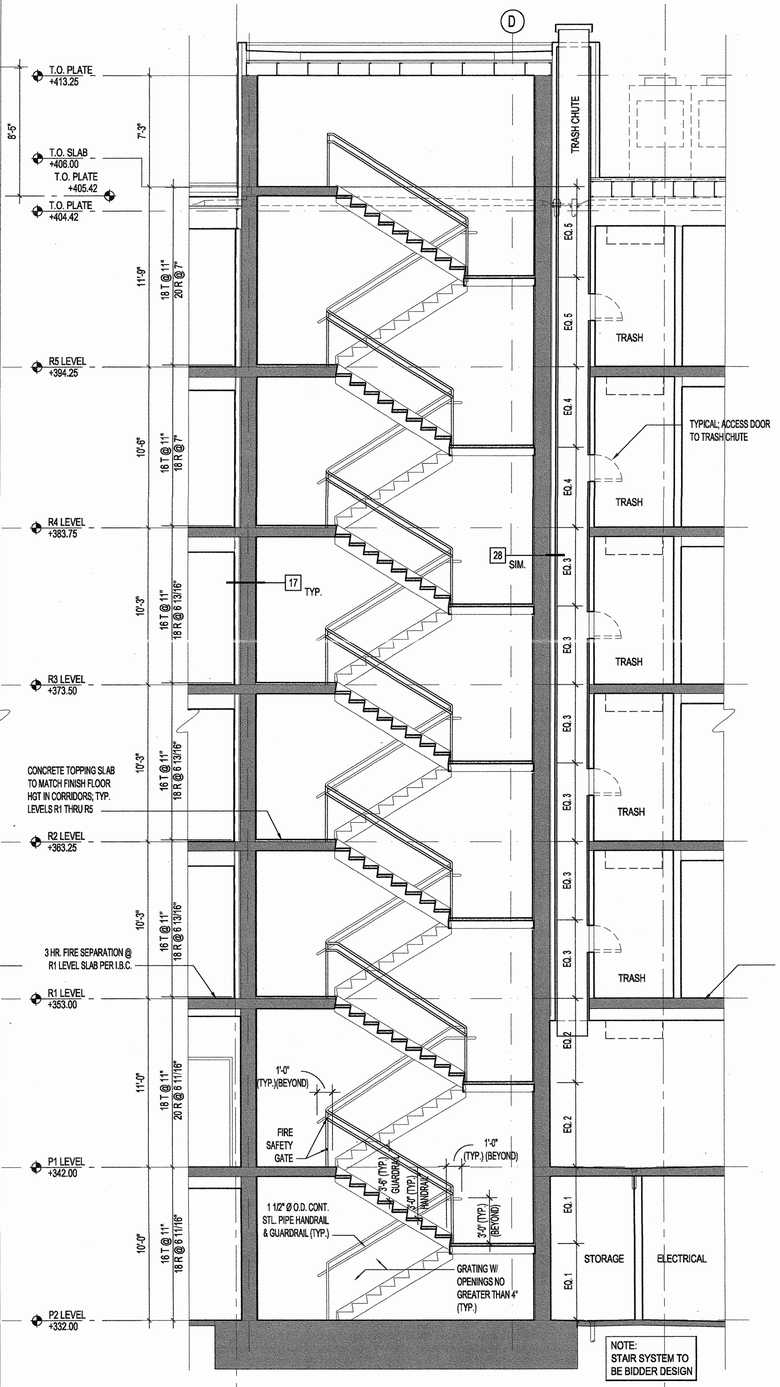

27 STAIR M1 CORE SECTION
1/4" = 1'-0"

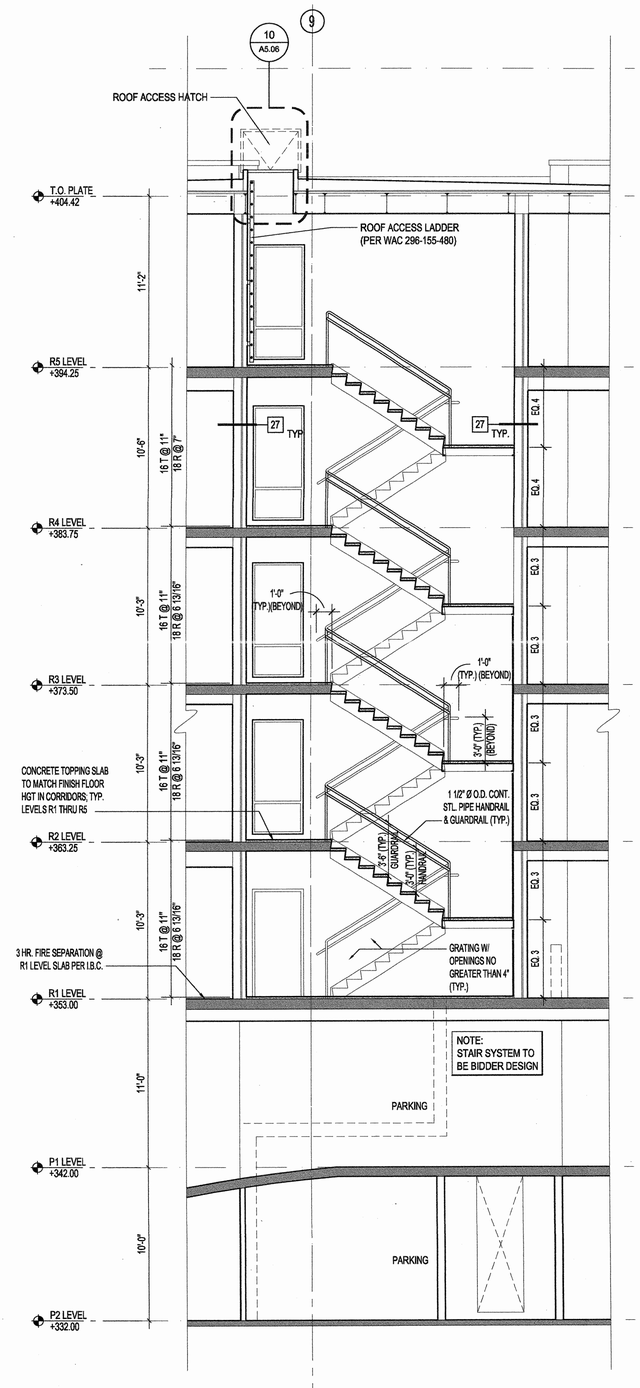

29 STAIR M2 CORE SECTION
1/4" = 1'-0"

MITHUN
Architects+Designers+Planners

Pier 56
1201 Alaskan Way
Suite 200
Seattle, WA 98101
TEL 206 623.3344
FAX 206 623.7005

PROJECT:
200 W. Highland Drive

LOCATION:
202 W. Highland Drive
Seattle, WA 98119

PREPARED FOR:
Lorig Associates, LLC
2025 First Avenue, Suite 420
Seattle WA. 98121
T= 206.728.7660

NO.	DATE	REVISION

PROJECT DIRECTOR: JB
PROJECT MANAGER: EMD
PROJECT ARCHITECT: BB
PROJECT TEAM MEMBERS: ML, ML
CHECK:

ARCHITECT SEAL


3689 REGISTERED ARCHITECT
BRUCE L. WILLIAMS
STATE OF WASHINGTON

TITLE
ELEVATOR & STAIR SECTIONS


PROJECT NO. 04470.00
DATE 04-02-07
PROJECT NETWORK PATH S:_2005\0447000\Cadd\
A\SHEETS
SHEET NUMBER **A6.01**

CONTRACT DOCUMENTS


© 2004 MITHUN, INC.

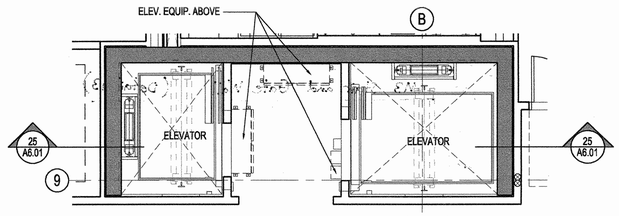


01 ELEVATOR CORE M1 & M2 - R5 LEVEL
1/4" = 1'-0"

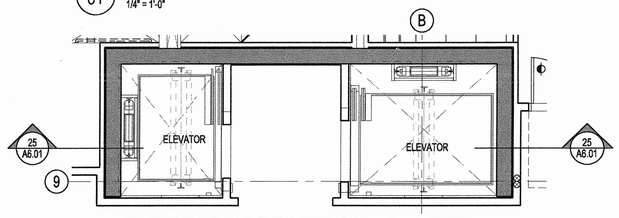


02 ELEVATOR CORE M1 & M2 - R4 LEVEL
1/4" = 1'-0"

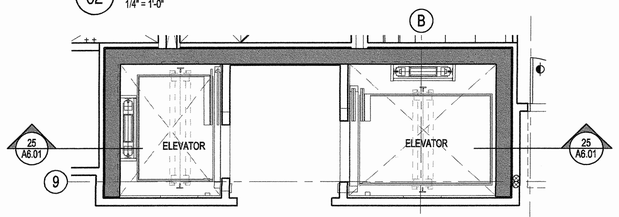


03 ELEVATOR CORE M1 & M2 - R3 LEVEL
1/4" = 1'-0"

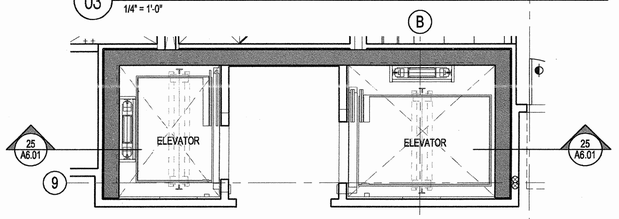


04 ELEVATOR CORE M1 & M2 - R2 LEVEL
1/4" = 1'-0"

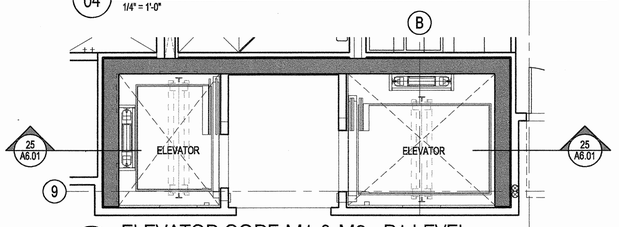


05 ELEVATOR CORE M1 & M2 - R1 LEVEL
1/4" = 1'-0"

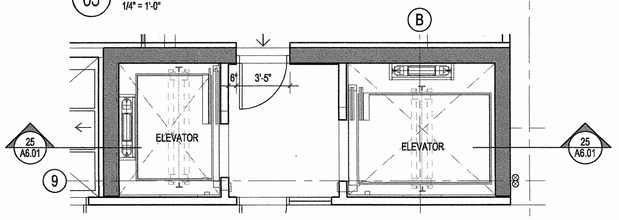


06 ELEVATOR CORE M1 & M2 - P1 LEVEL
1/4" = 1'-0"

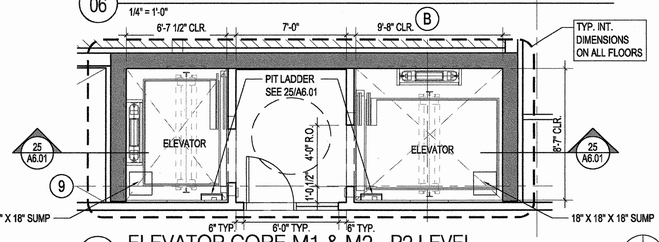


07 ELEVATOR CORE M1 & M2 - P2 LEVEL
1/4" = 1'-0"

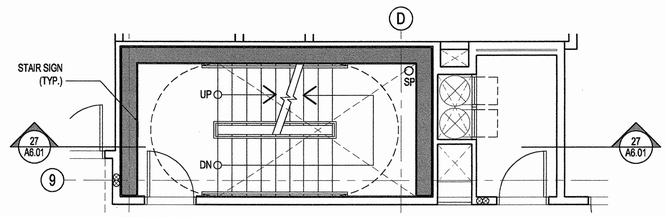


08 STAIR M1 - R5 LEVEL
1/4" = 1'-0"

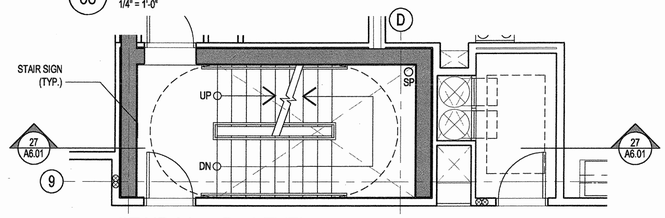


09 STAIR M1 - R4 LEVEL
1/4" = 1'-0"

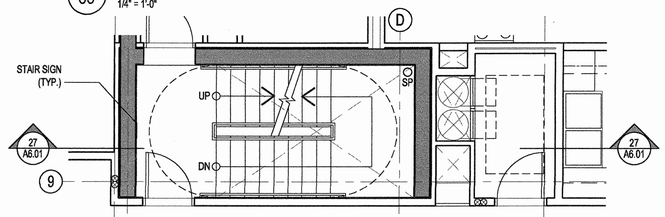


10 STAIR M1 - R3 LEVEL
1/4" = 1'-0"

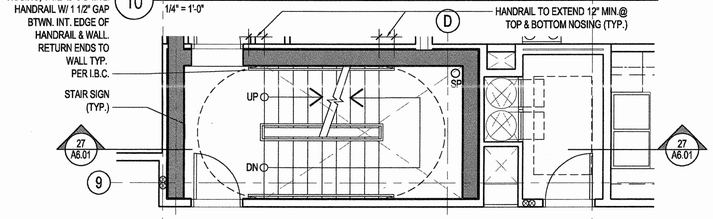


11 STAIR M1 - R2 LEVEL
1/4" = 1'-0"

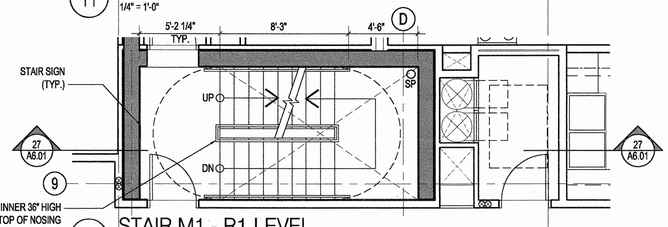


12 STAIR M1 - R1 LEVEL
1/4" = 1'-0"

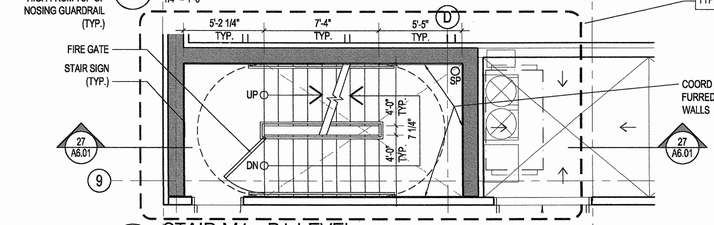


13 STAIR M1 - P1 LEVEL
1/4" = 1'-0"

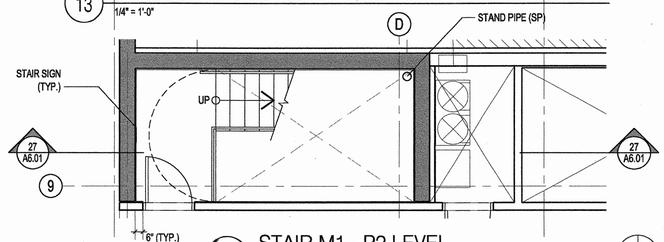


14 STAIR M1 - P2 LEVEL
1/4" = 1'-0"

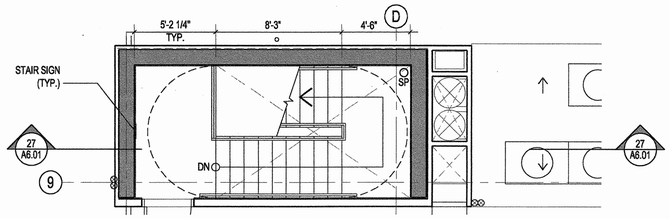


15 STAIR M1 - ROOF LEVEL
1/4" = 1'-0"

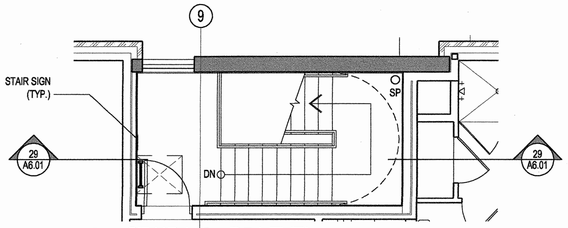


16 STAIR M2 - R5 LEVEL
1/4" = 1'-0"

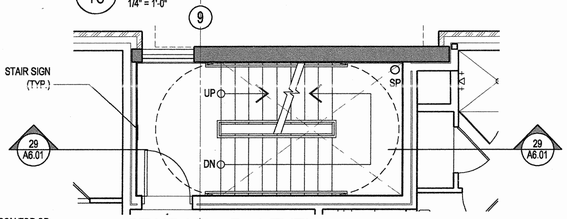


17 STAIR M2 - R4 LEVEL
1/4" = 1'-0"

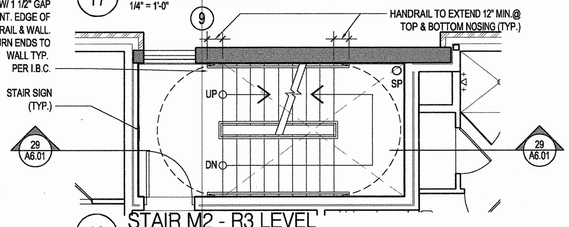

18 STAIR M2 - R3 LEVEL
1/4" = 1'-0"

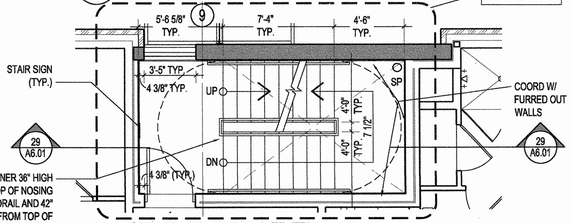

19 STAIR M2 - R2 LEVEL
1/4" = 1'-0"

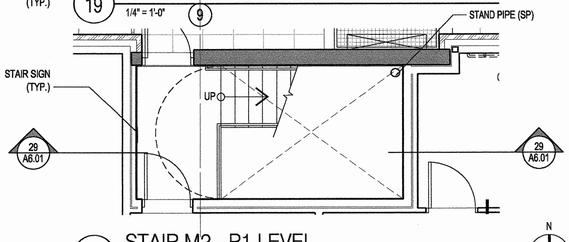

20 STAIR M2 - R1 LEVEL
1/4" = 1'-0"

MITHUN
Architects+Designers+Planners
Pier 56
1201 Alaskan Way
Suite 200
Seattle, WA 98101
TEL 206 623.3344
FAX 206 623.7005

200 West Highland

PROJECT:
200 W. Highland Drive
LOCATION:
202 W. Highland Drive
Seattle, WA 98119

PREPARED FOR:
Lorig Associates, LLC
2025 First Avenue, Suite 420
Seattle WA. 98121
T= 206.728.7660

NO.	DATE	REVISION


PROJECT DIRECTOR: JB
PROJECT MANAGER: EMD
PROJECT ARCHITECT: BB
PROJECT TEAM MEMBERS: ML, ML
CHECK:

ARCHITECT SEAL:
3589 REGISTERED ARCHITECT
BRUCE A. WILLIAMS
STATE OF WASHINGTON


TITLE
ELEVATOR & STAIR PLANS

PROJECT NO.: 04470.00
DATE: 04-02-07
PROJECT NETWORK PATH: S:_2005\047000\Cadd\
A\SHEETS
SHEET NUMBER
A6.02


CONTRACT DOCUMENTS
© 2004 MITHUN, INC.

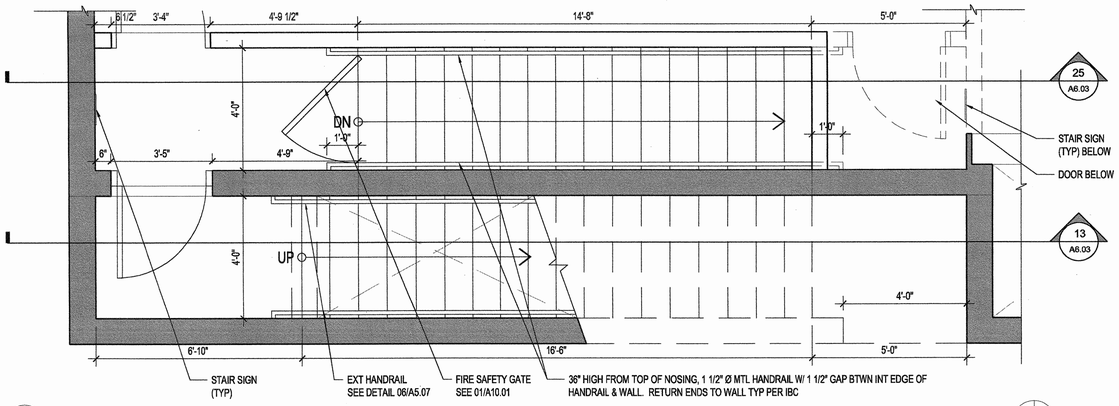


07 STAIR M3 PLAN AT P1
1/2" = 1'- 0"

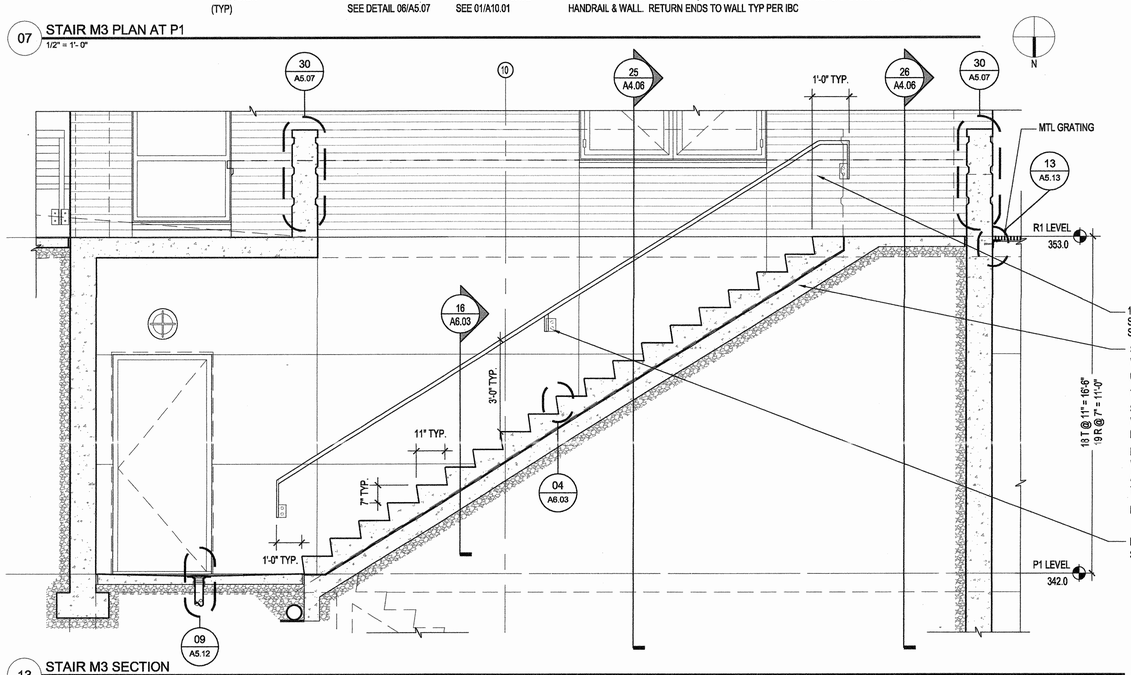


13 STAIR M3 SECTION
1/2" = 1'- 0"

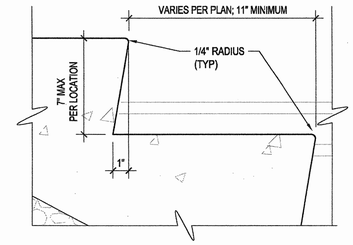


04 TYP CIP CONC STAIR
3" = 1' - 0"

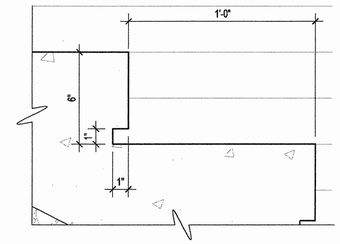


10 ENTRY CIP CONC STAIR
3" = 1' - 0"

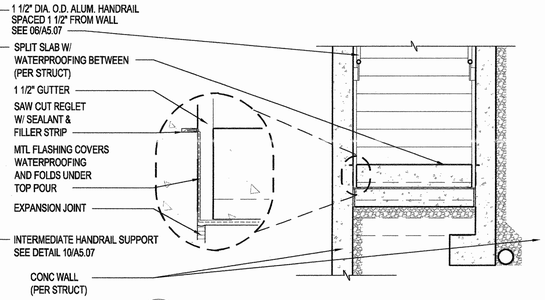


16 STAIR M3 SECTION
1/2" = 1'- 0"

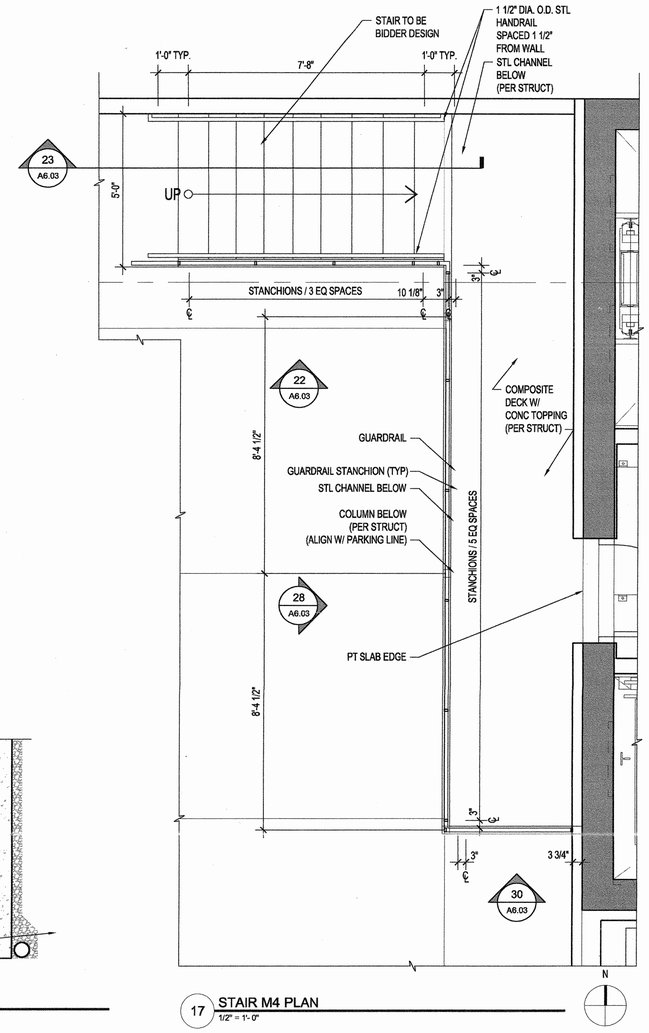


17 STAIR M4 PLAN
1/2" = 1'- 0"

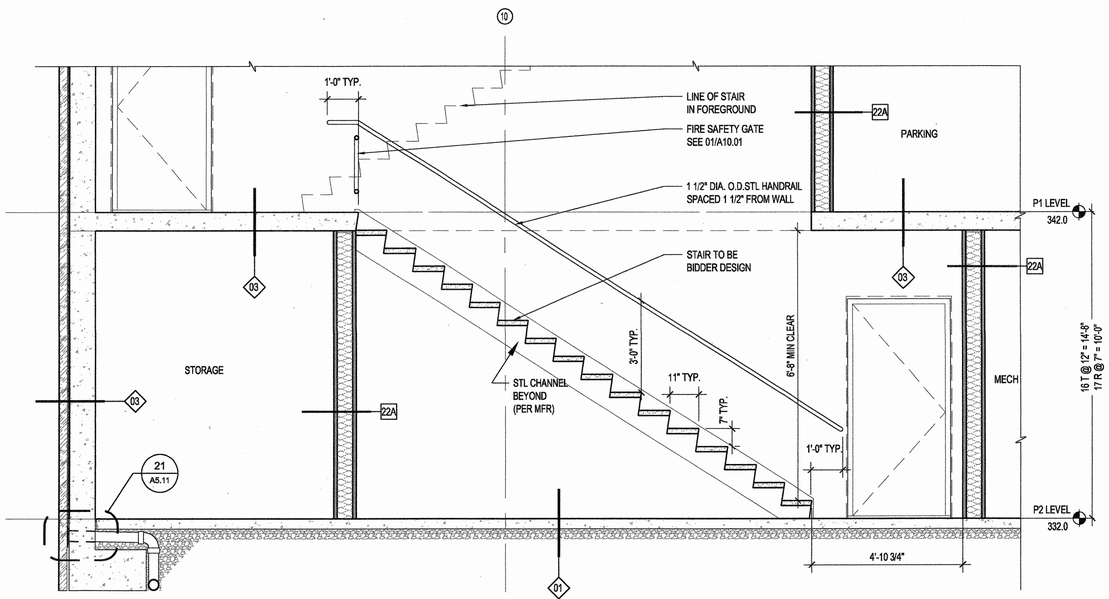


25 STAIR M3 SECTION
1/2" = 1'- 0"

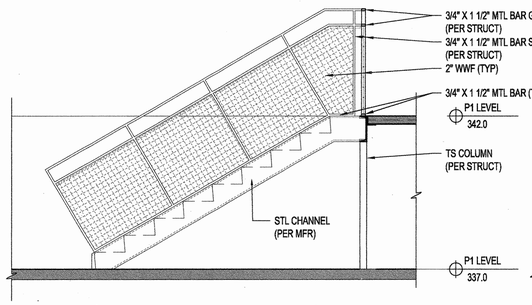

22 STAIR M4 ELEVATION
1/2" = 1'- 0"

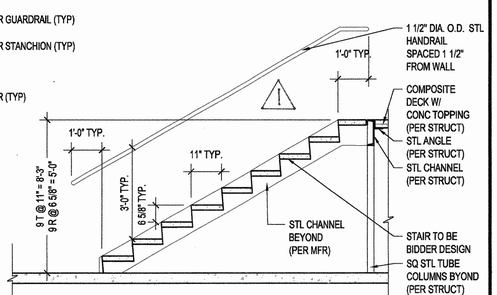

23 STAIR M4 SECTION
1/2" = 1'- 0"

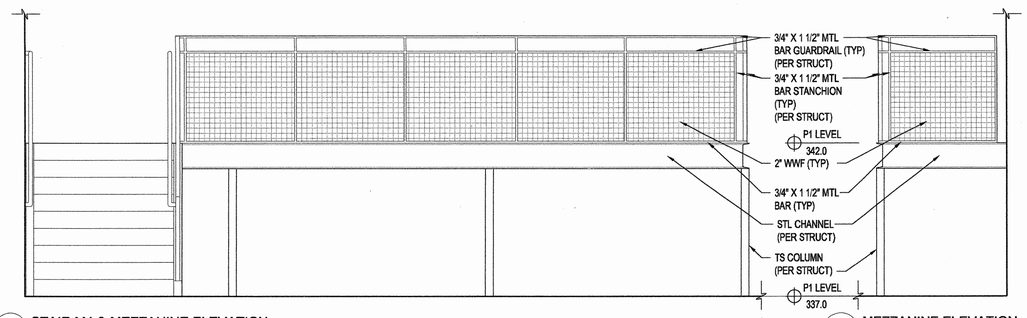

28 STAIR M4 & MEZZANINE ELEVATION
1/2" = 1'- 0"

30 MEZZANINE ELEVATION
1/2" = 1'- 0"

MITHUN
Architects+Designers+Planners
Pier 56
1201 Alaskan Way
Suite 200
Seattle, WA 98101
TEL 206 623.3344
FAX 206 623.7005

PROJECT:
200 W. Highland Drive
LOCATION:
202 W. Highland Drive
Seattle, WA 98119

PREPARED FOR:
Lorig Associates, LLC
2025 First Avenue, Suite 420
Seattle WA, 98121
T= 206.728.7660


NO.	DATE	REVISION


PROJECT DIRECTOR: JB
PROJECT MANAGER: EMD
PROJECT ARCHITECT: BB
PROJECT TEAM MEMBERS: ML, ML
CHECK:

ARCHITECT SEAL
3689 REGISTERED ARCHITECT BRUCE L. WILLIAMS STATE OF WASHINGTON

TITLE
STAIR SECTIONS & DETAILS

PROJECT NO. 04470.00
DATE 04-02-07
PROJECT NETWORK PATH S:\ 2005\0447000\Cadd\
A\SHEETS
SHEET NUMBER
A6.03
CONTRACT DOCUMENTS
© 2004 MITHUN, INC.

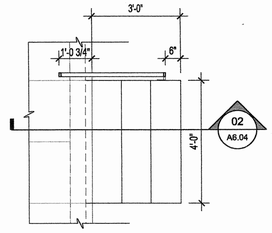

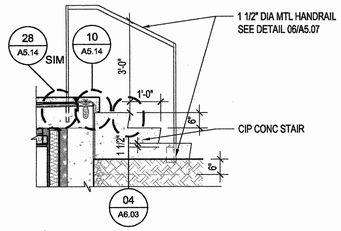

RFI #2 STAIR M5 CHANGES


RFI #105 MAINTENANCE STAIR DRAIN

RFI #118 M5 STAIR DIMENSION

01 STAIR PLAN @ R2 LEVEL
1/2" = 1'-0"


N

02 STAIR SECTION @ R2 LEVEL
1/2" = 1'-0"

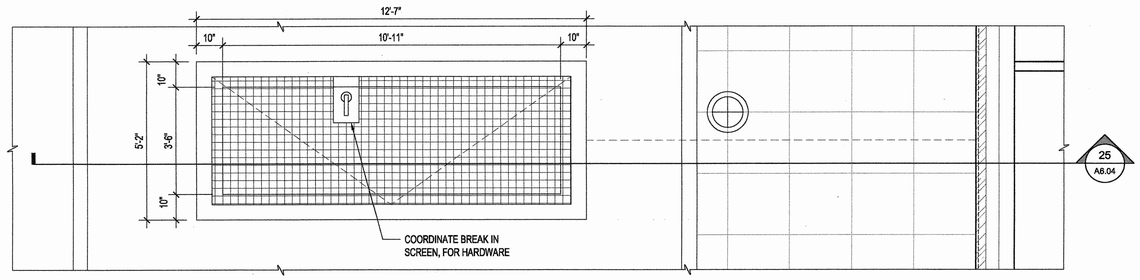


07 STAIR M5 PLAN @ R1 LEVEL
1/2" = 1'-0"

N

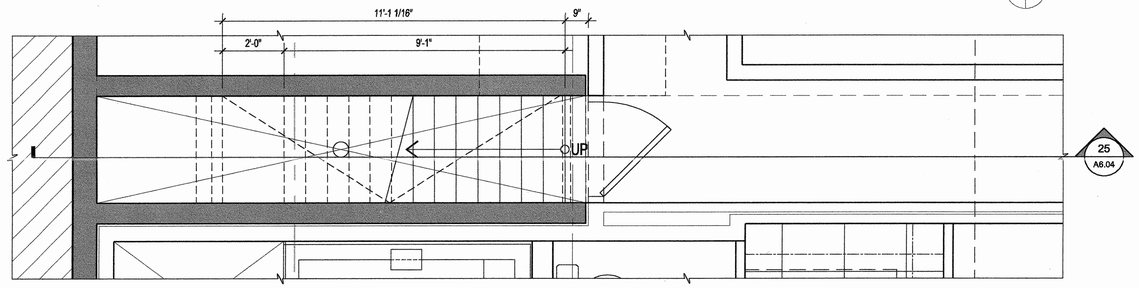


13 STAIR M5 PLAN @ P1 LEVEL
1/2" = 1'-0"

N

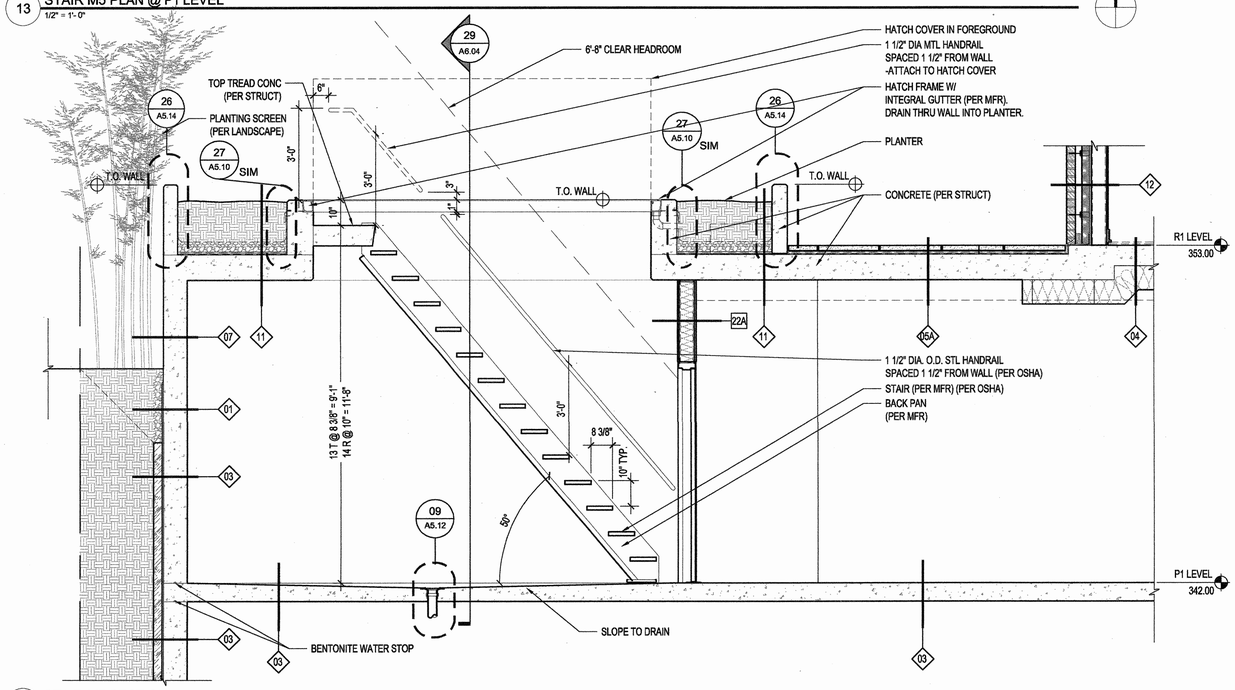

25 STAIR M5 SECTION
1/2" = 1'-0"

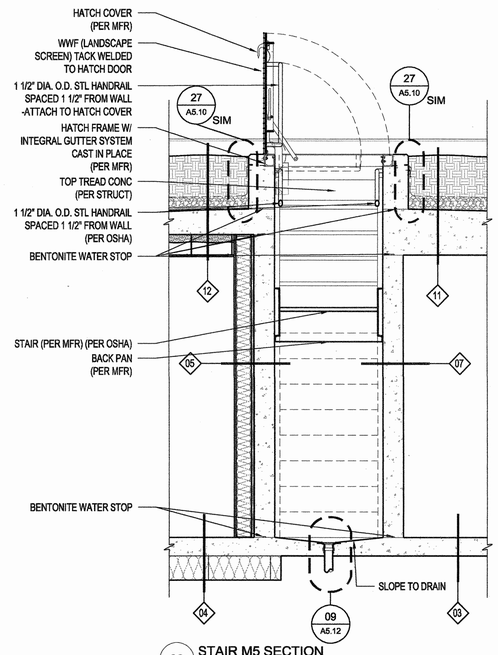

29 STAIR M5 SECTION
1/2" = 1'-0"

MITHUN
Architects+Designers+Planners

Pier 56
1201 Alaskan Way
Suite 200
Seattle, WA 98101
TEL 206 623.3344
FAX 206 623.7005

200 West Highland

PROJECT:
200 W. Highland Drive

LOCATION:
202 W. Highland Drive
Seattle, WA 98119

PREPARED FOR:
Lorig Associates, LLC
2025 First Avenue, Suite 420
Seattle WA. 98121
T= 206.728.7660

200 West Highland

NO.	DATE	REVISION

PROJECT DIRECTOR
JB
PROJECT MANAGER
EMD
PROJECT ARCHITECT
BB
PROJECT TEAM MEMBERS
ML, ML
CHECK

ARCHITECT SEAL

3689 REGISTERED ARCHITECT
BRUCE L. WILLIAMS
STATE OF WASHINGTON

TITLE
STAIR SECTIONS
& DETAILS

PROJECT NO.
04470.00
DATE
04-02-07
PROJECT NETWORK PATH
S:\ 2005\0447000\Cadd\
A\SHEETS
SHEET NUMBER
A6.04
CONTRACT DOCUMENTS

© 2004 MITHUN, INC.

ASI #13 MAILROOM CHANGES

ASI #31 MECHANICAL FANS IN SECONDARY BATHS

RFI #99 CEILING HEIGHTS


ASI #66 Mirror, electrical, data port layout

RFI #245 Ceiling Heights

ASI #84 Ceiling Framing, Down Lights, Wall Washers

RFI #344 Drop Header Heights @ Common Areas

RFI #368 Main Entry Soffit Light Change

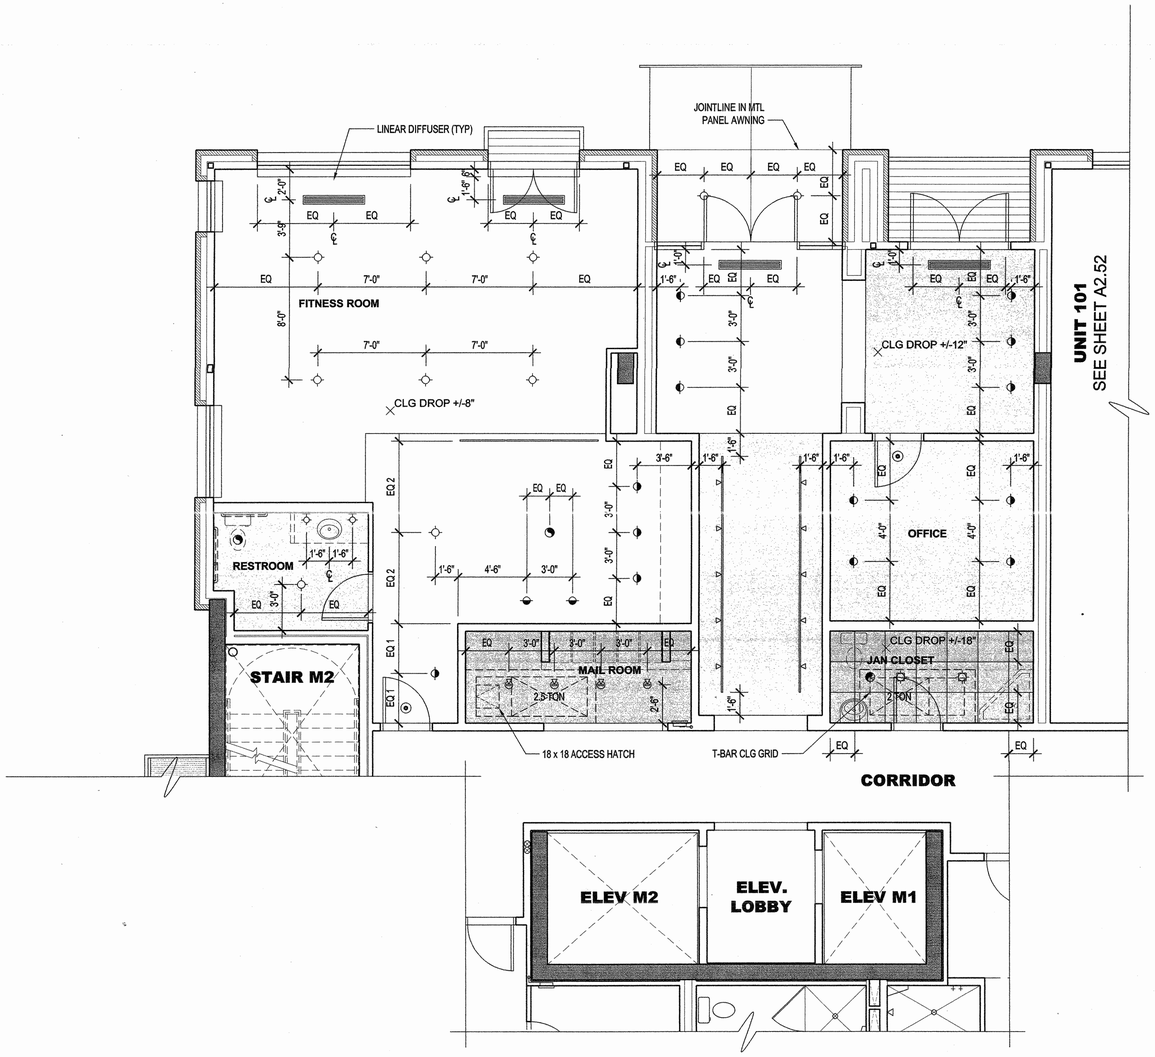

NOTE:
CEILING DROPS ARE TAKEN FROM BOTTOM OF PT SLAB

RCP PLAN LEGEND

01 SOFFIT DEPTHS ARE TAKEN FROM BOTTOM OF SLAB OR DROP SLAB; WHICHEVER IS LOWER TO BOTTOM OF SOFFIT FRAMING

02 LINEAR DIFFUSERS ARE TO BE PLACED 16" FROM INT. FACE OF FRAMED WALL; UNLESS OTHERWISE NOTED.

03 W.I.C. CLOSET LIGHTS ARE CENTERED IN ROOM BETWEEN INT. FACE OF WALL & FRONT FACE OF CLOSET SHELVING; WICHEVER IS CLOSER.

04 LINEAR CLOSET LIGHTS SHALL BE PLACED ON WALL CENTERED HORIZ. ON THE DOOR OPENING AND VERT. ON FINISHED CLG & HEAD OF DOOR OPENING.

05 SMOKE DETECTORS SHALL BE HARDWIRED AND BE PLACED ON WALL OVER DOOR; CENTERED HORIZ. ON DOOR OPENING & VERT. BTWN CLG & DOOR HEAD UNLESS OTHERWISE NOTED.

06 SURFACE MOUNTED LIGHTS & FANS ON T-BAR CLG GRID SHALL BE CENTERED ON SQ TILE AS SHOWN IN DWG.

07 LOCATE ELEC. UNIT PANEL BEHIND LAUNDRY DOOR UNLESS PANEL IS LOCATED ON OTHER WALL PER DWG.

ELECTRICAL LEGEND

- RECESSED LIGHT I.C. RATED WHERE REQ'D
- RECESSED WALL-WASHER I.C. RATED WHERE REQ'D
- WALL - MOUNT LIGHT
- STEP LIGHT
- CEILING - MOUNT LIGHT
- PENDANT LIGHT
- FLOOR MOUNTED UP-LIGHT
- LOW VOLTAGE TRACK LIGHTING
- LOW VOLTAGE MONOPOINT
- LINEAR FLUORESCENT
- STRIP LIGHT
- FLUORESCENT LIGHT
- EMERGENCY STAIR LIGHT
- EMERGENCY CORRIDOR LIGHT
- FAN / LIGHT
- BULB HEATER
- JUNCTION BOX
- EXHAUST FAN - V.T.O.S.
- SMOKE DETECTOR W/ BATTERY BACK-UP & AUDIBLE ALARM
- SWITCH
- SWITCH- 3 WAY
- SWITCH- 4 WAY
- TIMER SWITCH
- DIMMER SWITCH
- DIMMER SWITCH- 3 WAY
- TIMER / DIMMER SWITCH
- 110v OUTLET
- 220v HEAVY DUTY OUTLET
- GFI OUTLET
- WATERPROOF GFI OUTLET
- SWITCHED OUTLET
- FLOOR MOUNTED SWITCH
- SWITCHED FLOOR MOUNTED SWITCH
- SPECIAL PURPOSE
- CABLE T.V.
- TELEPHONE
- DATA
- DOORBELL CHIME
- DOORBELL
- THERMOSTAT

CEILING LEGEND

- LOW DROPPED CEILING
- STANDARD DROPPED CEILING
- HIGH DROPPED CEILING
- CLERESTORY CEILING
- CEILING PLENUM

RCP: LOBBY, FITNESS & BUILDING SERVICES
1/4" = 1'-0"

0' 2.5' 5' 10' 25'

MITHUN
Architects+Designers+Planners

Pier 56
1201 Alaskan Way
Suite 200
Seattle, WA 98101
TEL 206 623.3344
FAX 206 623.7005

202 highland drive

PROJECT:
200 W. Highland Drive

LOCATION:
202 W. Highland Drive
Seattle, WA 98119

PREPARED FOR:
Lorig Associates, LLC
2025 First Avenue, Suite 420
Seattle WA. 98121
T= 206.728.7660

200 West Highland

NO.	DATE	REVISION
1	05-01-07	ADDENDUM-1

PROJECT DIRECTOR: JB JPB
PROJECT MANAGER: EMD
PROJECT ARCHITECT: BB
PROJECT TEAM MEMBERS: ML, ML
CHECK:

ARCHITECT SEAL

3689 REGISTERED ARCHITECT
BRUCE L. WILLIAMS
STATE OF WASHINGTON

TITLE: RCP: LOBBY, FITNESS & BUILDING SERVICES

PROJECT NO.: 04470.00
DATE: 04-02-07
PROJECT NETWORK PATH: S:\ 2005\0447000\Cadd\A\SHEETS

SHEET NUMBER: A7.51

ENTIRE SHEET REVISED

CONTRACT DOCUMENTS

© 2004 MITHUN, INC.