RFI #310 Fireplace Exhaust Flange @ R5

ASI #1 ELEVATION DOOR CHANGE

RFI #102 SNAP TIE LAYOUT

RFI #178 Riser hights at South entry

RFI #202 Building elevations

RFI #229 Balcony Deck Bottom of Slab Finish

RFI #230 2" Step in Brick Condition

RFI #241 Add. Rain Shields

RFI #209 Ext. Paint Colors and Locations

RFI #260 Main entry Stair Riser Size

RFI #310 Fireplace exhaust flange @ R5

RFI #365 FDC Location

RFI #232 Brick Module @ MN and MY window



01 SOUTH ELEVATION
1/8" = 1'-0"



02 EAST ELEVATION
1/8" = 1'-0"

ELEVATION NOTES

1	SIDING TYPE #1 - CAST IN PLACE (CIP) CONCRETE (CLEAR SEALER)
2	SIDING TYPE #2 - BRICK VENEER
3	SIDING TYPE #3 - CAST IN PLACE (CIP) CONCRETE (PAINTED)
4	SIDING TYPE #4 - COMPOSITE ALUM PANEL SIDING SYSTEM (COLOR 1)
5	SIDING TYPE #5 - COMPOSITE ALUM PANEL SIDING SYSTEM (COLOR 2)
6	CORNICE TYPE #1 - PRE-CAST CONCRETE
7	TRELLIS TYPE # 1 - PAINTED GALVANIZED STEEL FRAME W/ LAMINATED GLASS
8	AWNING - COMPOSITE ALUM PANEL SIDING SYSTEM W/ STL. FRAME (COLOR 1)
9	TRELLIS TYPE # 2 - PAINTED GALVANIZED STEEL FRAME W/ GRATING
10	WINDOW TYPE #1 - ALUMINUM WINDOW
11	DOOR TYPE # 1 -ALUMINUM DOOR IN ALUMINUM WINDOW FRAME
12	DOOR TYPE # 2 - STEEL DOOR
13	DOOR TYPE #3 - SECTIONAL OVERHEAD ALUMINUM GATE
14	PAINTED GALVANIZED STEEL LINTEL
15	PAINTED ALUMINUM CHANNEL DECK FASCIA
16	PRECAST CONCRETE SILL
17	PRECAST CONCRETE CAP
18	PRE-FINISHED METAL FLASHING
19	PAINTED ALUMINUM GUARDRAIL
20	WOOD TOP-RAIL
21	PAINTED ALUMINUM GATE
22	SIDING TYPE #6 - HORIZONTAL PROFILED METAL PANEL (COLOR 1)
23	SS FIREPLACE VENT
24	SS FRESH AIR INTAKE VENT
25	EXTERIOR WALL SCONCE
26	ALUM RAIN SHIELD (COLOR 1)
27	BRICK LEDGER W/ 3/4" SOFTJOINT (TO MATCH MORTAR COLOR)
28	SS COMBUSTION AIR INTAKE FOR FIREPLACE

MITHUN
Architects+Designers+Planners
Pier 56
1201 Alaskan Way
Suite 200
Seattle, WA 98101
TEL 206 623.3344
FAX 206 623.7005

PROJECT:
200 W. Highland Drive

LOCATION:
202 W. Highland Drive
Seattle, WA 98119

PREPARED FOR:
Lorig Associates, LLC
2025 First Avenue, Suite 420
Seattle WA. 98121
T= 206.728.7660

NO.	DATE	REVISION

PROJECT DIRECTOR: JB
PROJECT MANAGER: EMD
PROJECT ARCHITECT: BB
PROJECT TEAM MEMBERS: ML, ML
CHECK:


ARCHITECT SEAL:
3689 REGISTERED ARCHITECT BRUCE L. WILLIAMS STATE OF WASHINGTON

TITLE: EXT. BLDG ELEV.


PROJECT NO.: 04470.00
DATE: 04-02-07
PROJECT NETWORK PATH: S:_2005\0447000\Cadd\
A\SHEETS
SHEET NUMBER: A3.01

CONTRACT DOCUMENTS

© 2004 MITHUN, INC.

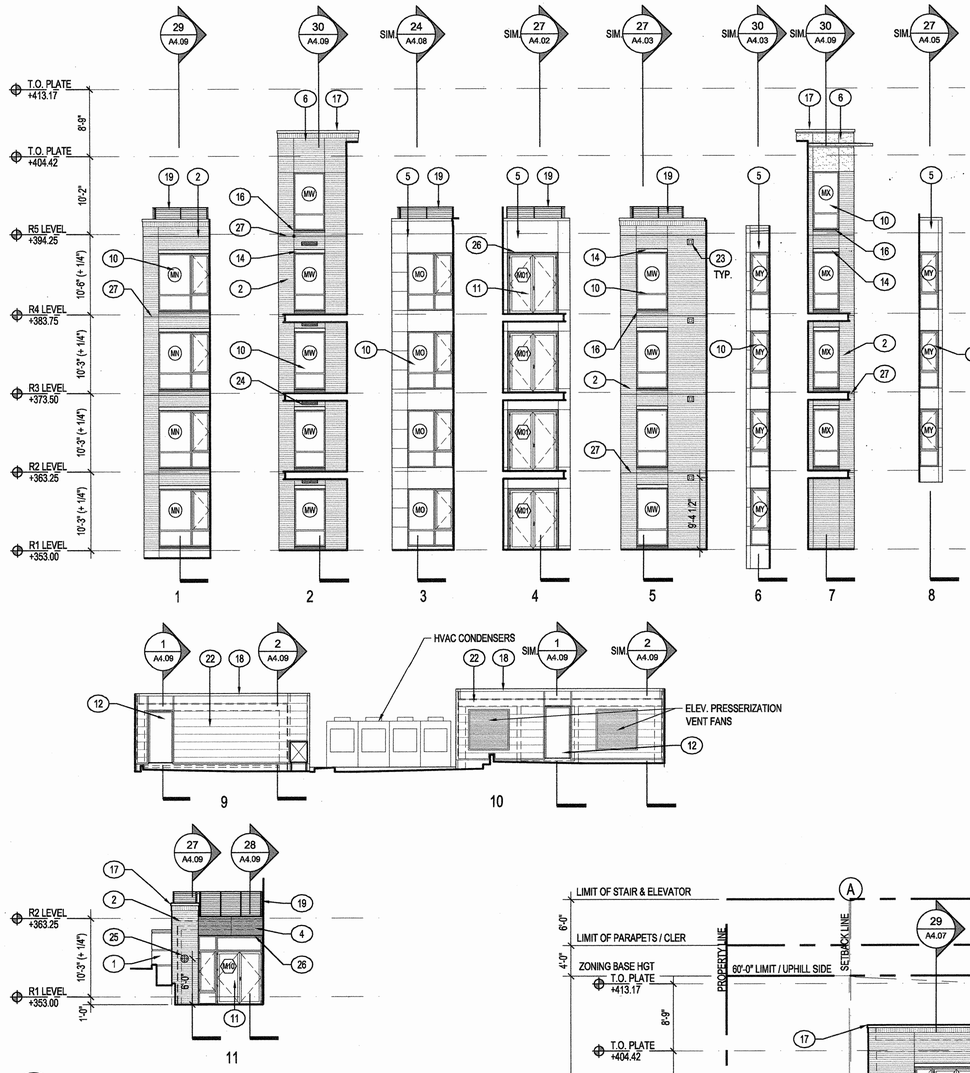

03 PARTIAL ELEVATIONS
1/8" = 1'-0"

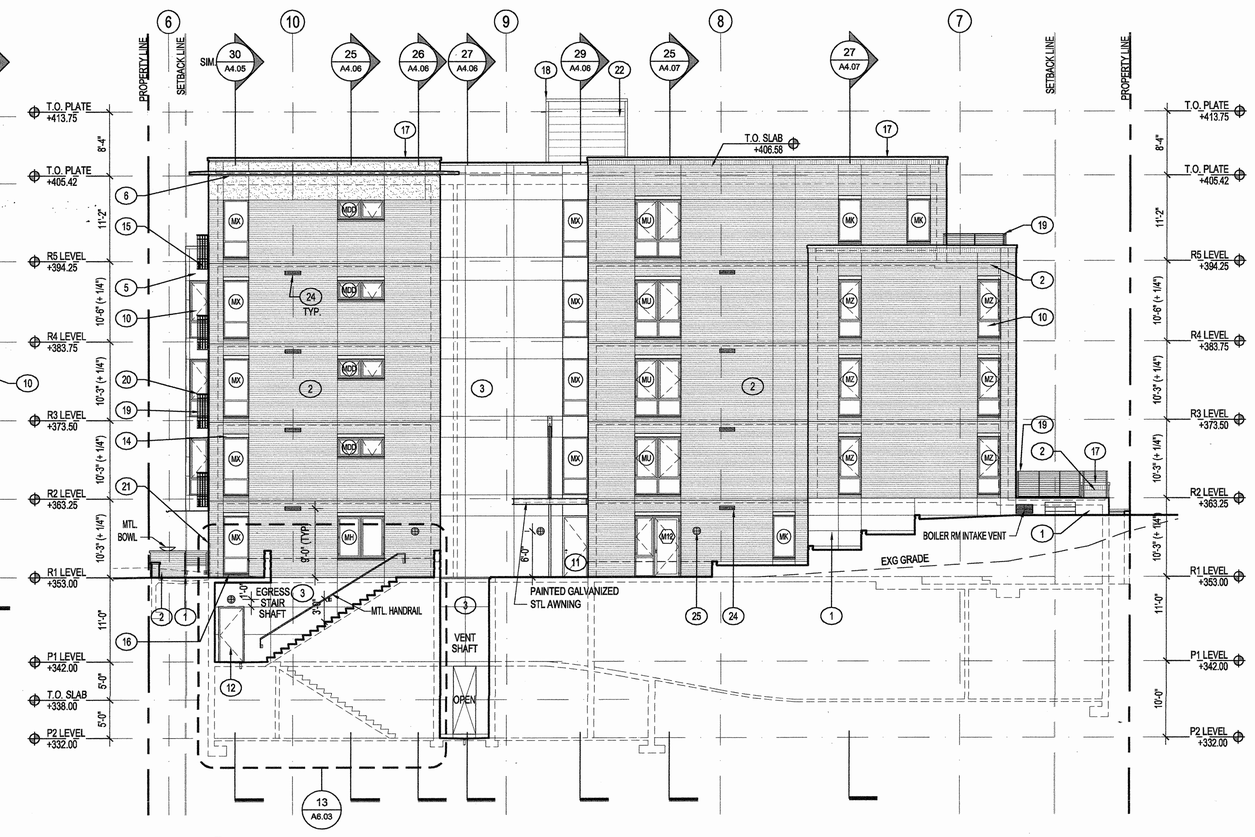

01 NORTH ELEVATION
1/8" = 1'-0"



02 WEST ELEVATION
1/8" = 1'-0"

ELEVATION NOTES

1	SIDING TYPE #1 - CAST IN PLACE (CIP) CONCRETE (CLEAR SEALER)
2	SIDING TYPE #2 - BRICK VENEER
3	SIDING TYPE #3 - CAST IN PLACE (CIP) CONCRETE (PAINTED)
4	SIDING TYPE #4 - COMPOSITE ALUM PANEL SIDING SYSTEM (COLOR 1)
5	SIDING TYPE #5 - COMPOSITE ALUM PANEL SIDING SYSTEM (COLOR 2)
6	CORNICE TYPE #1 - PRE-CAST CONCRETE
7	TRELLIS TYPE # 1 - PAINTED GALVANIZED STEEL FRAME W/ LAMINATED GLASS
8	AWNING - COMPOSITE ALUM PANEL SIDING SYSTEM W/ STL. FRAME (COLOR 1)
9	TRELLIS TYPE # 2 - PAINTED GALVANIZED STEEL FRAME W/ GRATING
10	WINDOW TYPE #1 - ALUMINUM WINDOW
11	DOOR TYPE # 1 -ALUMINUM DOOR IN ALUMINUM WINDOW FRAME
12	DOOR TYPE # 2 - STEEL DOOR
13	DOOR TYPE #3 - SECTIONAL OVERHEAD ALUMINUM GATE
14	PAINTED GALVANIZED STEEL LINTEL
15	PAINTED ALUMINUM CHANNEL DECK FASCIA
16	PRECAST CONCRETE SILL
17	PRECAST CONCRETE CAP
18	PRE-FINISHED METAL FLASHING
19	PAINTED ALUMINUM GUARDRAIL
20	WOOD TOP-RAIL
21	PAINTED ALUMINUM GATE
22	SIDING TYPE #6 - HORIZONTAL PROFILED METAL PANEL (COLOR 1)
23	SS FIREPLACE VENT
24	SS FRESH AIR INTAKE VENT
25	EXTERIOR WALL SCONCE
26	ALUM RAIN SHIELD (COLOR 1)
27	BRICK LEDGER W/ 3/4" SOFTJOINT (TO MATCH MORTAR COLOR)
28	SS COMBUSTION AIR INTAKE FOR FIREPLACE

MITHUN
Architects+Designers+Planners

Pier 56
1201 Alaskan Way
Suite 200
Seattle, WA 98101
TEL 206 623.3344
FAX 206 623.7005

PROJECT:
200 W. Highland Drive

LOCATION:
202 W. Highland Drive
Seattle, WA 98119

PREPARED FOR:
Lorig Associates, LLC
2025 First Avenue, Suite 420
Seattle WA, 98121
T= 206.728.7660

NO.	DATE	REVISION

PROJECT DIRECTOR: JB
PROJECT MANAGER: EMD
PROJECT ARCHITECT: BB
PROJECT TEAM MEMBERS: ML, ML
CHECK:

ARCHITECT SEAL

3689 REGISTERED ARCHITECT
BRUCE L. WILLIAMS
STATE OF WASHINGTON

TITLE
EXT. BLDG ELEV.


PROJECT NO.
04470.00
DATE
04-02-07
PROJECT NETWORK PATH
S:\ 2005\0447000\Cadd\
A\SHEETS
SHEET NUMBER
A3.02

CONTRACT DOCUMENTS


© 2004 MITHUN, INC.

RFI #189 Plinth Wall Waterproofing @ Garage

ASI #32 RAILING AT DRIVEWAY

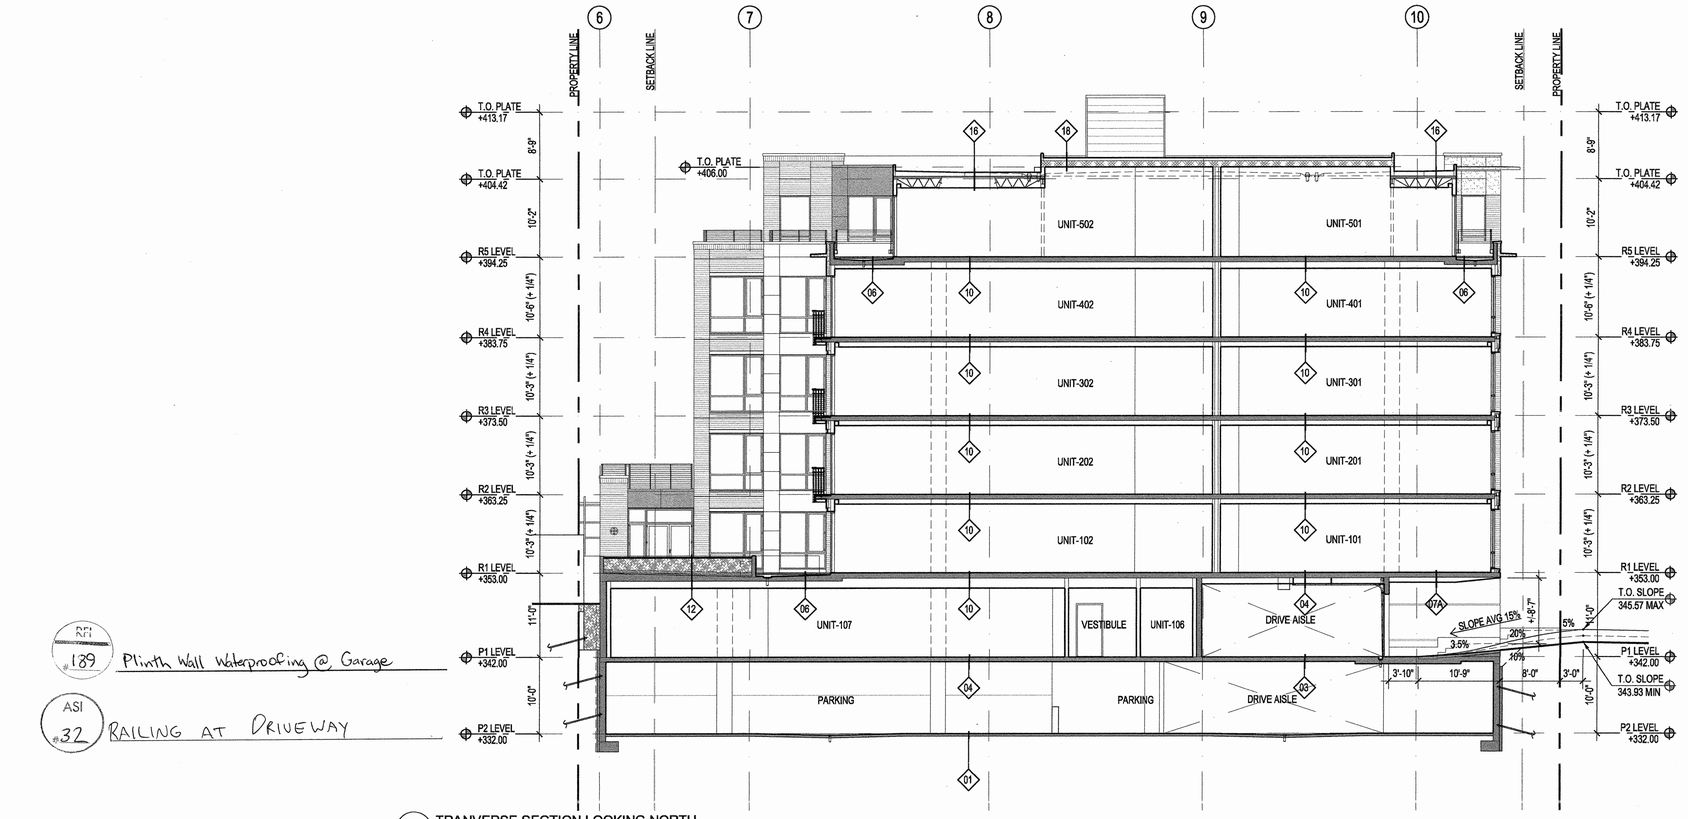

01 TRANVERSE SECTION LOOKING NORTH
1/8" = 1'-0"

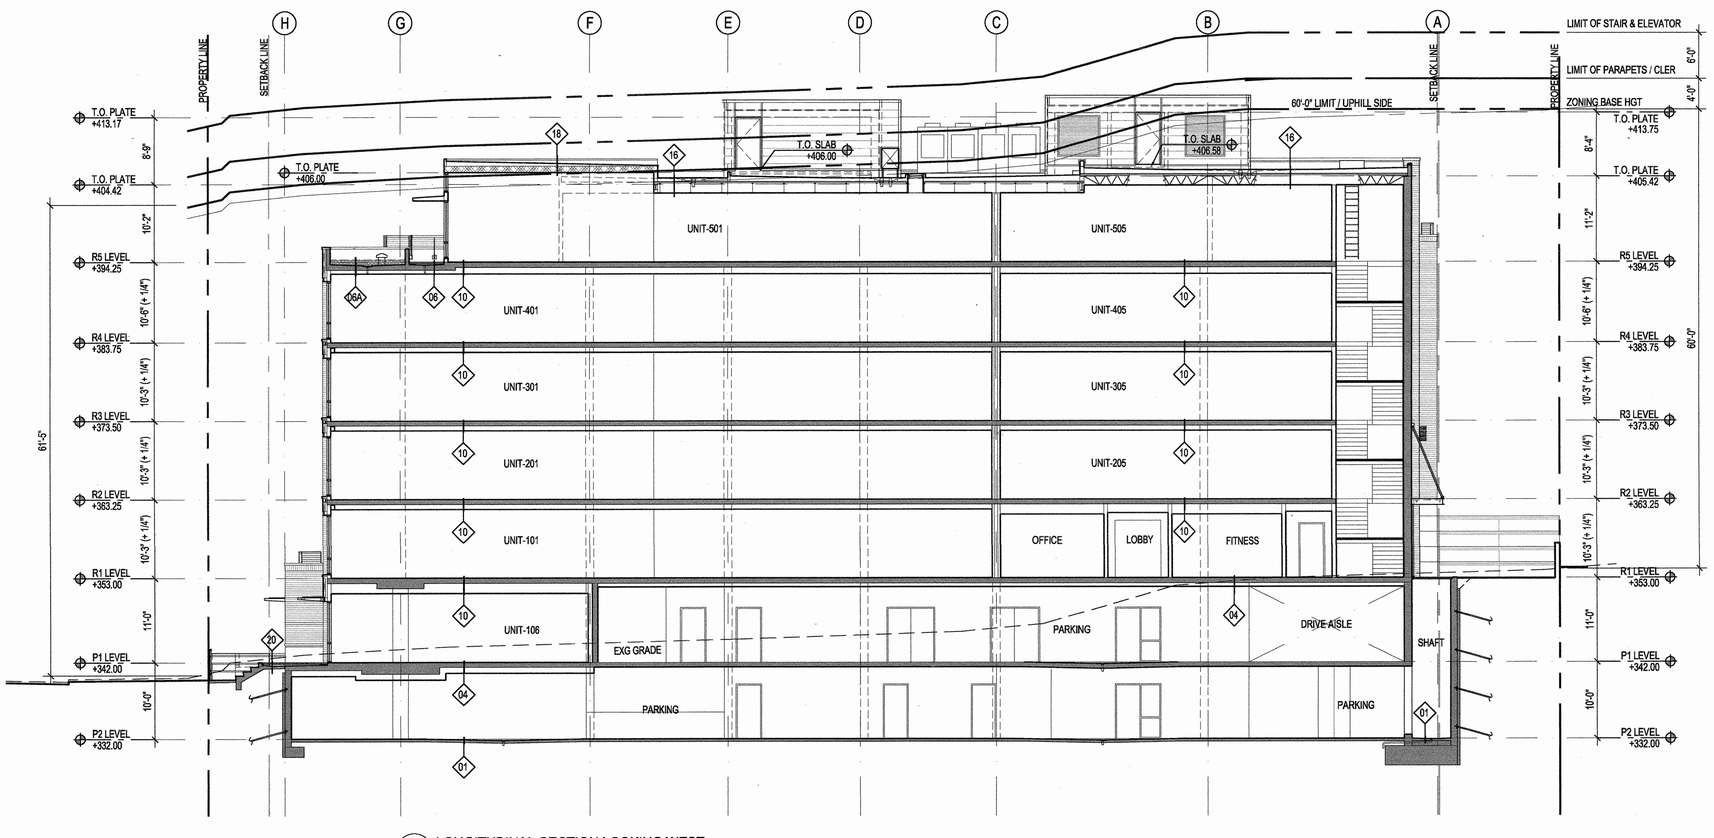

02 LONGITUDINAL SECTION LOOKING WEST
1/8" = 1'-0"

NOTE:
SEE SHT. A5.02 FOR FLOOR AND ROOF ASSEMBLIES

SECTION MATERIALS

- CAST IN PLACE (CIP) CONCRETE
- BRICK VENEER
- PRE-CAST CONCRETE PANEL (ASSEMBLY 1)
- PRE-CAST CONCRETE PANEL (ASSEMBLY 2)
- LIGHT-GAUGE METAL FRAMING

MITHUN
Architects+Designers+Planners
Pier 56
1201 Alaskan Way
Suite 200
Seattle, WA 98101
TEL 206 623.3344
FAX 206 623.7005

PROJECT:
200 W. Highland Drive

LOCATION:
202 W. Highland Drive
Seattle, WA 98119

PREPARED FOR:
Lorig Associates, LLC
2025 First Avenue, Suite 420
Seattle WA. 98121
T= 206.728.7660

200 West Highland

NO.	DATE	REVISION

PROJECT DIRECTOR: JB
PROJECT MANAGER: EMD
PROJECT ARCHITECT: BB
PROJECT TEAM MEMBERS: ML, ML
CHECK:

ARCHITECT SEAL:
3689 REGISTERED ARCHITECT
BRUCE L. WILLIAMS
STATE OF WASHINGTON

TITLE: BLDG SECTIONS


PROJECT NO.: 04470.00
DATE: 04-02-07
PROJECT NETWORK PATH: S:\ 2005\0447000\Cadd\A\SHEETS
SHEET NUMBER: A3.11

CONTRACT DOCUMENTS


© 2004 MITHUN, INC.

RFI #35 WATERPROOFING AT ELEVATOR PTNG.

RFI #62 NORTH RAMP DESIGN

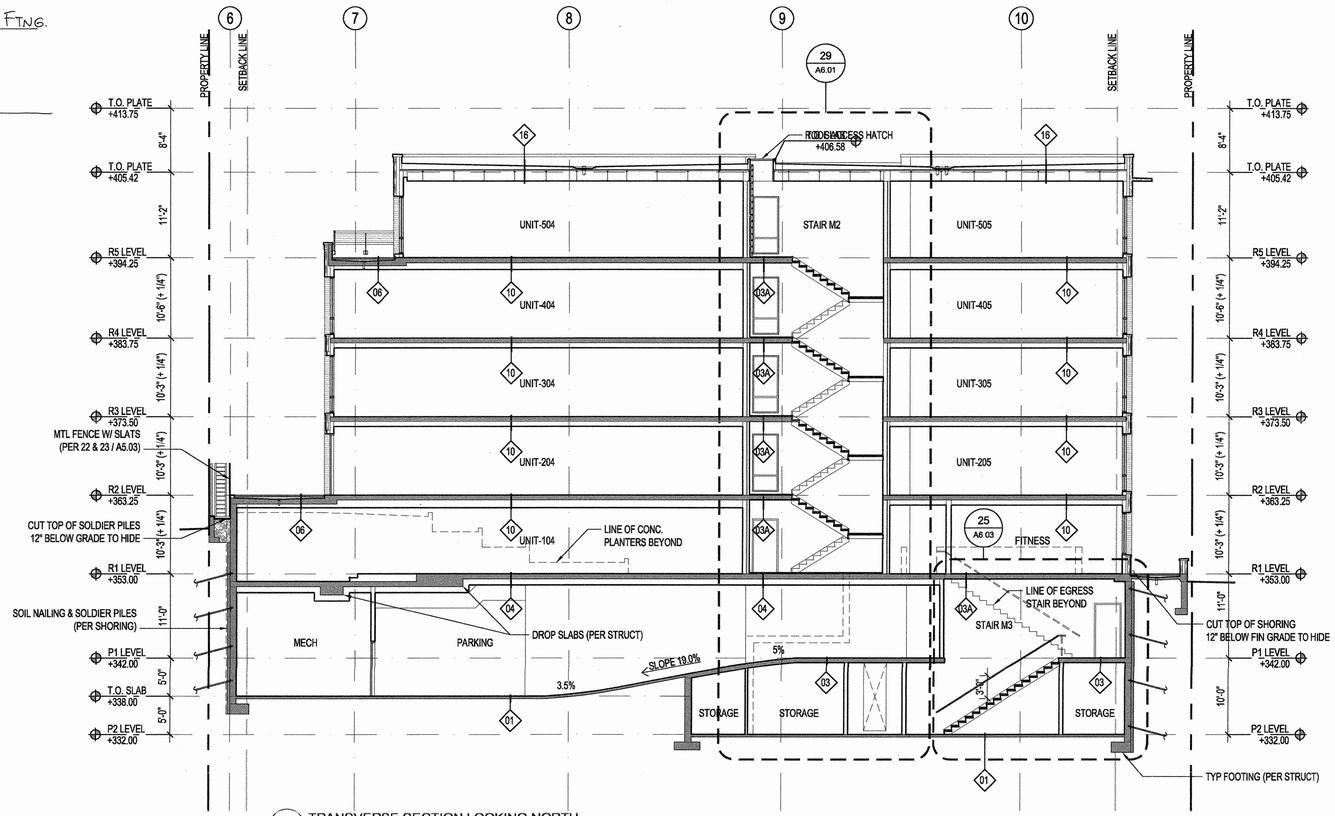

01 TRANSVERSE SECTION LOOKING NORTH
1/8" = 1'-0"

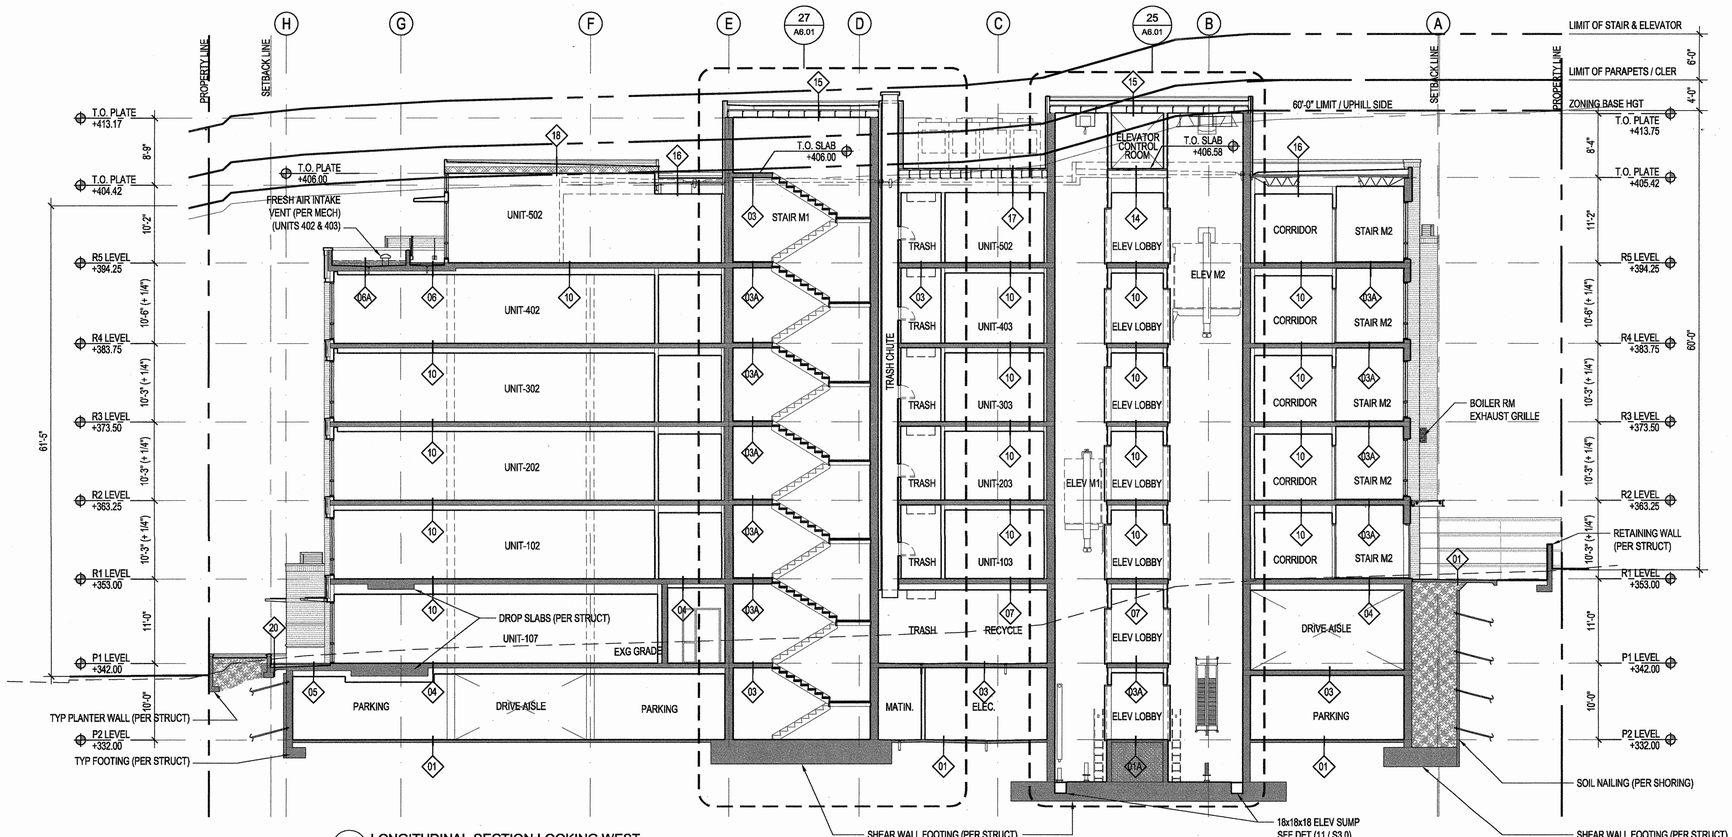

02 LONGITUDINAL SECTION LOOKING WEST
1/8" = 1'-0"

NOTE:
SEE SHT. A5.02 FOR FLOOR AND ROOF ASSEMBLIES

SECTION MATERIALS

- CAST IN PLACE (CIP) CONCRETE
- BRICK VENEER
- PRE-CAST CONCRETE PANEL (ASSEMBLY 1)
- PRE-CAST CONCRETE PANEL (ASSEMBLY 2)
- LIGHT-GAUGE METAL FRAMING

MITHUN
Architects+Designers+Planners
Pier 56
1201 Alaskan Way
Suite 200
Seattle, WA 98101
TEL 206 623.3344
FAX 206 623.7005

PROJECT:
200 W. Highland Drive

LOCATION:
202 W. Highland Drive
Seattle, WA 98119

PREPARED FOR:
Lorig Associates, LLC
2025 First Avenue, Suite 420
Seattle WA, 98121
T= 206.728.7660

NO. DATE REVISION

PROJECT DIRECTOR
JB
PROJECT MANAGER
EMD
PROJECT ARCHITECT
BB
PROJECT TEAM MEMBERS
ML, ML
CHECK


ARCHITECT SEAL
3689 REGISTERED ARCHITECT
BRUCE L. WILLIAMS
STATE OF WASHINGTON

TITLE
BLDG SECTIONS


PROJECT NO.
04470.00
DATE
04-02-07
PROJECT NETWORK PATH
S:\ 2005\0447000\Cadd\
A\SHEETS
SHEET NUMBER
A3.12

CONTRACT DOCUMENTS

© 2004 MITHUN, INC.

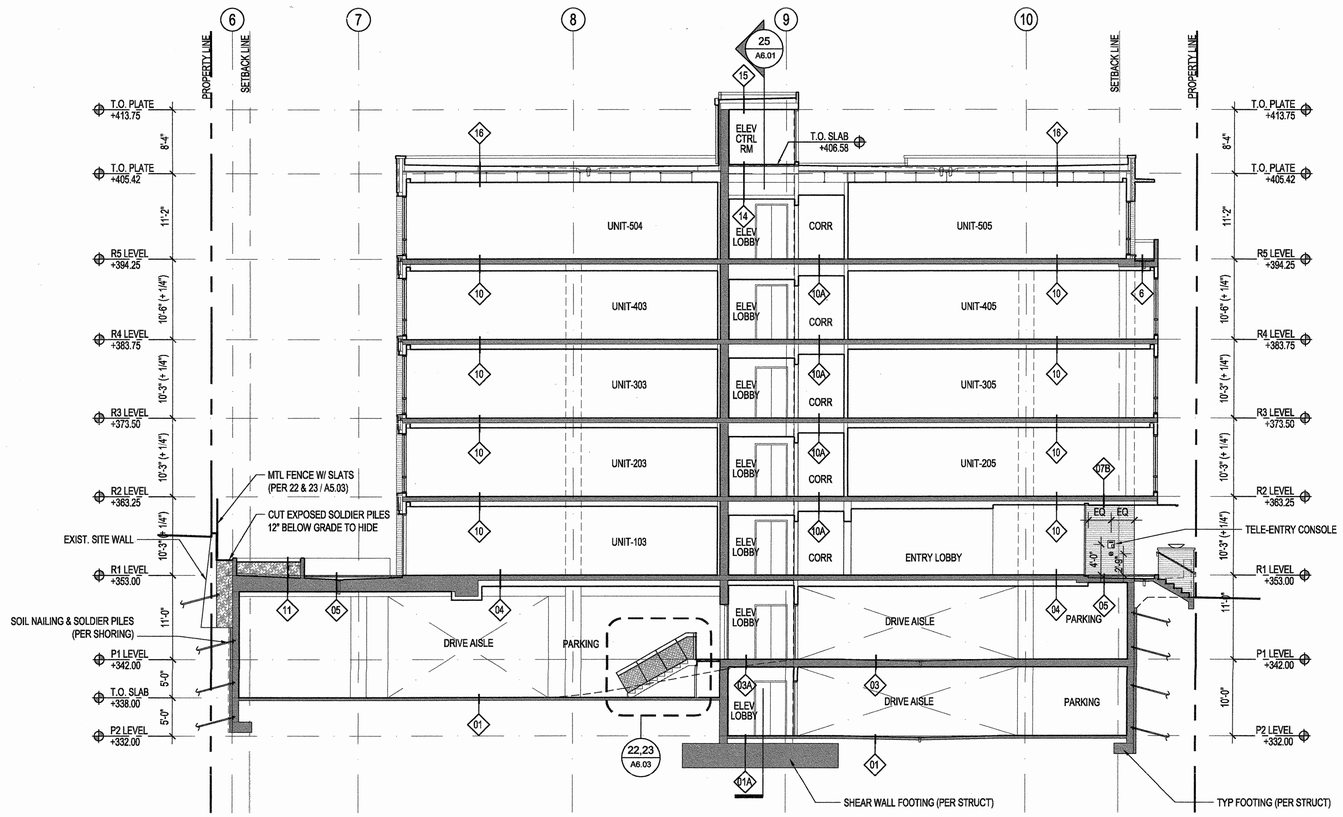

01 TRANSVERSE SECTION LOOKING NORTH
1/8" = 1'-0"

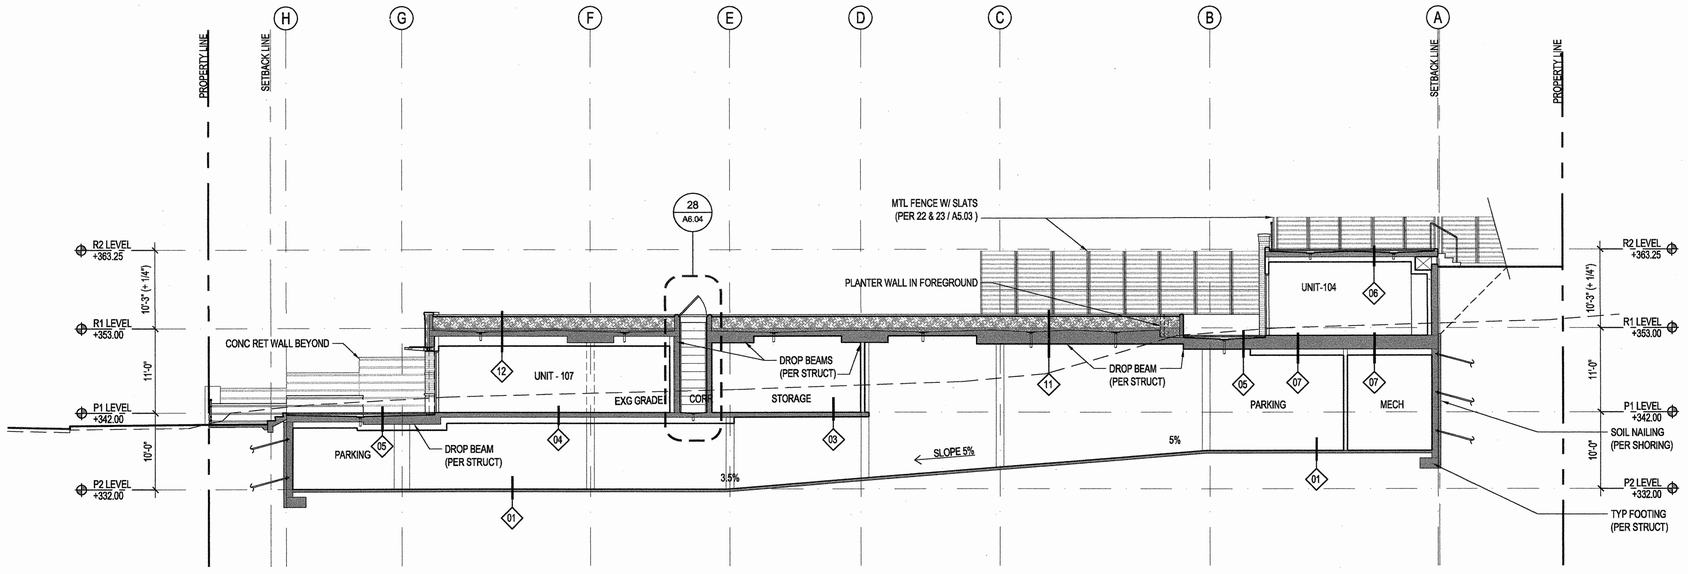

02 LONGITUDINAL SECTION THROUGH MID-RISE COURT LOOKING WEST
1/8" = 1'-0"

NOTE:
SEE SHT. A5.02 FOR FLOOR AND ROOF ASSEMBLIES

SECTION MATERIALS

- CAST IN PLACE (CIP) CONCRETE
- BRICK VENEER
- PRE-CAST CONCRETE PANEL (ASSEMBLY 1)
- PRE-CAST CONCRETE PANEL (ASSEMBLY 2)
- LIGHT-GAUGE METAL FRAMING

MITHUN
Architects+Designers+Planners

Pier 56
1201 Alaskan Way
Suite 200
Seattle, WA 98101
TEL 206 623.3344
FAX 206 623.7005

202 W. Highland dr.

PROJECT:
200 W. Highland Drive

LOCATION:
202 W. Highland Drive
Seattle, WA 98119

PREPARED FOR:
Lorig Associates, LLC
2025 First Avenue, Suite 420
Seattle WA, 98121
T= 206.728.7660

200 West Highland

NO.	DATE	REVISION

PROJECT DIRECTOR: JB
PROJECT MANAGER: EMD
PROJECT ARCHITECT: BB
PROJECT TEAM MEMBERS: ML, ML
CHECK:

ARCHITECT SEAL

3689 REGISTERED ARCHITECT
BRUCE L. WILLIAMS
STATE OF WASHINGTON

TITLE
BLDG SECTIONS

PROJECT NO. 04470.00
DATE 04-02-07
PROJECT NETWORK PATH S:\ 2005\0447000\Cadd\
A\SHEETS
SHEET NUMBER **A3.13**

CONTRACT DOCUMENTS

© 2004 MITHUN, INC.