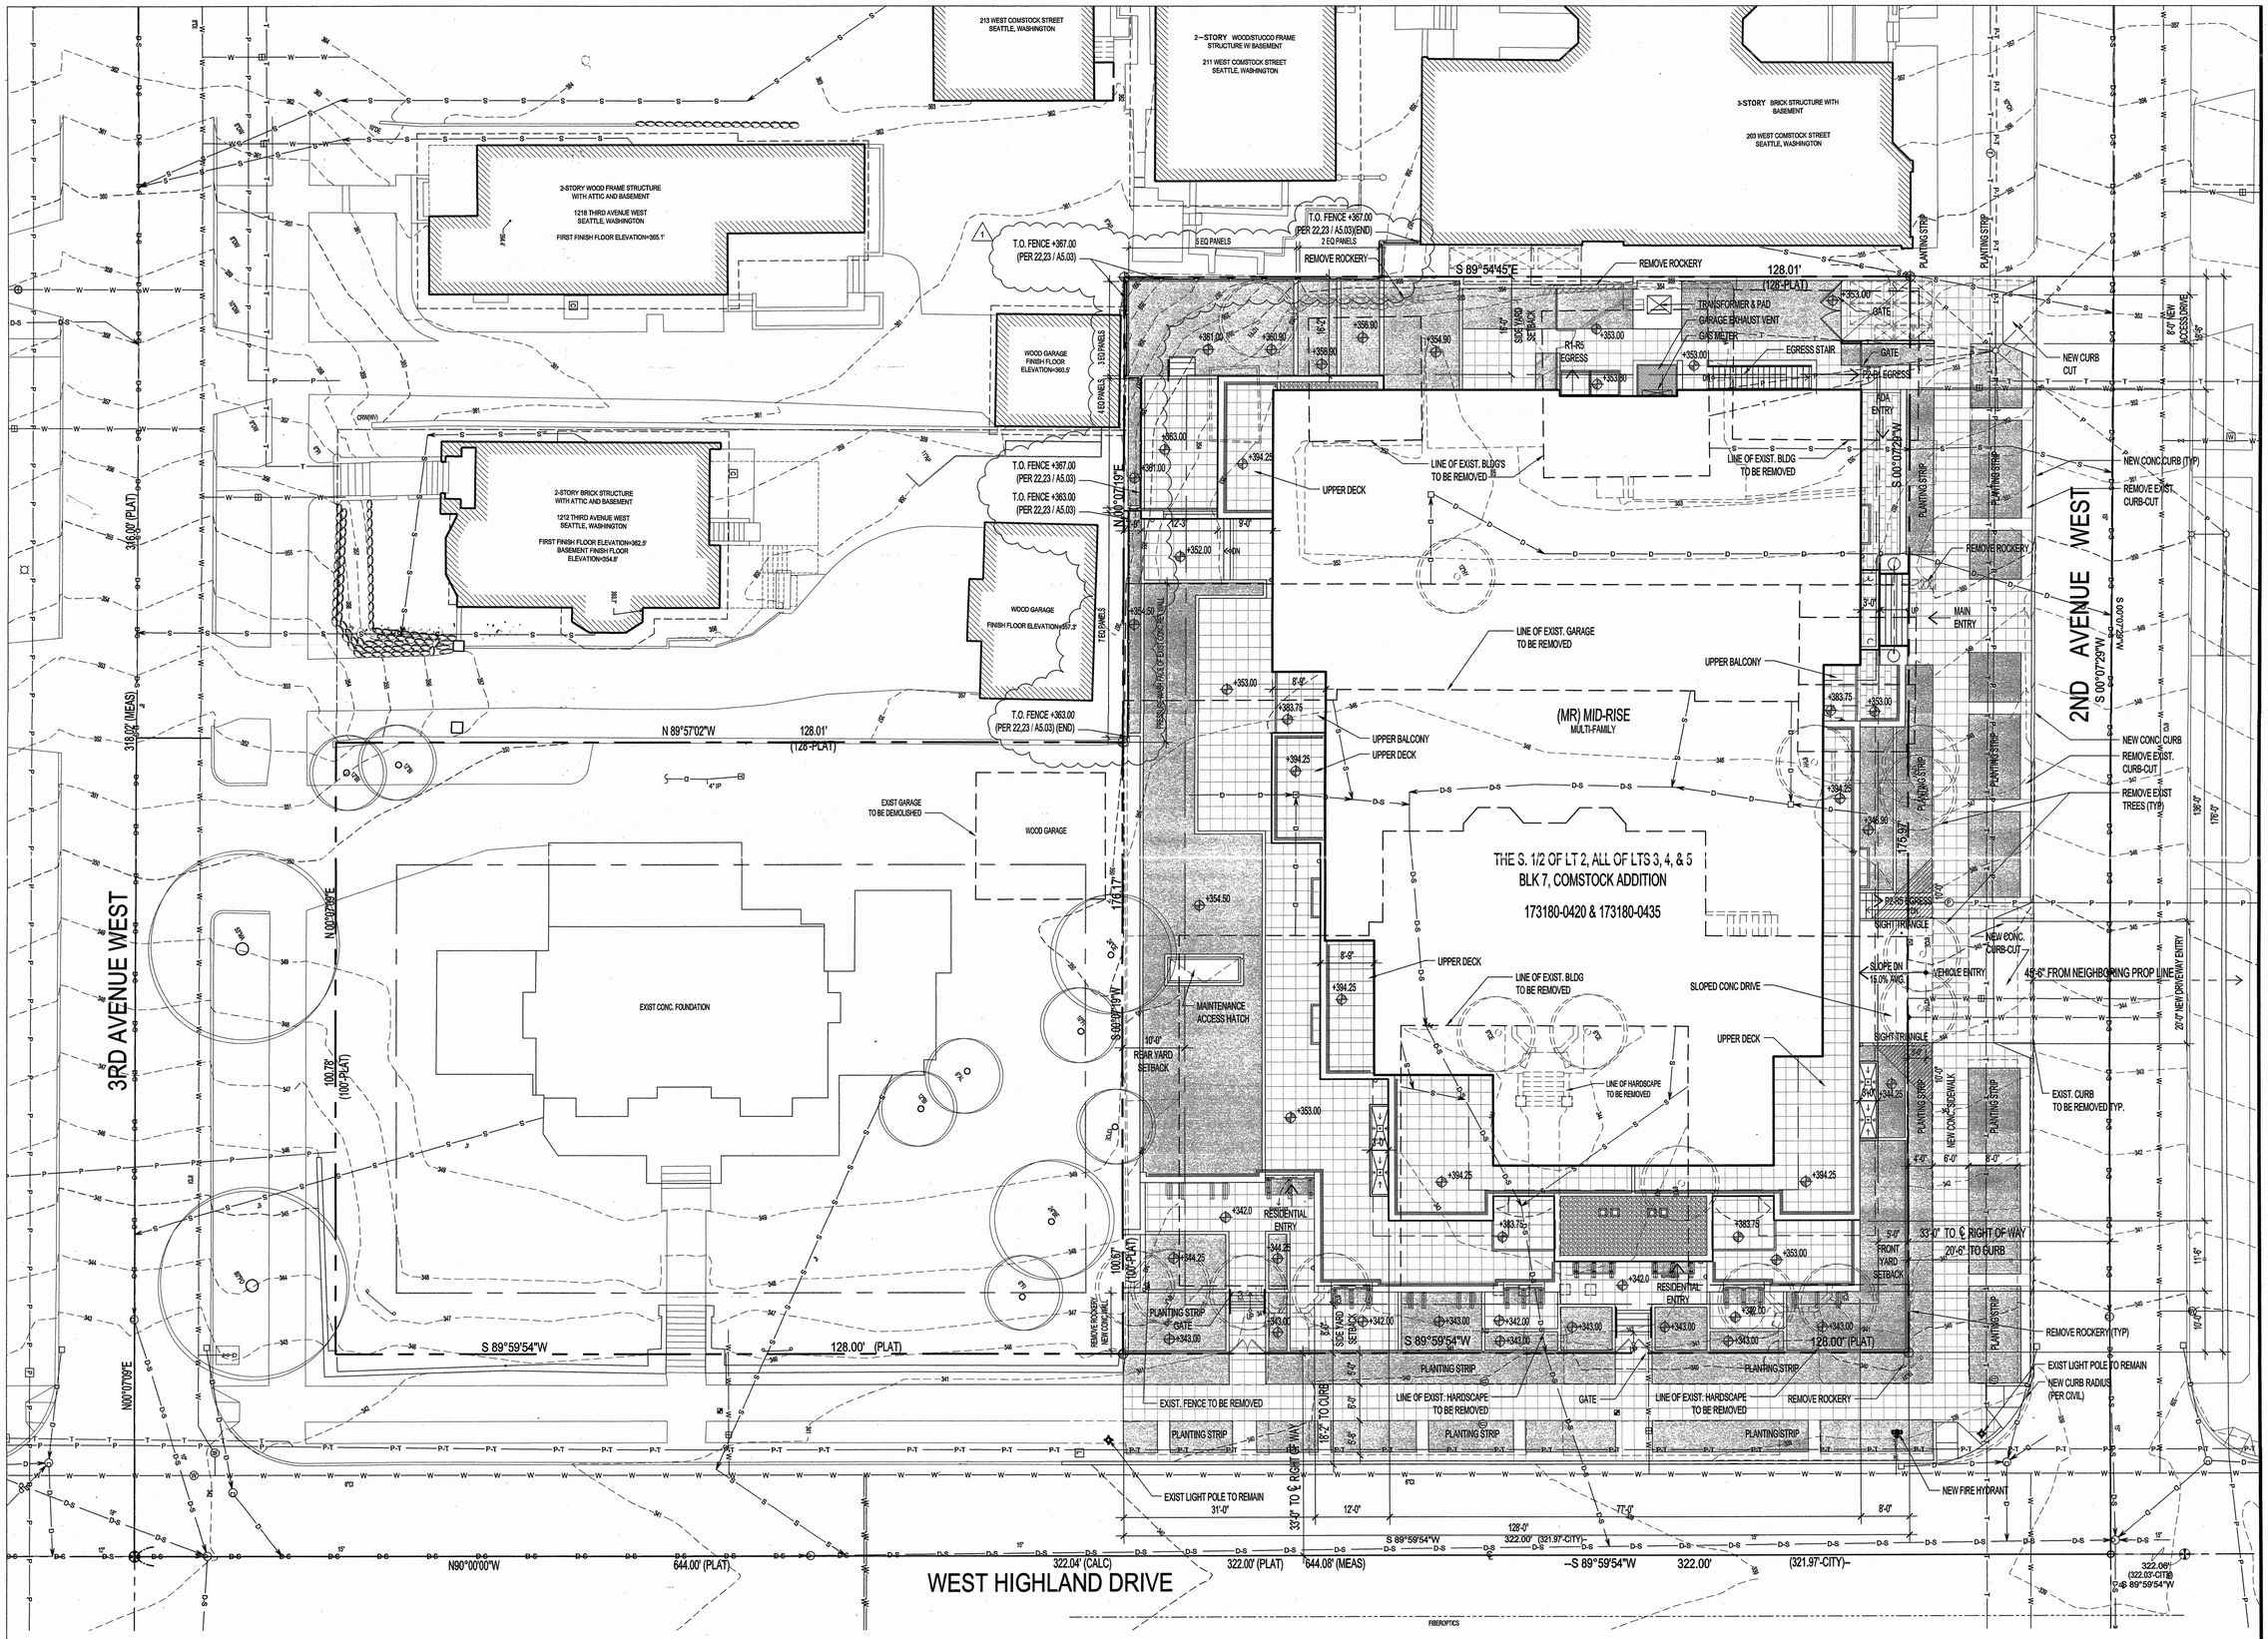


PLOT PLAN / SITE PLAN
1:10

NOTE:
1. PLOT PLAN GIVES SITE & OVERALL BUILDING DIMENSIONS - SEE ARCH. DRAWINGS SHEETS A2.01-A2.07 FOR BUILDING DIMENSIONS
2. SEE LANDSCAPE DRAWINGS FOR SIDEWALKS, TREES, & PLANTING STRIPS

ENTIRE SHEET REVISED

MITHUN
Architects+Designers+Planners

Pier 56
1201 Alaskan Way
Suite 200
Seattle, WA 98101
TEL 206 623.3344
FAX 206 623.7005

202 highland drive

PROJECT:
200 W. Highland Drive

LOCATION:
202 W. Highland Drive
Seattle, WA 98119

PREPARED FOR:
Lorig Associates, LLC
2025 First Avenue, Suite 420
Seattle WA. 98121
T= 206.728.7660

200 West Highland

NO.	DATE	REVISION
1	05-01-07	ADDENDUM-1

PROJECT DIRECTOR: JB
PROJECT MANAGER: EMD
PROJECT ARCHITECT: BB
PROJECT TEAM MEMBERS: ML, ML
CHECK:

ARCHITECT SEAL


3689 REGISTERED ARCHITECT
BRUCE L. WILLIAMS
STATE OF WASHINGTON

TITLE: PLOT PLAN/SITE PLAN

PROJECT NO.: 04470.00
DATE: 04-02-07
PROJECT NETWORK PATH: S:_2005\0447000\Cadd\
A\SHEETS
SHEET NUMBER: **A1.01**

CONTRACT DOCUMENTS


© 2004 MITHUN, INC.

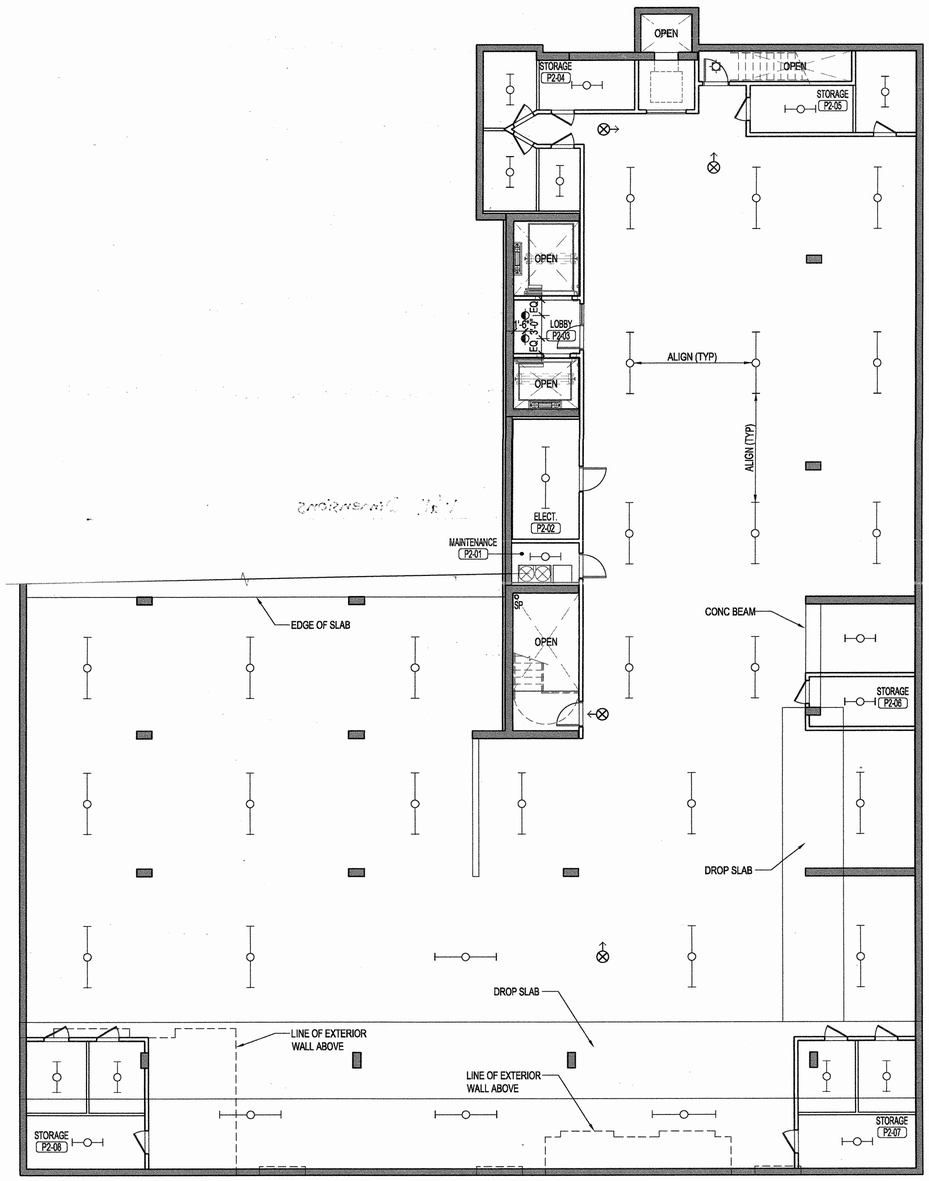

N

LEVEL P2 - RCP

1/8" = 1'-0"

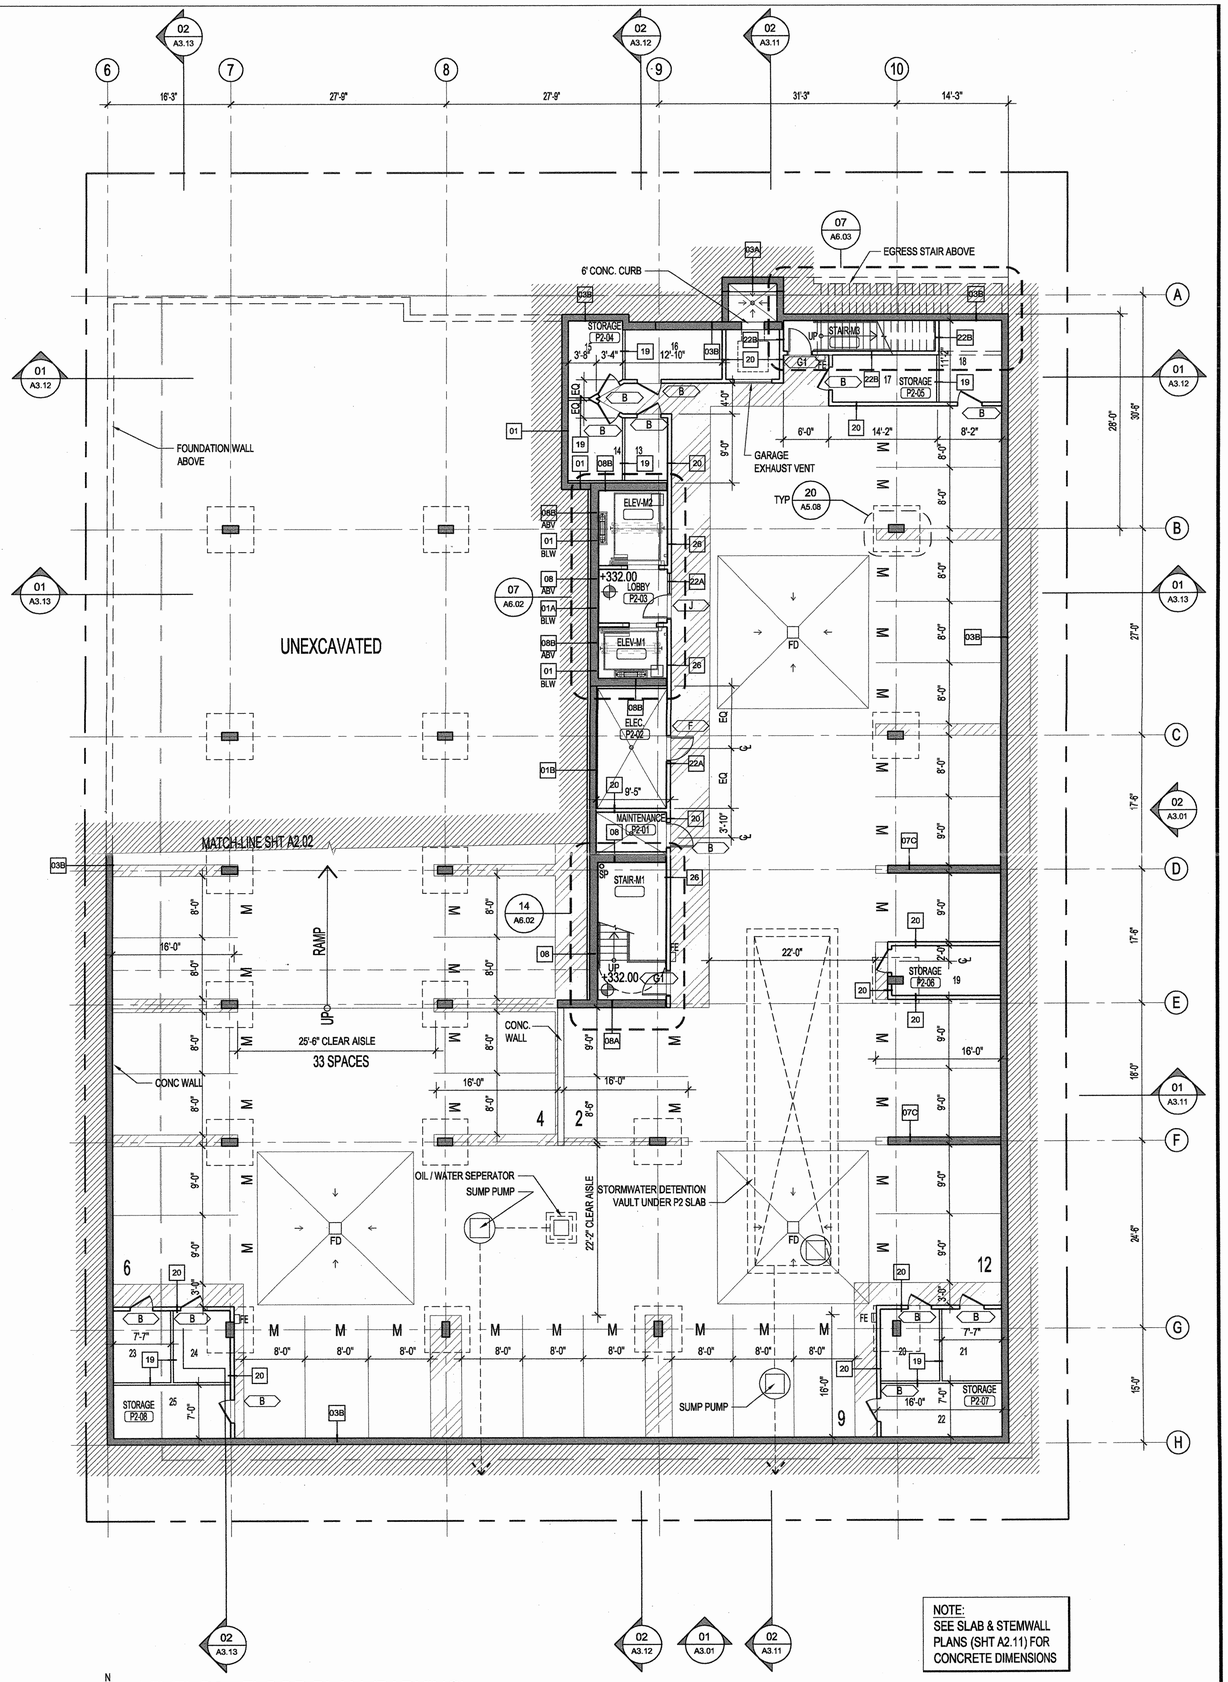

N

LEVEL P2 - FLOOR PLAN (PARKING)

1/8" = 1'-0"

0' 5' 10' 20' 50'

PLAN WALL SYMBOLS

- C.I.P. CONC WALL
- MASONRY VENEER
- PRECAST PANELS (ASSEMBLY 1)
- PRECAST PANELS (ASSEMBLY 2)
- MTL FRAMING

ELECTRICAL LEGEND

- RECESSED LIGHT I.C. RATED WHERE REQ'D
- RECESSED WALL-WASHER I.C. RATED WHERE REQ'D
- WALL - MOUNT LIGHT
- STEP LIGHT
- CEILING - MOUNT LIGHT
- PENDANT LIGHT
- LOW VOLTAGE TRACK LIGHTING
- FLOOR MOUNTED UP-LIGHT
- LOW VOLTAGE MONOPOINT
- LINEAR FLUORESCENT
- LED STRIP LIGHT
- FLUORESCENT LIGHT
- EMERGENCY STAIR LIGHT
- EMERGENCY CORRIDOR LIGHT
- FAN / LIGHT
- BULB HEATER
- JUNCTION BOX
- EXHAUST FAN - V.T.O.S.
- SMOKE DETECTOR W/ BATTERY BACKUP
- SWITCH
- SWITCH- 3 WAY
- TIMER SWITCH
- DIMMER SWITCH
- 110v OUTLET
- 220v HEAVY DUTY OUTLET
- GFI OUTLET
- WATERPROOF GFI OUTLET
- SWITCHED OUTLET
- FLOOR MOUNTED SWITCH
- SWITCHED FLOOR MOUNTED SWITCH
- SPECIAL PURPOSE
- CABLE T.V.
- TELEPHONE
- DATA
- DOORBELL CHIME
- DOORBELL
- THERMOSTAT

MITHUN
Architects+Designers+Planners

Pier 56
1201 Alaskan Way
Suite 200
Seattle, WA 98101
TEL 206 623.3344
FAX 206 623.7005

200 west highland

PROJECT:
200 W. Highland Drive

LOCATION:
202 W. Highland Drive
Seattle, WA 98119

PREPARED FOR:
Lorig Associates, LLC
2025 First Avenue, Suite 420
Seattle WA. 98121
T= 206.728.7660

200 West Highland

NO.	DATE	REVISION

PROJECT DIRECTOR: JB
PROJECT MANAGER: EMD
PROJECT ARCHITECT: BB
PROJECT TEAM MEMBERS: ML, ML
CHECK:

ARCHITECT SEAL


3689 REGISTERED ARCHITECT
BRUCE E. WILLIAMS
STATE OF WASHINGTON

TITLE
LEVEL P2 - PLAN & RCP

PROJECT NO.: 04470.00
DATE: 04-02-07
PROJECT NETWORK PATH: S:_2005\047000\Cadd\A\SHEETS
SHEET NUMBER: **A2.01**

CONTRACT DOCUMENTS

© 2004 MITHUN, INC.

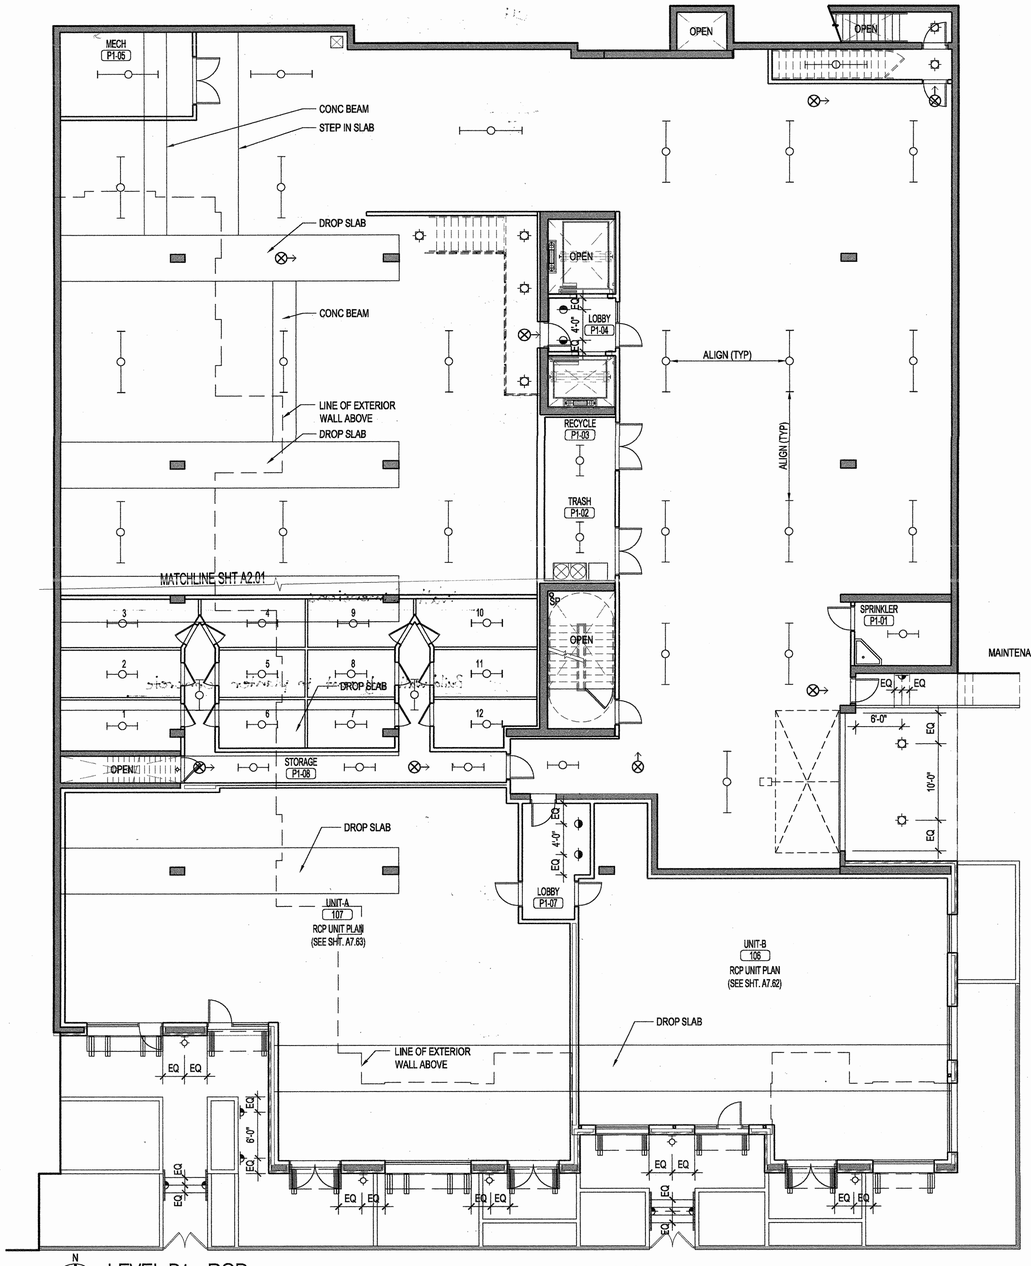

N

LEVEL P1 - RCP


1/8" = 1'-0"

PLAN WALL SYMBOLS

- C.I.P. CONC WALL
- MASONRY VENEER
- PRECAST PANELS (ASSEMBLY 1)
- PRECAST PANELS (ASSEMBLY 2)
- MTL FRAMING

ELECTRICAL LEGEND

- RECESSED LIGHT I.C. RATED WHERE REQ'D
- RECESSED WALL-WASHER I.C. RATED WHERE REQ'D
- WALL - MOUNT LIGHT
- STEP LIGHT
- CEILING - MOUNT LIGHT
- PENDANT LIGHT
- LOW VOLTAGE TRACK LIGHTING
- FLOOR MOUNTED UP-LIGHT
- LOW VOLTAGE MONOPOINT
- LINEAR FLUORESCENT
- LED STRIP LIGHT
- FLUORESCENT LIGHT
- EMERGENCY STAIR LIGHT
- EMERGENCY CORRIDOR LIGHT
- FAN / LIGHT
- BULB HEATER
- JUNCTION BOX
- EXHAUST FAN - V.T.O.S.
- SMOKE DETECTOR W/ BATTERY BACKUP
- SWITCH
- SWITCH- 3 WAY
- TIMER SWITCH
- DIMMER SWITCH
- 110v OUTLET
- 220v HEAVY DUTY OUTLET
- GFI OUTLET
- WATERPROOF GFI OUTLET
- SWITCHED OUTLET
- FLOOR MOUNTED SWITCH
- SWITCHED FLOOR MOUNTED SWITCH
- SPECIAL PURPOSE
- CABLE T.V.
- TELEPHONE
- DATA
- DOORBELL CHIME
- DOORBELL
- THERMOSTAT

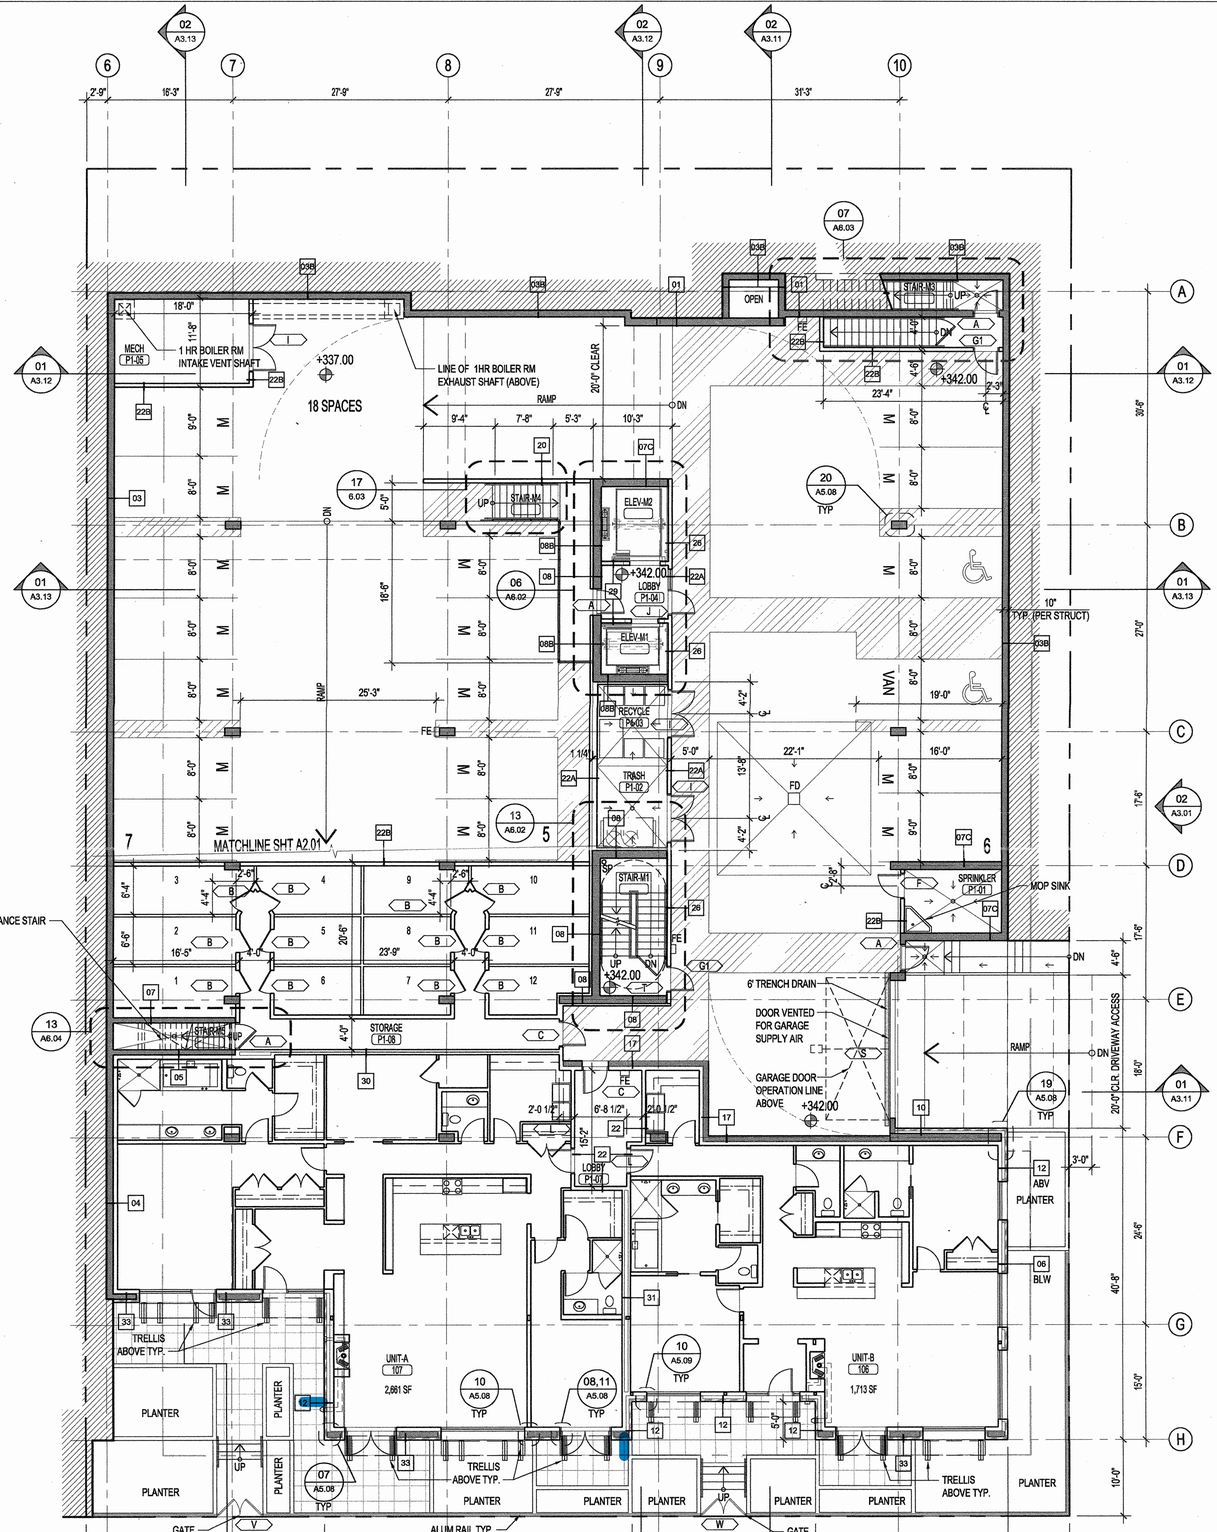

NOTE:
SEE SLAB & STEMWALL PLANS (SHT A2.12) FOR CONCRETE DIMENSIONS

N

LEVEL P1 - FLOOR PLAN (PARKING & RESIDENTIAL)

1/8" = 1'-0"

10' 0' 5' 20' 50'

MITHUN
Architects+Designers+Planners

Pier 56
1201 Alaskan Way
Suite 200
Seattle, WA 98101
TEL 206 623.3344
FAX 206 623.7005

202 West Highland

PROJECT:
200 W. Highland Drive

LOCATION:
202 W. Highland Drive
Seattle, WA 98119

PREPARED FOR:
Lorig Associates, LLC
2025 First Avenue, Suite 420
Seattle WA. 98121
T= 206.728.7660

NO.	DATE	REVISION

PROJECT DIRECTOR: JB
PROJECT MANAGER: EMD
PROJECT ARCHITECT: BB
PROJECT TEAM MEMBERS: ML, ML
CHECK:

ARCHITECT SEAL


3689 REGISTERED ARCHITECT
BRUCE L. WILLIAMS
STATE OF WASHINGTON

TITLE
LEVEL P1 - PLAN & RCP

PROJECT NO.
04470.00
DATE
04-02-07
PROJECT NETWORK PATH
S:_2005\0447000\Cadd\
A\SHEETS
SHEET NUMBER
A2.02

CONTRACT DOCUMENTS

© 2004 MITHUN, INC.

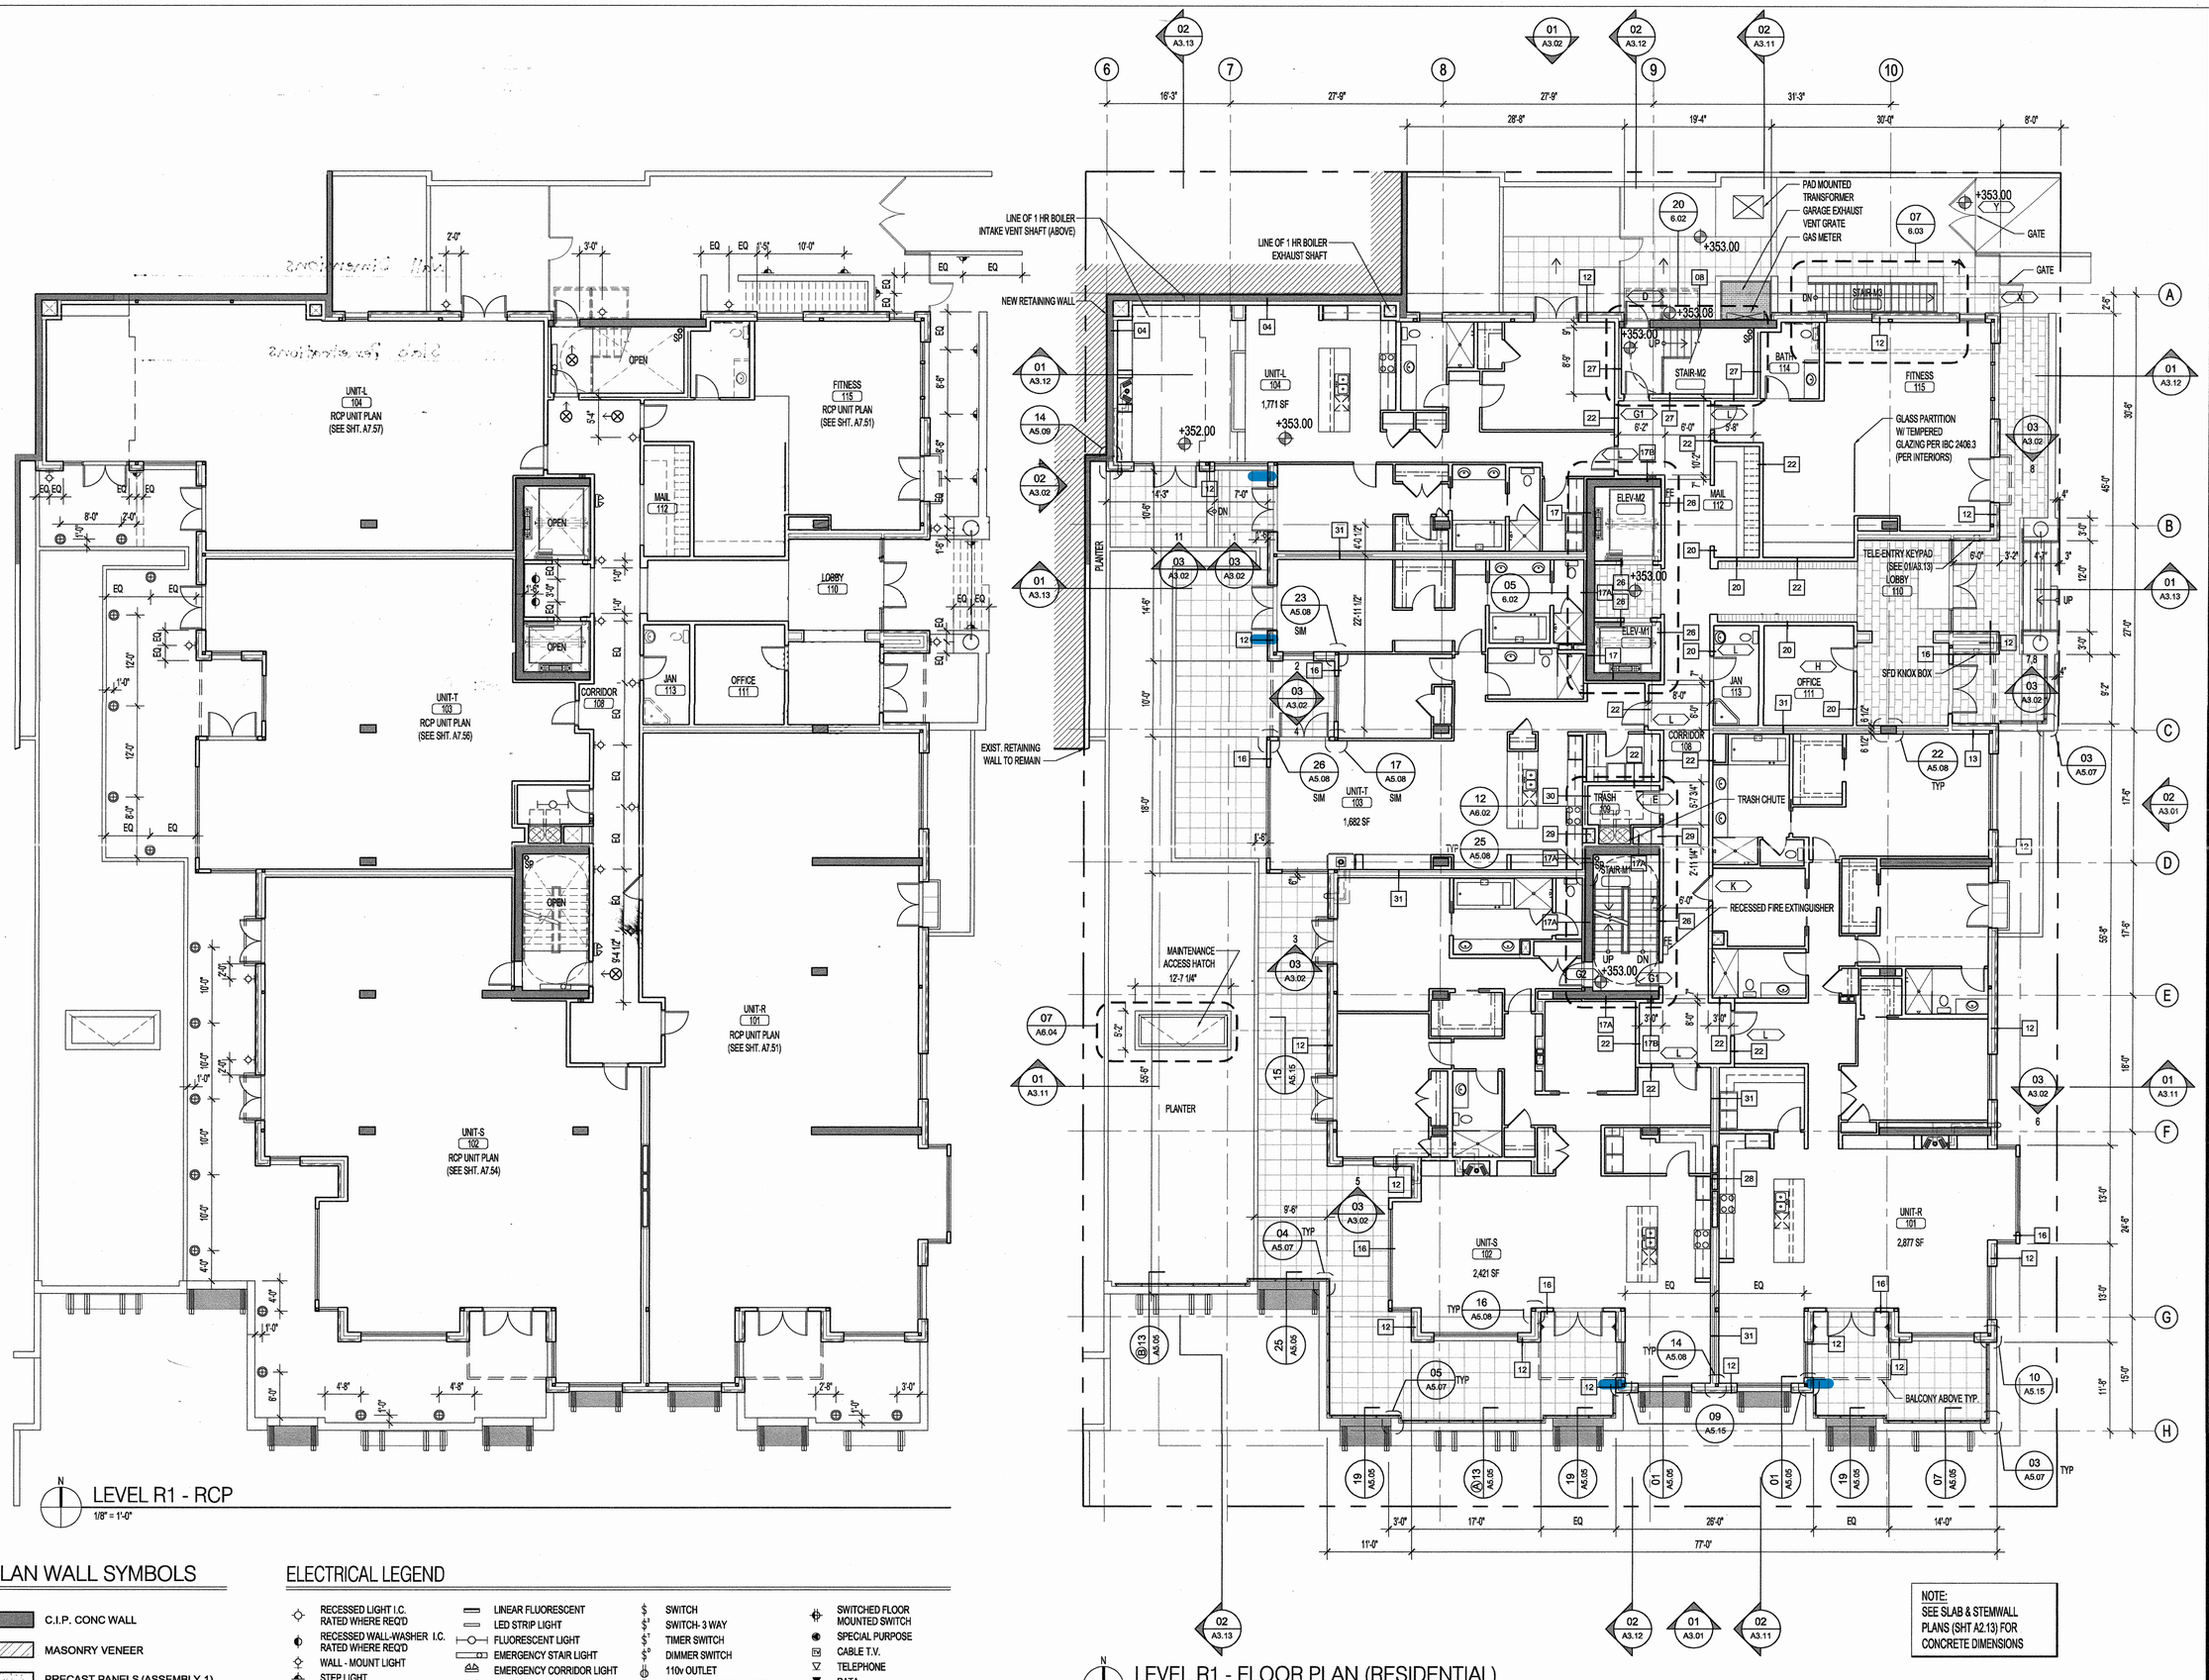

N

LEVEL R1 - RCP

1/8" = 1'-0"

N

LEVEL R1 - FLOOR PLAN (RESIDENTIAL)

1/8" = 1'-0"

NOTE:
SEE SLAB & STEMWALL PLANS (SHT A2.13) FOR CONCRETE DIMENSIONS

10' 0' 5' 20' 50'

PLAN WALL SYMBOLS

- C.I.P. CONC WALL
- MASONRY VENEER
- PRECAST PANELS (ASSEMBLY 1)
- PRECAST PANELS (ASSEMBLY 2)
- MTL FRAMING

ELECTRICAL LEGEND

- RECESSED LIGHT I.C. RATED WHERE REQ'D
- RECESSED WALL-WASHER I.C. RATED WHERE REQ'D
- WALL - MOUNT LIGHT
- STEP LIGHT
- CEILING - MOUNT LIGHT
- PENDANT LIGHT
- LOW VOLTAGE TRACK LIGHTING
- FLOOR MOUNTED UP-LIGHT
- LOW VOLTAGE MONOPOINT
- LINEAR FLUORESCENT
- LED STRIP LIGHT
- FLUORESCENT LIGHT
- EMERGENCY STAIR LIGHT
- EMERGENCY CORRIDOR LIGHT
- FAN / LIGHT
- BULB HEATER
- JUNCTION BOX
- EXHAUST FAN - V.T.O.S.
- SMOKE DETECTOR W/ BATTERY BACKUP
- SWITCH
- SWITCH- 3 WAY
- TIMER SWITCH
- DIMMER SWITCH
- 110v OUTLET
- 220v HEAVY DUTY OUTLET
- GFI OUTLET
- WATERPROOF GFI OUTLET
- SWITCHED OUTLET
- FLOOR MOUNTED SWITCH
- SWITCHED FLOOR MOUNTED SWITCH
- SPECIAL PURPOSE
- CABLE T.V.
- TELEPHONE
- DATA
- DOORBELL CHIME
- DOORBELL
- THERMOSTAT

MITHUN
Architects+Designers+Planners
Pier 56
1201 Alaskan Way
Suite 200
Seattle, WA 98101
TEL 206 623.3344
FAX 206 623.7005

200 West Highland

PROJECT:
200 W. Highland Drive

LOCATION:
202 W. Highland Drive
Seattle, WA 98119

PREPARED FOR:
Lorig Associates, LLC
2025 First Avenue, Suite 420
Seattle WA. 98121
T= 206.728.7660

RFI #

NO.	DATE	REVISION

PROJECT DIRECTOR: JB
PROJECT MANAGER: JRB
PROJECT ARCHITECT: EMD
PROJECT TEAM MEMBERS: BB
CHECK: ML, ML


ARCHITECT SEAL

3689 REGISTERED ARCHITECT
DAVID L. WILLIAMS
STATE OF WASHINGTON

TITLE
LEVEL R1 - PLAN & RCP

PROJECT NO.
04470.00
DATE
04-02-07
PROJECT NETWORK PATH
S:\ 2005\0447000\Cadd\
A\SHEETS
SHEET NUMBER
A2.03
CONTRACT DOCUMENTS


© 2004 MITHUN, INC.

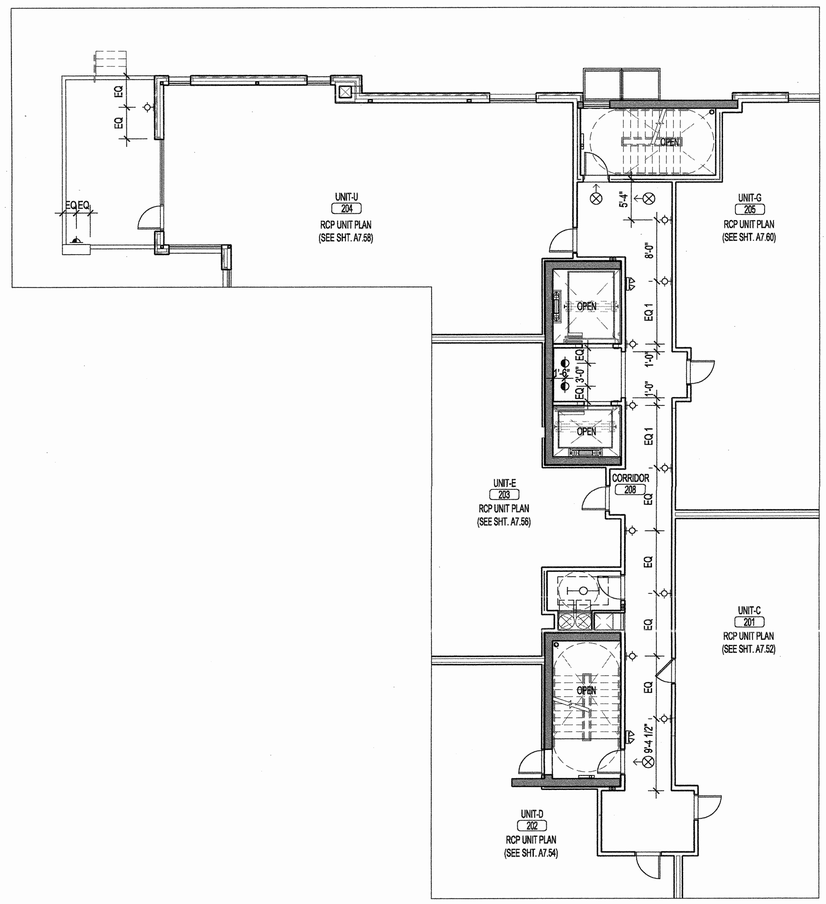

LEVEL R2 - RCP

1/8" = 1'-0"

NOTE:
UNIT ENTRY LIGHTS & BALCONY LIGHTS ARE LOCATED ON UNIT PLANS

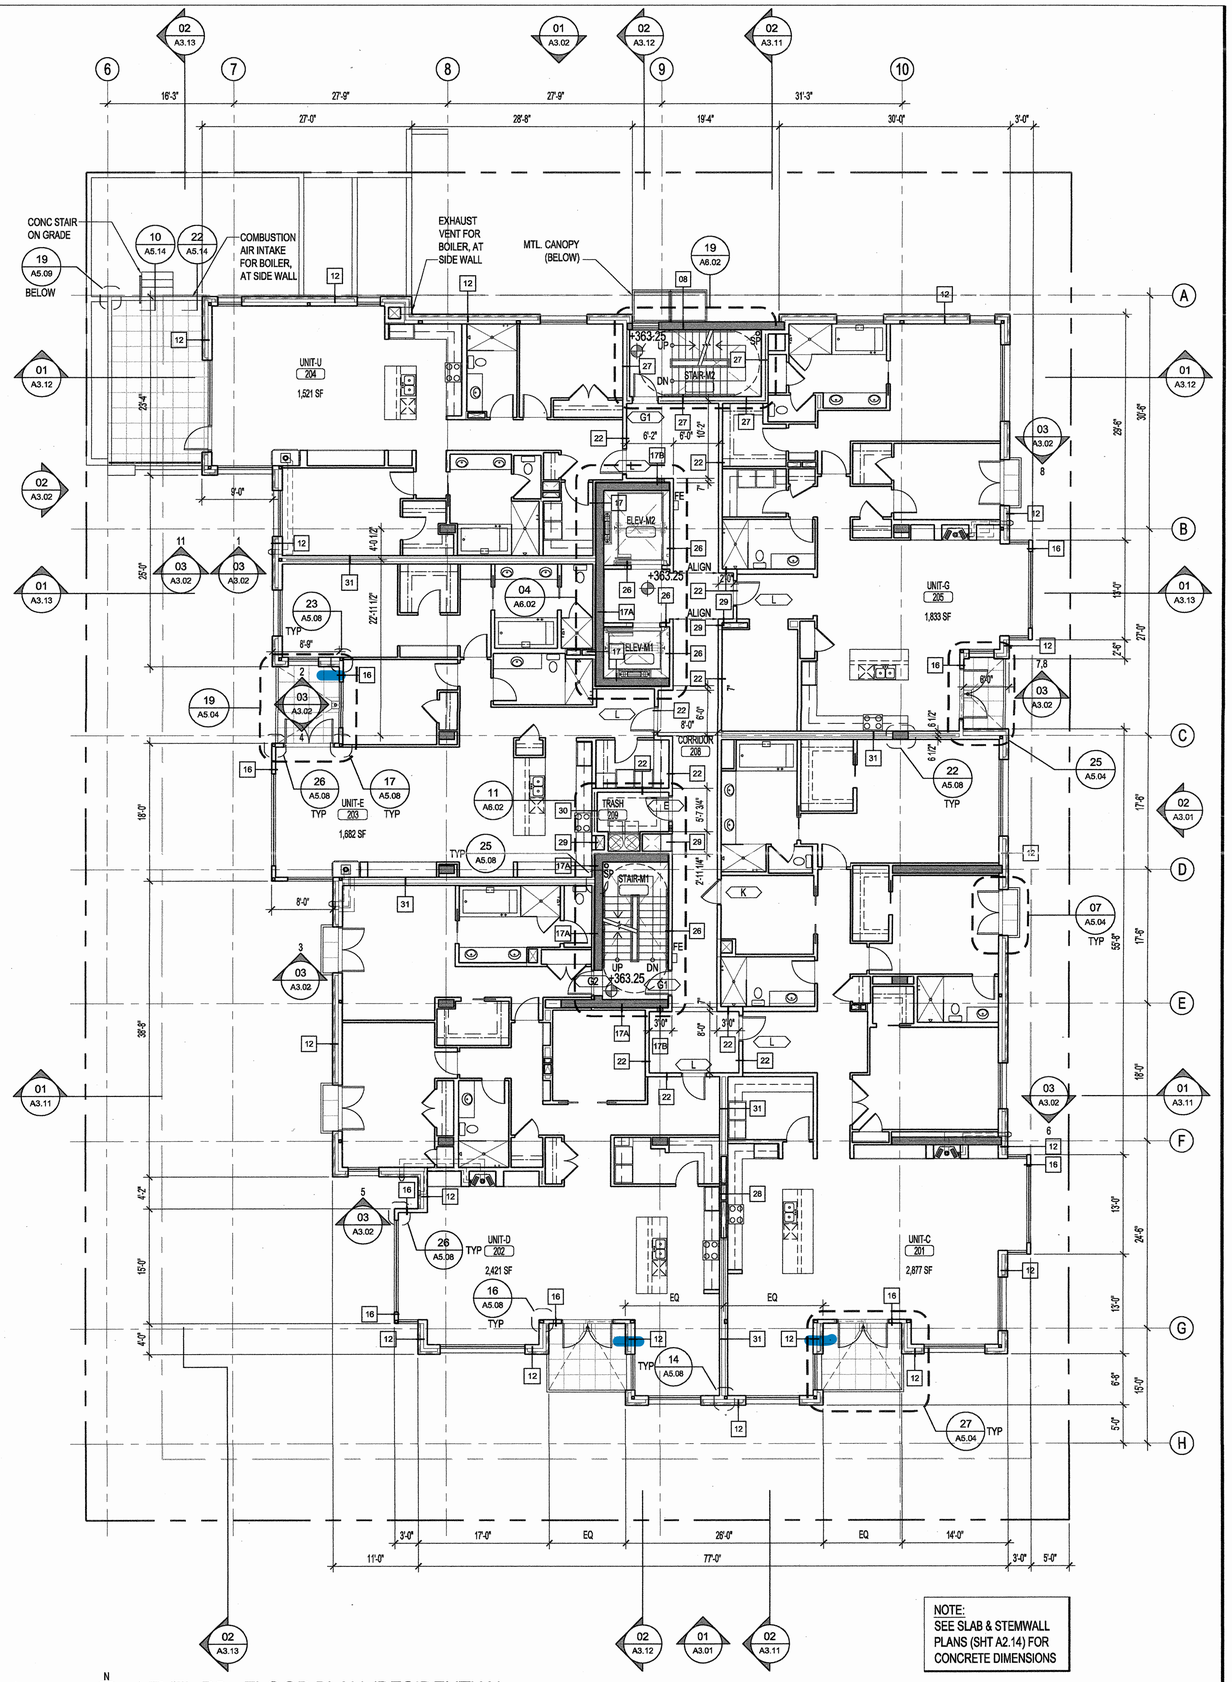

LEVEL R2 - FLOOR PLAN (RESIDENTIAL)

1/8" = 1'-0"

NOTE:
SEE SLAB & STEMWALL PLANS (SHT A2.14) FOR CONCRETE DIMENSIONS

PLAN WALL SYMBOLS

- C.I.P. CONC WALL
- MASONRY VENEER
- PRECAST PANELS (ASSEMBLY 1)
- PRECAST PANELS (ASSEMBLY 2)
- MTL FRAMING

ELECTRICAL LEGEND

- RECESSED LIGHT I.C. RATED WHERE REQ'D
- RECESSED WALL-WASHER I.C. RATED WHERE REQ'D
- WALL - MOUNT LIGHT
- STEP LIGHT
- CEILING - MOUNT LIGHT
- PENDANT LIGHT
- LOW VOLTAGE TRACK LIGHTING
- FLOOR MOUNTED UP-LIGHT
- LOW VOLTAGE MONOPOINT
- LINEAR FLUORESCENT
- LED STRIP LIGHT
- FLUORESCENT LIGHT
- EMERGENCY STAIR LIGHT
- EMERGENCY CORRIDOR LIGHT
- FAN / LIGHT
- BULB HEATER
- JUNCTION BOX
- EXHAUST FAN - V.T.O.S.
- SMOKE DETECTOR W/ BATTERY BACKUP
- SWITCH
- SWITCH- 3 WAY
- TIMER SWITCH
- DIMMER SWITCH
- 110v OUTLET
- 220v HEAVY DUTY OUTLET
- GFI OUTLET
- WATERPROOF GFI OUTLET
- SWITCHED OUTLET
- FLOOR MOUNTED SWITCH
- SWITCHED FLOOR MOUNTED SWITCH
- SPECIAL PURPOSE
- CABLE T.V.
- TELEPHONE
- DATA
- DOORBELL CHIME
- DOORBELL
- THERMOSTAT

MITHUN
Architects+Designers+Planners

Pier 56
1201 Alaskan Way
Suite 200
Seattle, WA 98101
TEL 206 623.3344
FAX 206 623.7005

202 highland dr

PROJECT:
200 W. Highland Drive

LOCATION:
202 W. Highland Drive
Seattle, WA 98119

PREPARED FOR:
Lorig Associates, LLC
2025 First Avenue, Suite 420
Seattle WA. 98121
T= 206.728.7660

200 West Highland

NO.	DATE	REVISION

PROJECT DIRECTOR: JB
PROJECT MANAGER: EMD
PROJECT ARCHITECT: BB
PROJECT TEAM MEMBERS: ML, ML
CHECK:
ARCHITECT SEAL:

J689 REGISTERED ARCHITECT BRUCE L. WILLIAMS STATE OF WASHINGTON

TITLE
LEVEL R2 - PLAN & RCP

PROJECT NO. 04470.00
DATE 04-02-07
PROJECT NETWORK PATH S:_2005\0447000\Cadd\
A\SHEETS
SHEET NUMBER **A2.04**

CONTRACT DOCUMENTS

© 2004 MITHUN, INC.

ASI #45 SECOND EGRESS DOOR UNIT 302

RFI #161 Wall Dimensions


RFI #211 Revised Ceiling Heights

RFI #301 Master Bath Ceiling Heights 305

RFI #325 Trash Room Door Width Change

ASI #96 Trash Room ADA Changes

RFI #344 Drop Header Heights, unit 305

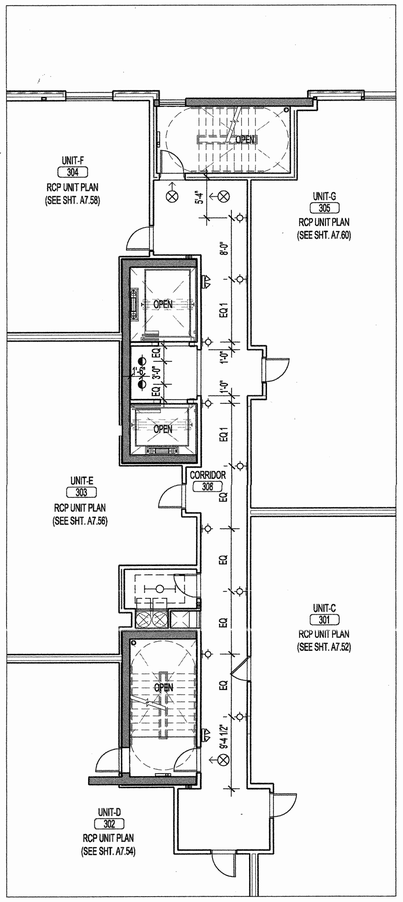


N

LEVEL R3 - RCP

1/8" = 1'-0"

NOTE:
UNIT ENTRY LIGHTS & BALCONY LIGHTS ARE LOCATED ON UNIT PLANS

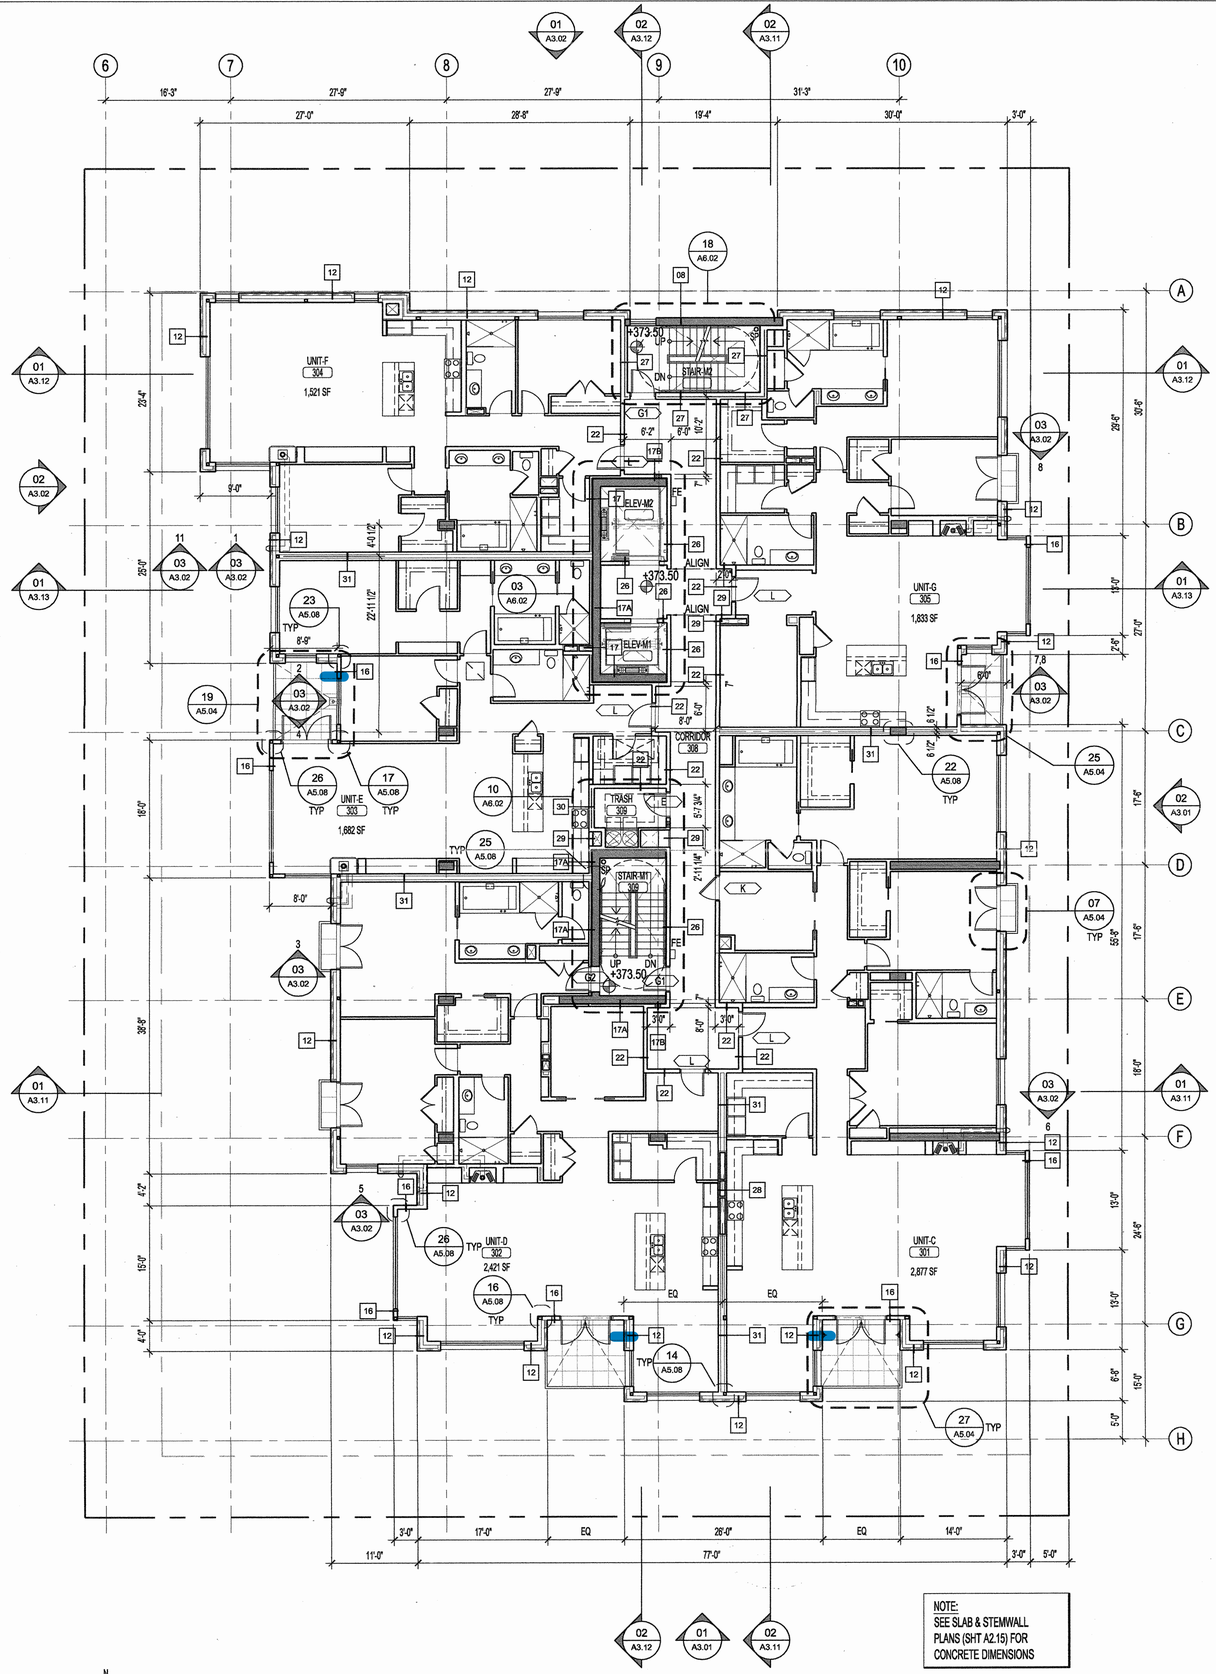

N

LEVEL R3 - FLOOR PLAN (RESIDENTIAL) / LOWRISE ROOF PLAN

1/8" = 1'-0"

NOTE:
SEE SLAB & STEMWALL PLANS (SHT A2.15) FOR CONCRETE DIMENSIONS

10' 0' 5' 20' 50'

PLAN WALL SYMBOLS

- C.I.P. CONC WALL
- MASONRY VENEER
- PRECAST PANELS (ASSEMBLY 1)
- PRECAST PANELS (ASSEMBLY 2)
- MTL FRAMING

ELECTRICAL LEGEND

- RECESSED LIGHT I.C. RATED WHERE REQ'D
- RECESSED WALL-WASHER I.C. RATED WHERE REQ'D
- WALL - MOUNT LIGHT
- STEP LIGHT
- CEILING - MOUNT LIGHT
- PENDANT LIGHT
- LOW VOLTAGE TRACK LIGHTING
- FLOOR MOUNTED UP-LIGHT
- LOW VOLTAGE MONOPOINT
- LINEAR FLUORESCENT
- LED STRIP LIGHT
- FLUORESCENT LIGHT
- EMERGENCY STAIR LIGHT
- EMERGENCY CORRIDOR LIGHT
- FAN / LIGHT
- BULB HEATER
- JUNCTION BOX
- EXHAUST FAN - V.T.O.S.
- SMOKE DETECTOR W/ BATTERY BACKUP
- SWITCH
- SWITCH- 3 WAY
- TIMER SWITCH
- DIMMER SWITCH
- 110v OUTLET
- 220v HEAVY DUTY OUTLET
- GFI OUTLET
- WATERPROOF GFI OUTLET
- SWITCHED OUTLET
- FLOOR MOUNTED SWITCH
- SWITCHED FLOOR MOUNTED SWITCH
- SPECIAL PURPOSE
- CABLE T.V.
- TELEPHONE
- DATA
- DOORBELL CHIME
- DOORBELL
- THERMOSTAT

MITHUN
Architects+Designers+Planners
Pier 56
1201 Alaskan Way
Suite 200
Seattle, WA 98101
TEL 206 623.3344
FAX 206 623.7005

202 highland dr

PROJECT:
200 W. Highland Drive
LOCATION:
202 W. Highland Drive
Seattle, WA 98119

PREPARED FOR:
Lorig Associates, LLC
2025 First Avenue, Suite 420
Seattle WA. 98121
T= 206.728.7660

200 West Highland

NO.	DATE	REVISION

PROJECT DIRECTOR
JB
PROJECT MANAGER
EMD
PROJECT ARCHITECT
BB
PROJECT TEAM MEMBERS
ML, ML
CHECK

ARCHITECT SEAL

3689 REGISTERED ARCHITECT
CHARLES L. WILLIAMS
STATE OF WASHINGTON

TITLE
LEVEL R3 - PLAN & RCP

PROJECT NO.
04470.00
DATE
04-02-07
PROJECT NETWORK PATH
S:\ 2005\0447000\Cadd\
A\SHEETS
SHEET NUMBER
A2.05

CONTRACT DOCUMENTS

© 2004 MITHUN, INC.

ASI #45 SECOND EGRESS DOOR UNIT 402

RFI #161 Wall Dimensions

RFI #269 Air Intakes For Units 401, 402

RFI #211 Revised Ceiling Heights

RFI #301 Master Bath Ceiling Heights 405


RFI #306 Ceiling Dropped 5" @ Structural Soffit

RFI #316 Follow up to RFI # 306

RFI #325 Trash Room Width Change to Door

ASI #96 Trash Room ADA Changes

RFI #349 Drop Header Heights, unit 405

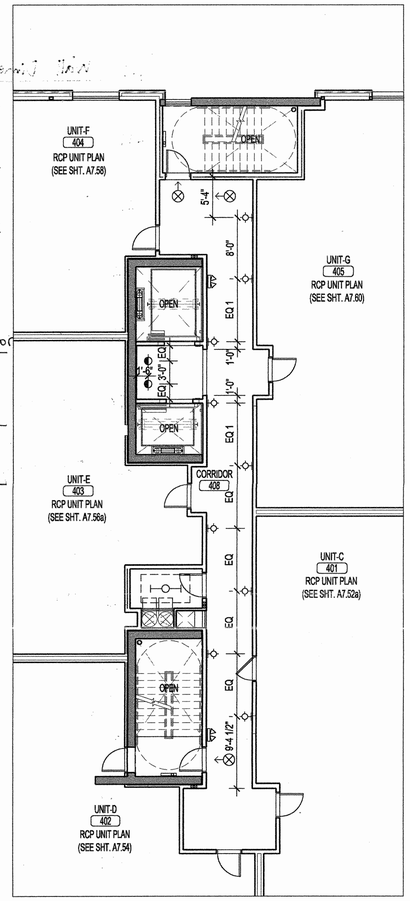


N

LEVEL R4 - RCP

1/8" = 1'-0"

NOTE:
UNIT ENTRY LIGHTS & BALCONY LIGHTS ARE LOCATED ON UNIT PLANS

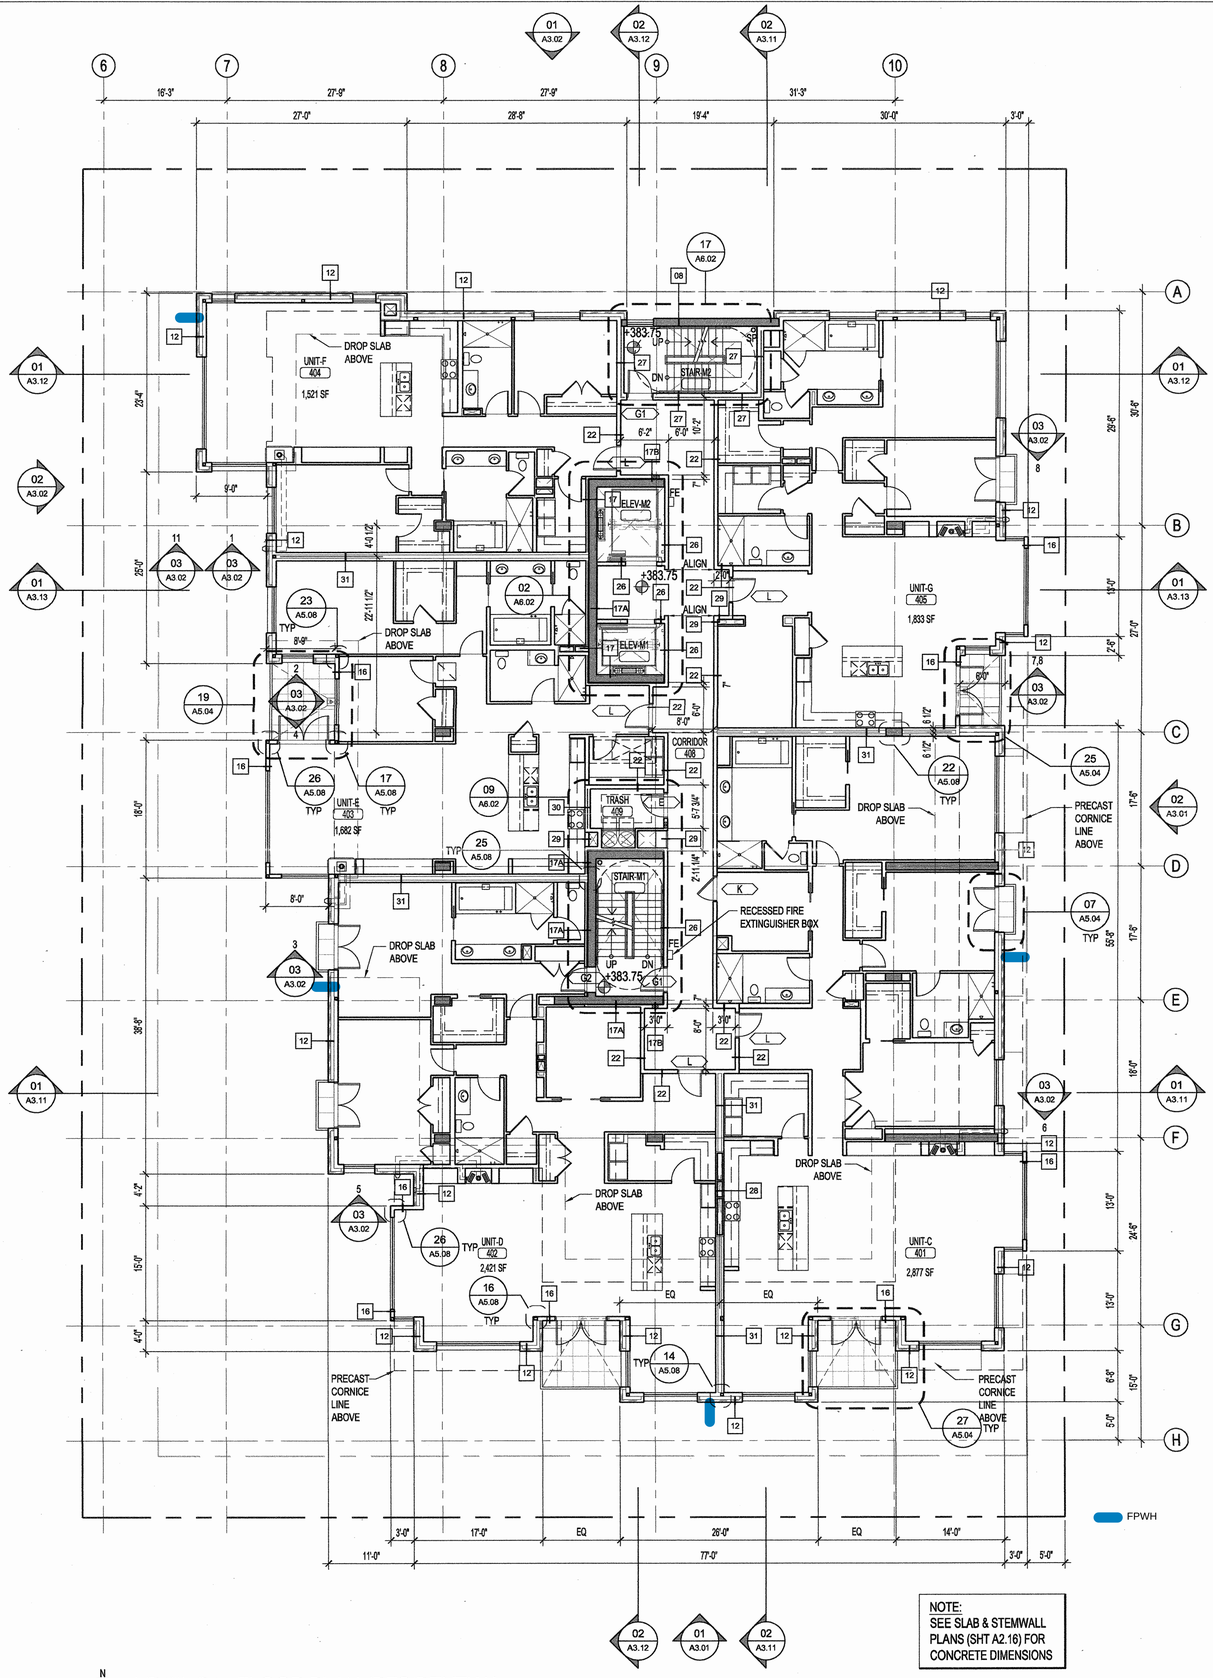

N

LEVEL R4 - FLOOR PLAN (RESIDENTIAL)

1/8" = 1'-0"

0' 5' 10' 20' 50'

PLAN WALL SYMBOLS

- C.I.P. CONC WALL
- MASONRY VENEER
- PRECAST PANELS (ASSEMBLY 1)
- PRECAST PANELS (ASSEMBLY 2)
- MTL FRAMING

ELECTRICAL LEGEND

- RECESSED LIGHT I.C. RATED WHERE REQ'D
- RECESSED WALL-WASHER I.C. RATED WHERE REQ'D
- WALL - MOUNT LIGHT
- STEP LIGHT
- CEILING - MOUNT LIGHT
- PENDANT LIGHT
- LOW VOLTAGE TRACK LIGHTING
- FLOOR MOUNTED UP-LIGHT
- LOW VOLTAGE MONOPOINT
- LINEAR FLUORESCENT
- LED STRIP LIGHT
- FLUORESCENT LIGHT
- EMERGENCY STAIR LIGHT
- EMERGENCY CORRIDOR LIGHT
- FAN / LIGHT
- BULB HEATER
- JUNCTION BOX
- EXHAUST FAN - V.T.O.S.
- SMOKE DETECTOR W/ BATTERY BACKUP
- SWITCH
- SWITCH- 3 WAY
- TIMER SWITCH
- DIMMER SWITCH
- 110v OUTLET
- 220v HEAVY DUTY OUTLET
- GFI OUTLET
- WATERPROOF GFI OUTLET
- SWITCHED OUTLET
- FLOOR MOUNTED SWITCH
- SWITCHED FLOOR MOUNTED SWITCH
- SPECIAL PURPOSE
- CABLE T.V.
- TELEPHONE
- DATA
- DOORBELL CHIME
- DOORBELL
- THERMOSTAT

MITHUN
Architects+Designers+Planners
Pier 56
1201 Alaskan Way
Suite 200
Seattle, WA 98101
TEL 206 623.3344
FAX 206 623.7005

PROJECT:
200 W. Highland Drive

LOCATION:
202 W. Highland Drive
Seattle, WA 98119

PREPARED FOR:
Lorig Associates, LLC
2025 First Avenue, Suite 420
Seattle WA, 98121
T= 206.728.7660

NO. DATE REVISION

PROJECT DIRECTOR: JB
PROJECT MANAGER: EMD
PROJECT ARCHITECT: BB
PROJECT TEAM MEMBERS: ML, ML
CHECK:


ARCHITECT SEAL:
3689 REGISTERED ARCHITECT BRUCE L. WILLIAMS STATE OF WASHINGTON

TITLE
LEVEL R4 - PLAN & RCP

PROJECT NO. 04470.00
DATE 04-02-07
PROJECT NETWORK PATH S:\ 2005\0447000\Cadd\
A\SHEETS
SHEET NUMBER A2.06

CONTRACT DOCUMENTS

© 2004 MITHUN, INC.

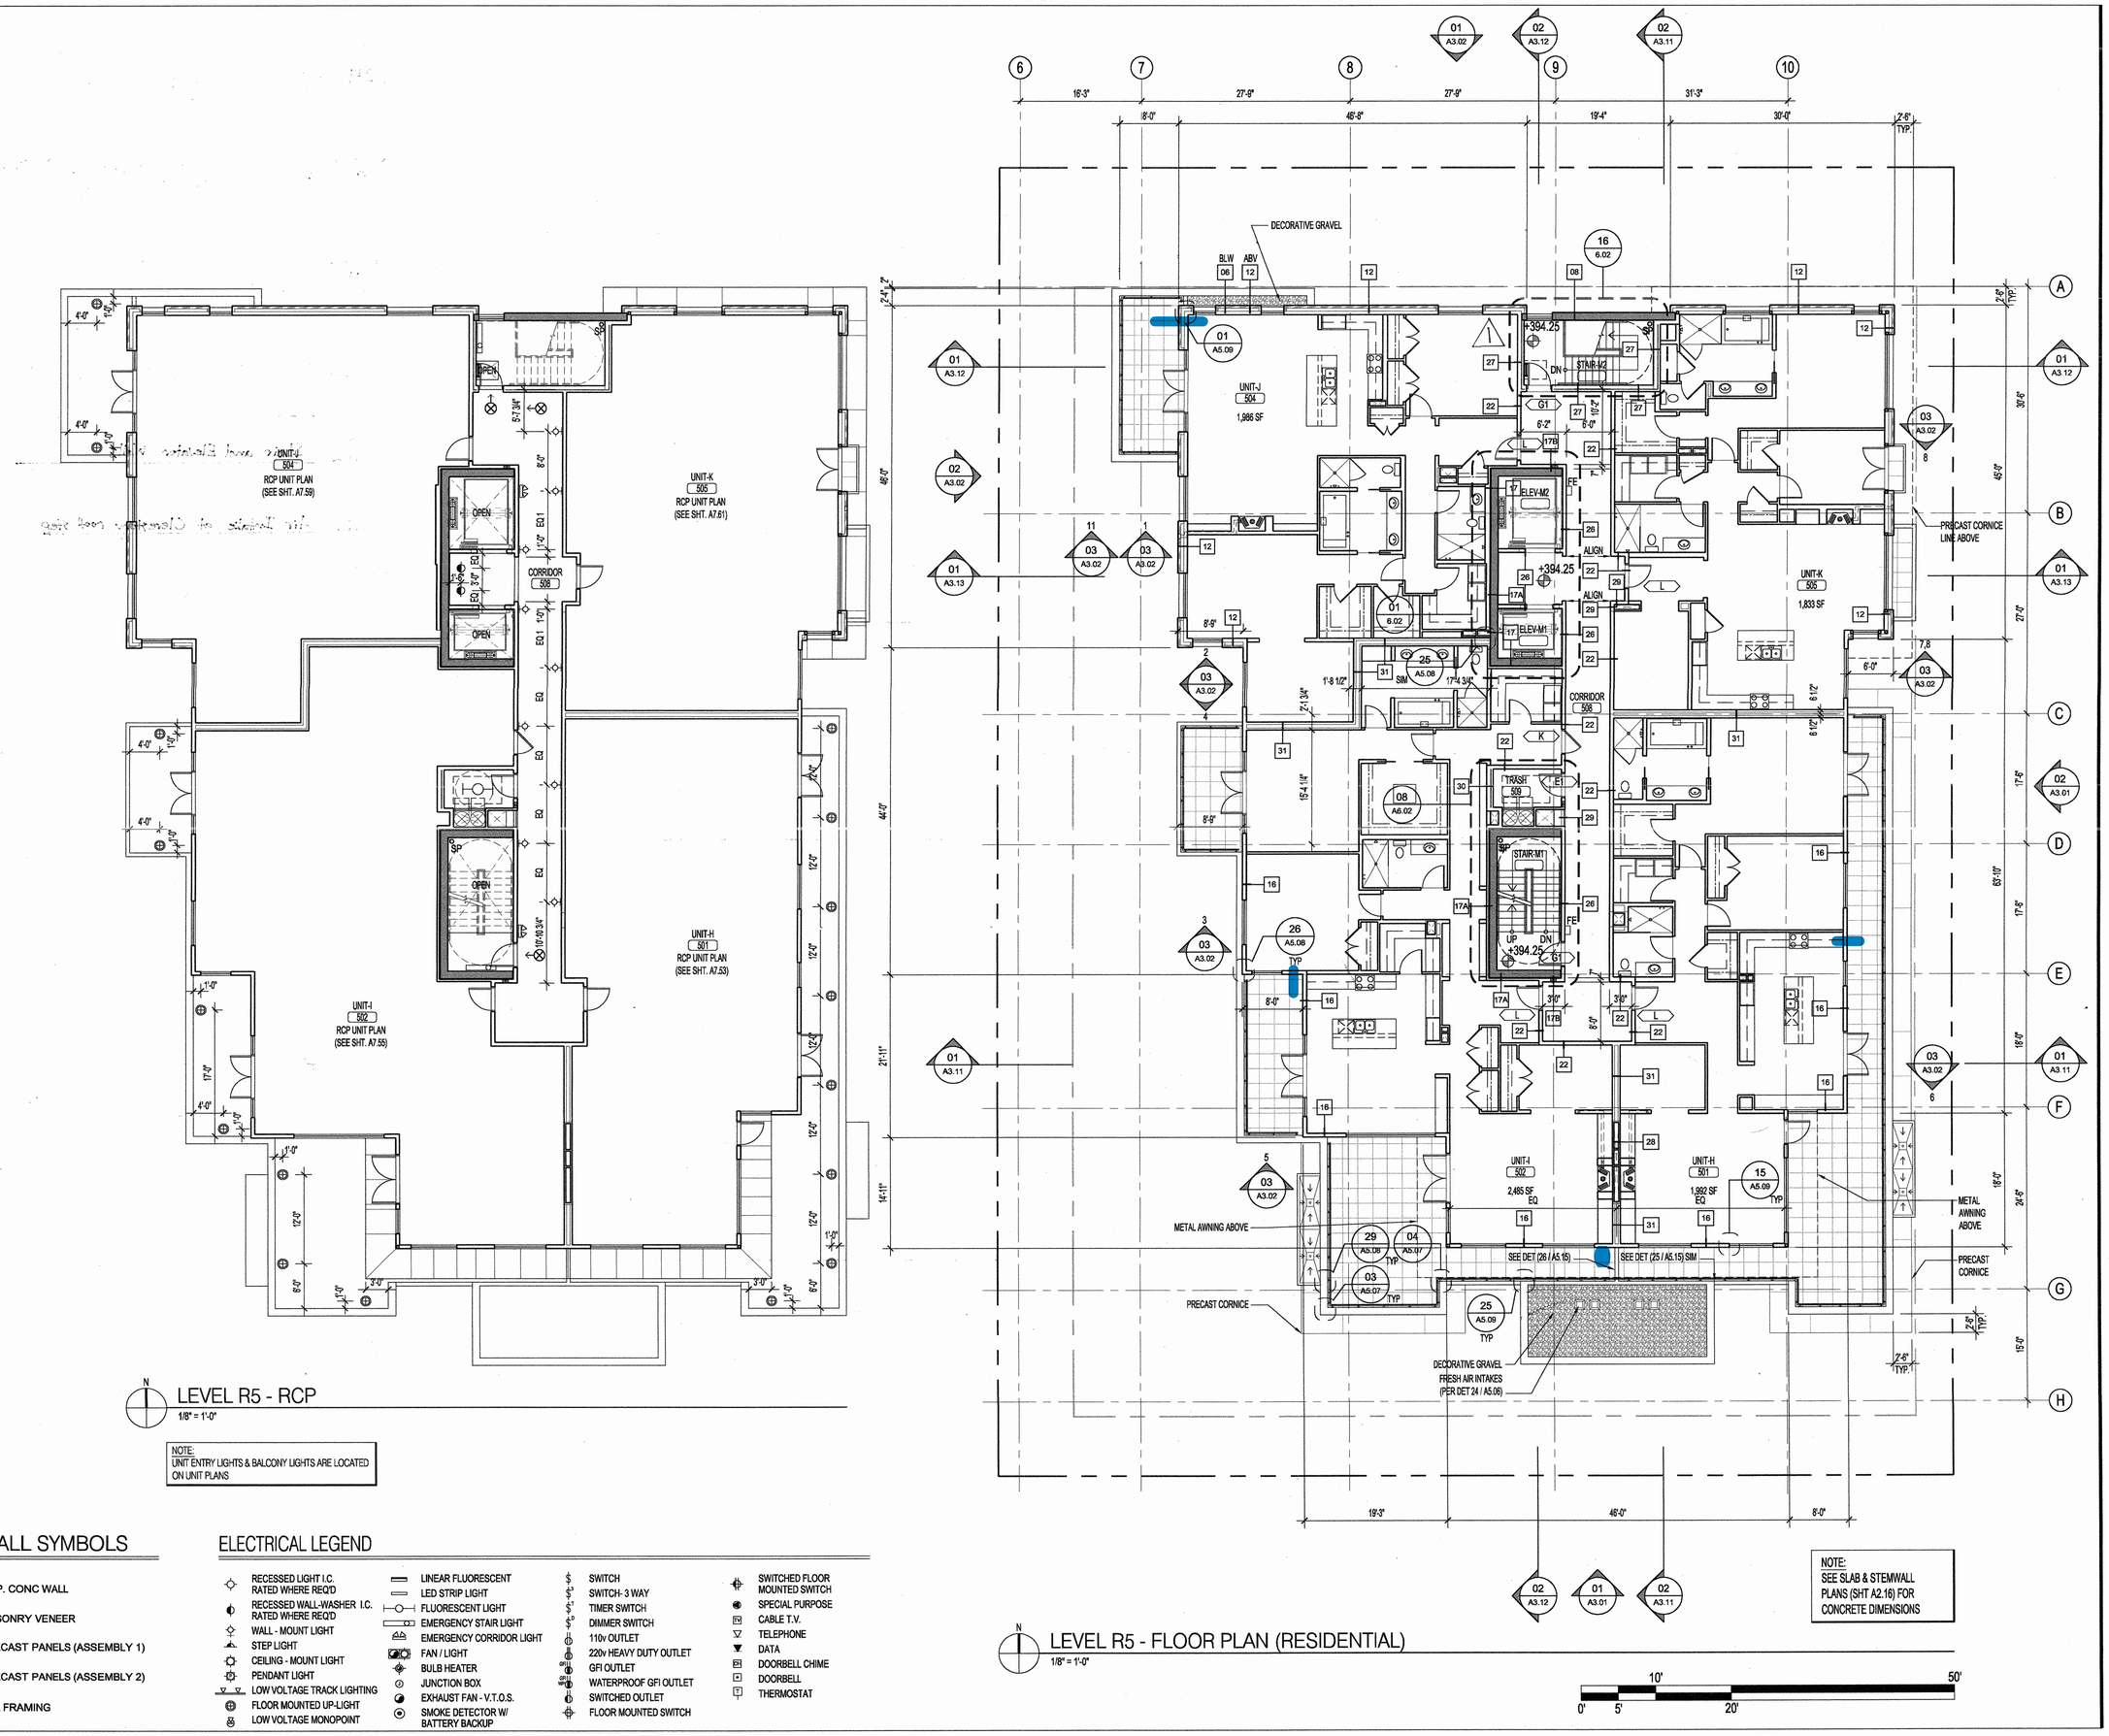

N

LEVEL R5 - RCP

1/8" = 1'-0"

NOTE:
UNIT ENTRY LIGHTS & BALCONY LIGHTS ARE LOCATED ON UNIT PLANS

N

LEVEL R5 - FLOOR PLAN (RESIDENTIAL)

1/8" = 1'-0"

NOTE:
SEE SLAB & STEMWALL PLANS (SHT A2.16) FOR CONCRETE DIMENSIONS

10' 5' 0' 20' 50'

PLAN WALL SYMBOLS

- C.I.P. CONC WALL
- MASONRY VENEER
- PRECAST PANELS (ASSEMBLY 1)
- PRECAST PANELS (ASSEMBLY 2)
- MTL FRAMING

ELECTRICAL LEGEND

- RECESSED LIGHT I.C. RATED WHERE REQ'D
- RECESSED WALL-WASHER I.C. RATED WHERE REQ'D
- WALL - MOUNT LIGHT
- STEP LIGHT
- CEILING - MOUNT LIGHT
- PENDANT LIGHT
- LOW VOLTAGE TRACK LIGHTING
- FLOOR MOUNTED UP-LIGHT
- LOW VOLTAGE MONOPOINT
- LINEAR FLUORESCENT
- LED STRIP LIGHT
- FLUORESCENT LIGHT
- EMERGENCY STAIR LIGHT
- EMERGENCY CORRIDOR LIGHT
- FAN / LIGHT
- BULB HEATER
- JUNCTION BOX
- EXHAUST FAN - V.T.O.S.
- SMOKE DETECTOR W/ BATTERY BACKUP
- SWITCH
- SWITCH- 3 WAY
- TIMER SWITCH
- DIMMER SWITCH
- 110v OUTLET
- 220v HEAVY DUTY OUTLET
- GFI OUTLET
- WATERPROOF GFI OUTLET
- SWITCHED OUTLET
- FLOOR MOUNTED SWITCH
- SWITCHED FLOOR MOUNTED SWITCH
- SPECIAL PURPOSE
- CABLE T.V.
- TELEPHONE
- DATA
- DOORBELL CHIME
- DOORBELL
- THERMOSTAT

MITHUN
Architects+Designers+Planners

Pier 56
1201 Alaskan Way
Suite 200
Seattle, WA 98101
TEL 206 623.3344
FAX 206 623.7005

PROJECT:
200 W. Highland Drive

LOCATION:
202 W. Highland Drive
Seattle, WA 98119

PREPARED FOR:
Lorig Associates, LLC
2025 First Avenue, Suite 420
Seattle WA. 98121
T= 206.728.7660

NO.	DATE	REVISION

PROJECT DIRECTOR
JB
PROJECT MANAGER
EMD
PROJECT ARCHITECT
BB
PROJECT TEAM MEMBERS
ML, ML
CHECK

ARCHITECT SEAL


3689 REGISTERED ARCHITECT
BRUCE L. WILLIAMS
STATE OF WASHINGTON

TITLE
LEVEL R5 - PLAN & RCP


PROJECT NO.
04470.00
DATE
04-02-07
PROJECT NETWORK PATH
S:_2005\0447000\Cadd\
A\SHEETS
SHEET NUMBER
A2.07

CONTRACT DOCUMENTS

© 2004 MITHUN, INC.

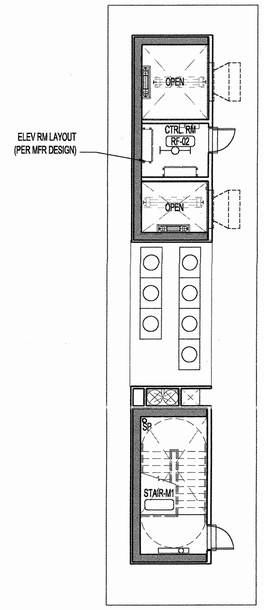


N
STAIR & ELEVATOR TOWER - RCP
1/8" = 1'-0"

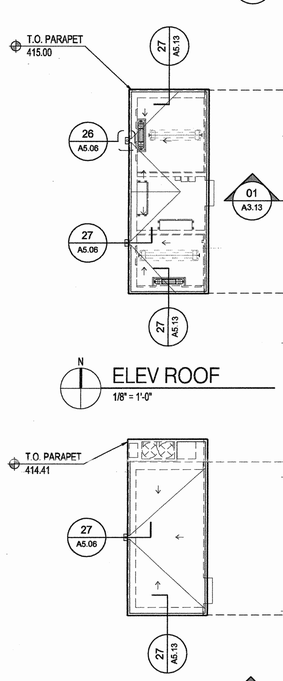

N
ELEV ROOF
1/8" = 1'-0"

N
STAIR ROOF
1/8" = 1'-0"

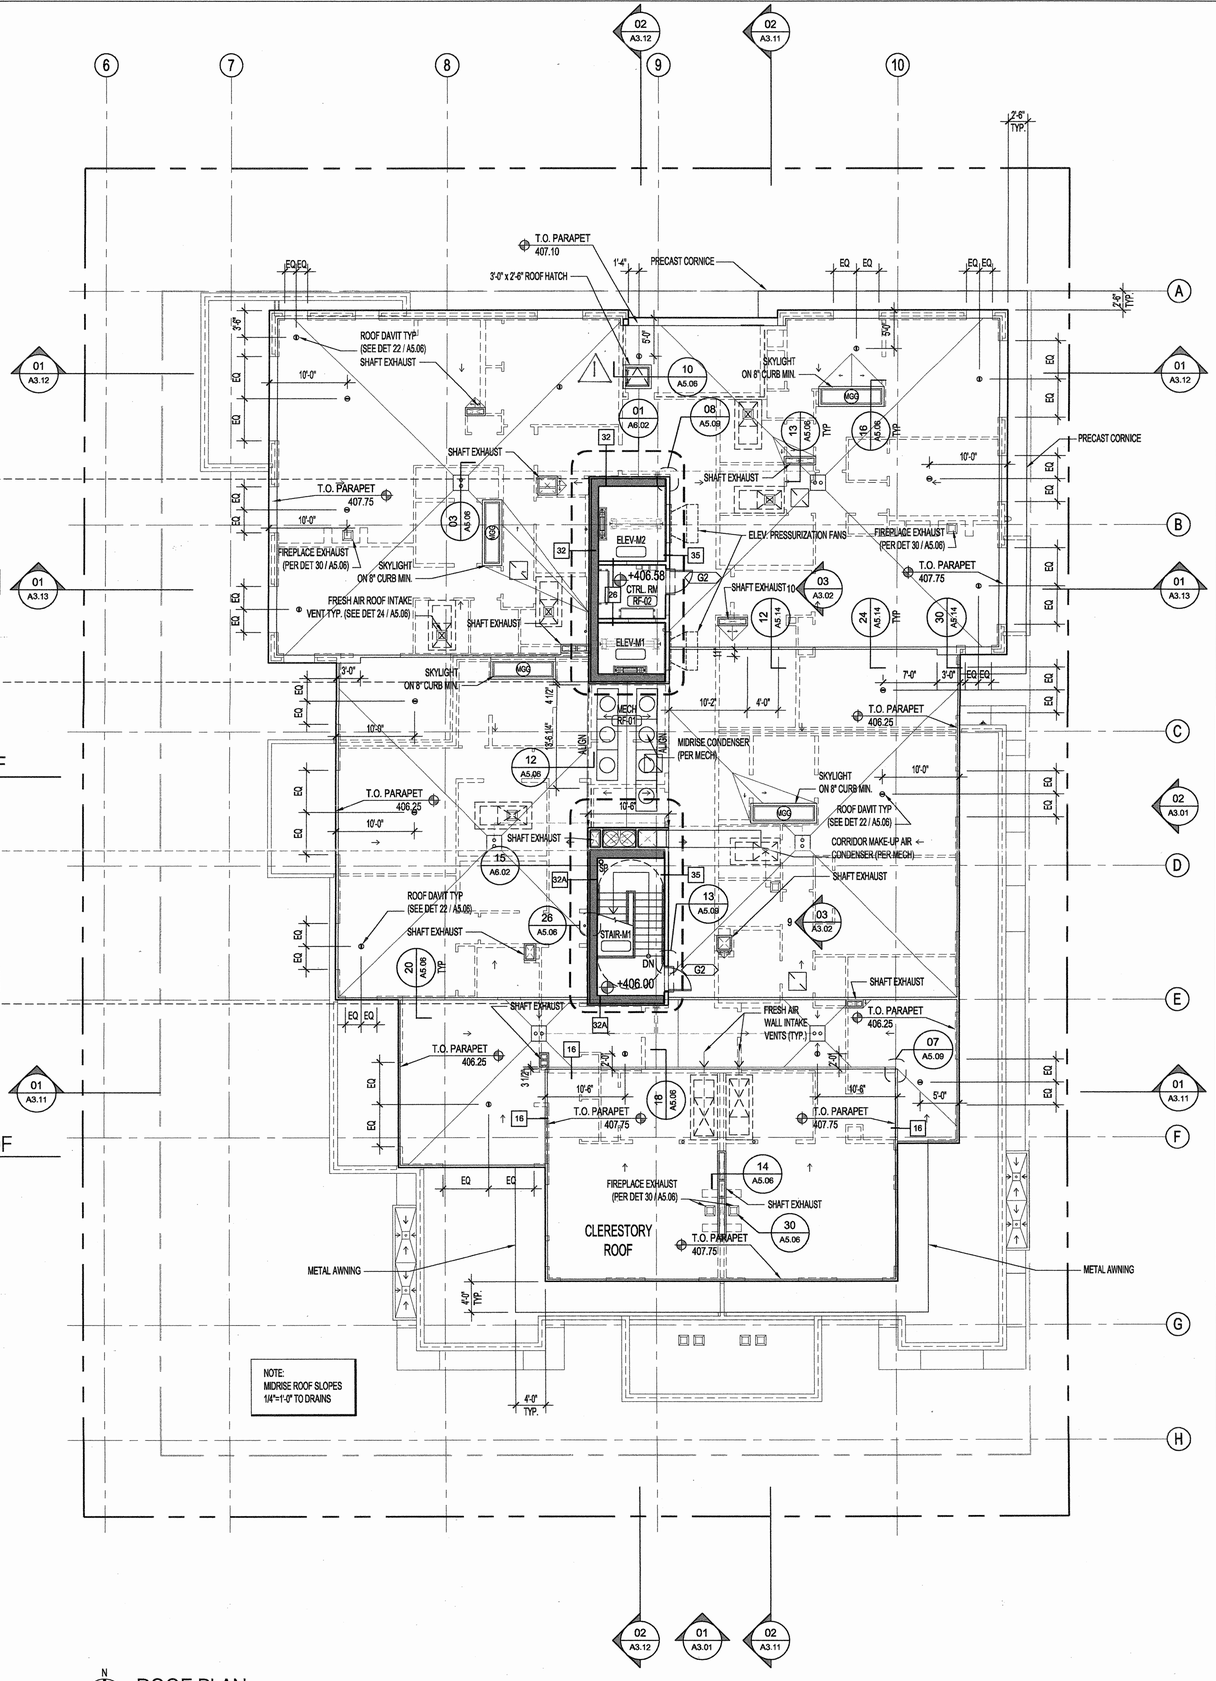

N
ROOF PLAN
1/8" = 1'-0"

Distance
50'-2 3/4"
0' 5' 10' 20' 50'

PLAN WALL SYMBOLS

- C.I.P. CONC WALL
- MASONRY VENEER
- PRECAST PANELS (ASSEMBLY 1)
- PRECAST PANELS (ASSEMBLY 2)
- MTL FRAMING

ELECTRICAL LEGEND

- RECESSED LIGHT I.C. RATED WHERE REQ'D
- RECESSED WALL-WASHER I.C. RATED WHERE REQ'D
- WALL - MOUNT LIGHT
- STEP LIGHT
- CEILING - MOUNT LIGHT
- PENDANT LIGHT
- LOW VOLTAGE TRACK LIGHTING
- FLOOR MOUNTED UP-LIGHT
- LOW VOLTAGE MONOPOINT
- LINEAR FLUORESCENT
- LED STRIP LIGHT
- FLUORESCENT LIGHT
- EMERGENCY STAIR LIGHT
- EMERGENCY CORRIDOR LIGHT
- FAN / LIGHT
- BULB HEATER
- JUNCTION BOX
- EXHAUST FAN - V.T.O.S.
- SMOKE DETECTOR W/ BATTERY BACKUP
- SWITCH
- SWITCH- 3 WAY
- TIMER SWITCH
- DIMMER SWITCH
- 110v OUTLET
- 220v HEAVY DUTY OUTLET
- GFI OUTLET
- WATERPROOF GFI OUTLET
- SWITCHED OUTLET
- FLOOR MOUNTED SWITCH
- SWITCHED FLOOR MOUNTED SWITCH
- SPECIAL PURPOSE
- CABLE T.V.
- TELEPHONE
- DATA
- DOORBELL CHIME
- DOORBELL
- THERMOSTAT

MITHUN
Architects+Designers+Planners

Pier 56
1201 Alaskan Way
Suite 200
Seattle, WA 98101
TEL 206 623.3344
FAX 206 623.7005

PROJECT:
200 W. Highland Drive

LOCATION:
202 W. Highland Drive
Seattle, WA 98119

PREPARED FOR:
Lorig Associates, LLC
2025 First Avenue, Suite 420
Seattle WA. 98121
T= 206.728.7660

NO.	DATE	REVISION

PROJECT DIRECTOR: JB
PROJECT MANAGER: EMD
PROJECT ARCHITECT: BB
PROJECT TEAM MEMBERS: ML, ML
CHECK:

ARCHITECT SEAL

3689 REGISTERED ARCHITECT
BRUCE L. WILLIAMS
STATE OF WASHINGTON

TITLE
ROOF PLAN
& RCP

PROJECT NO. 04470.00
DATE 04-02-07
PROJECT NETWORK PATH S:_2005\0447000\Cadd\
A\SHEETS
SHEET NUMBER **A2.08**

CONTRACT DOCUMENTS

© 2004 MITHUN, INC.