
Primary bathroom: supply connections


Nine explicit fixture ports connect the two lavatories, tub, shower and toilet. Rounded elbows, branch tees, five shutoffs and two mixing bodies are representative hardware. Heights and local wall-side offsets remain assumed.

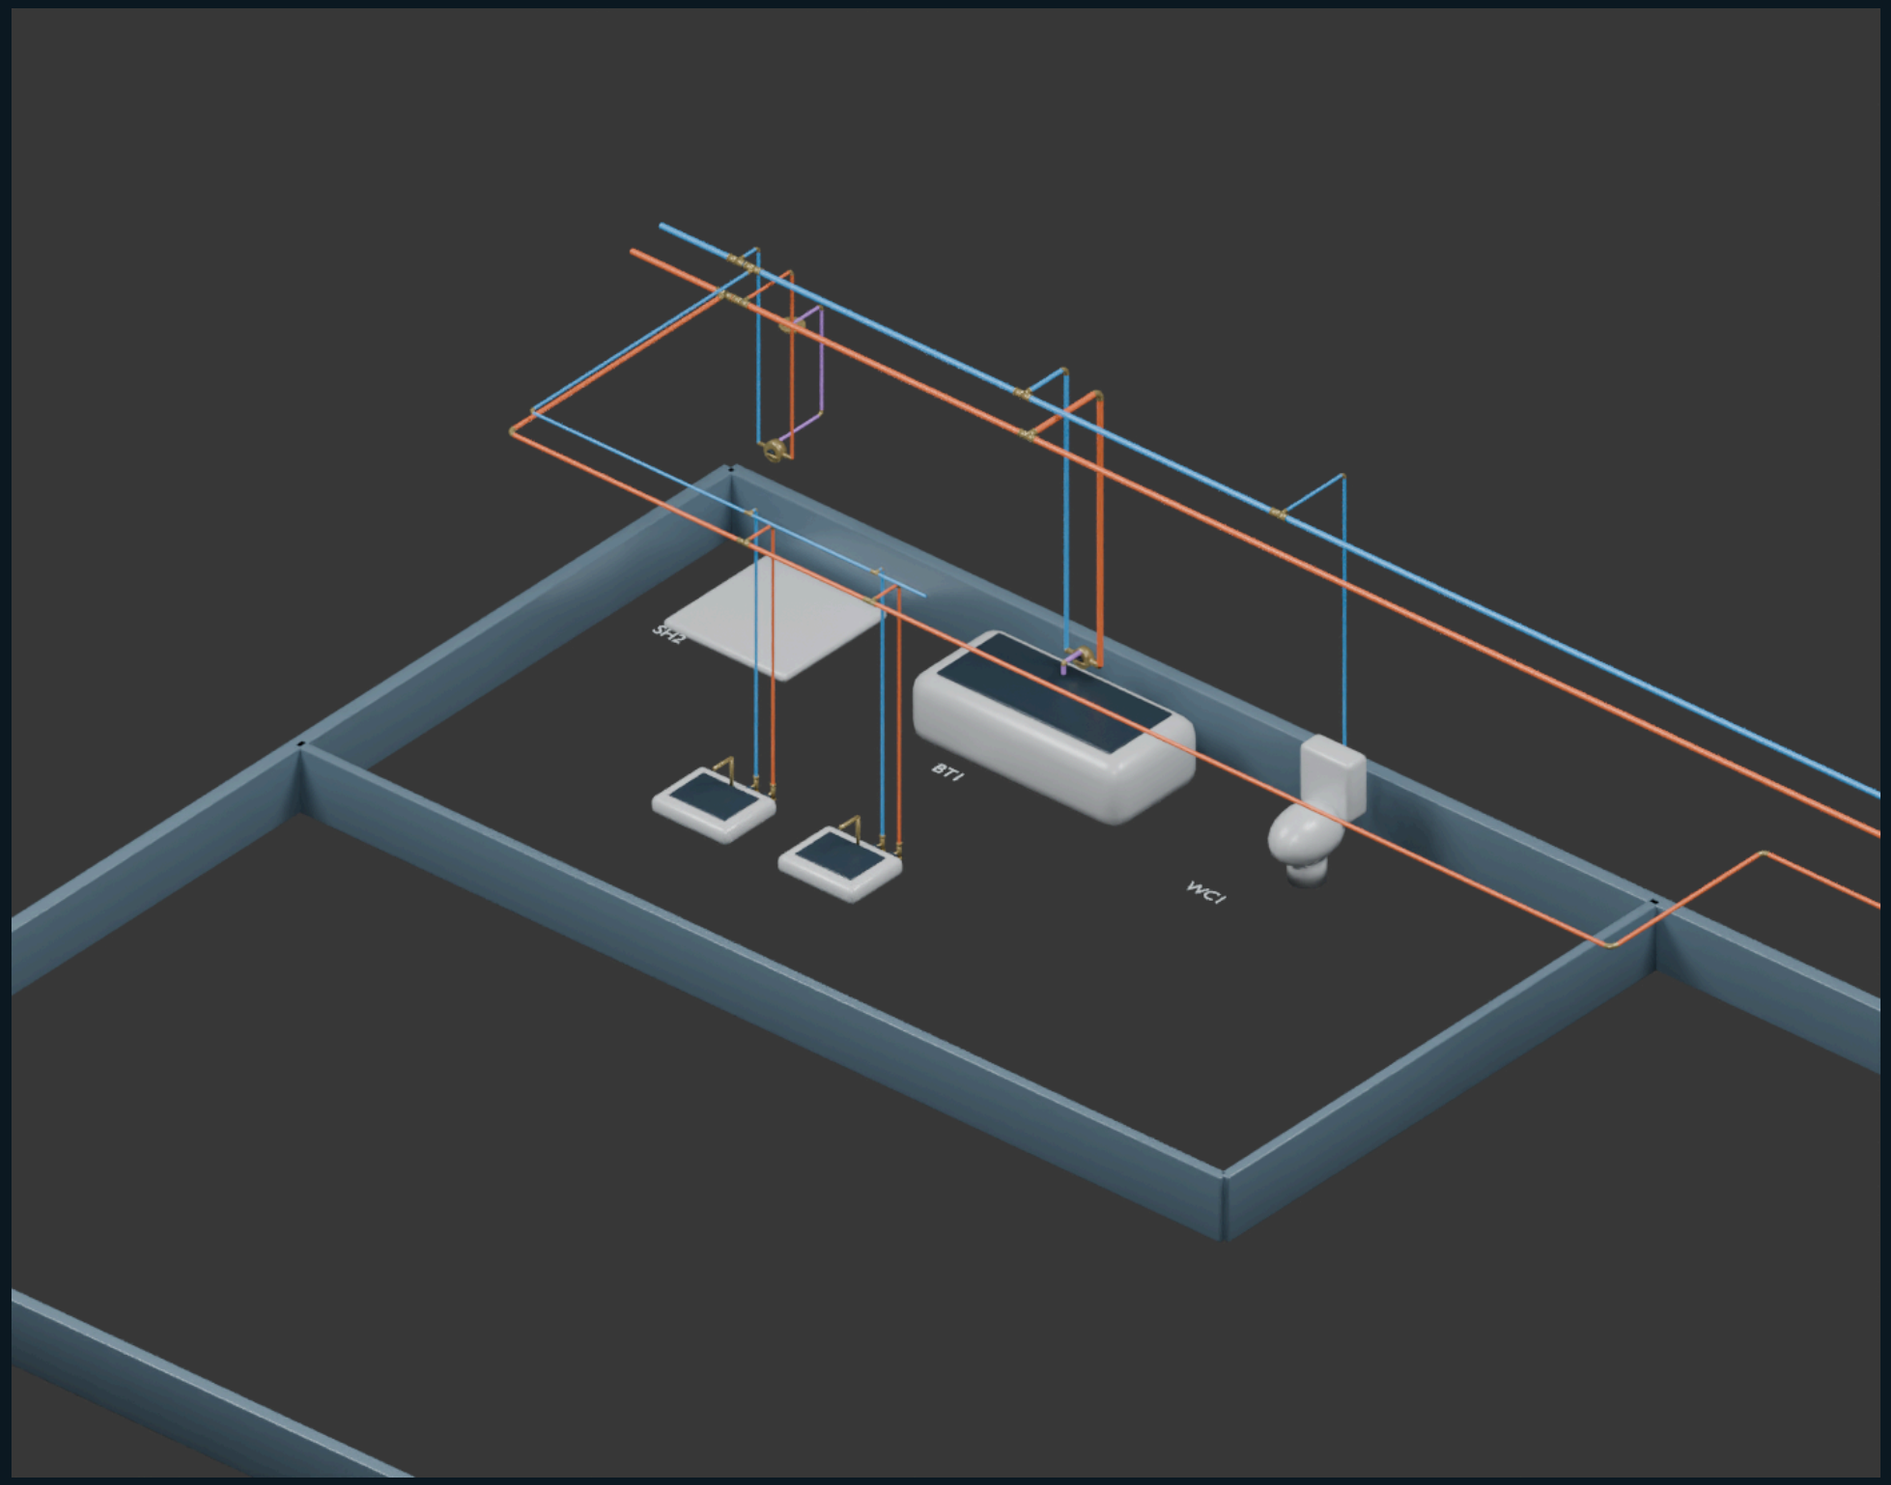

MODEL STUDY | Unit XY provisionally calibrated; pipe heights and envelopes assumed. Not an as-built.

Fixture connections: behind the basins

Vertical supplies run behind the fixture envelopes. Short flexible connectors join five shutoffs to the two faucets and toilet tank. Both mixing bodies have connected mixed-water outlets. No sanitary or vent piping is represented.

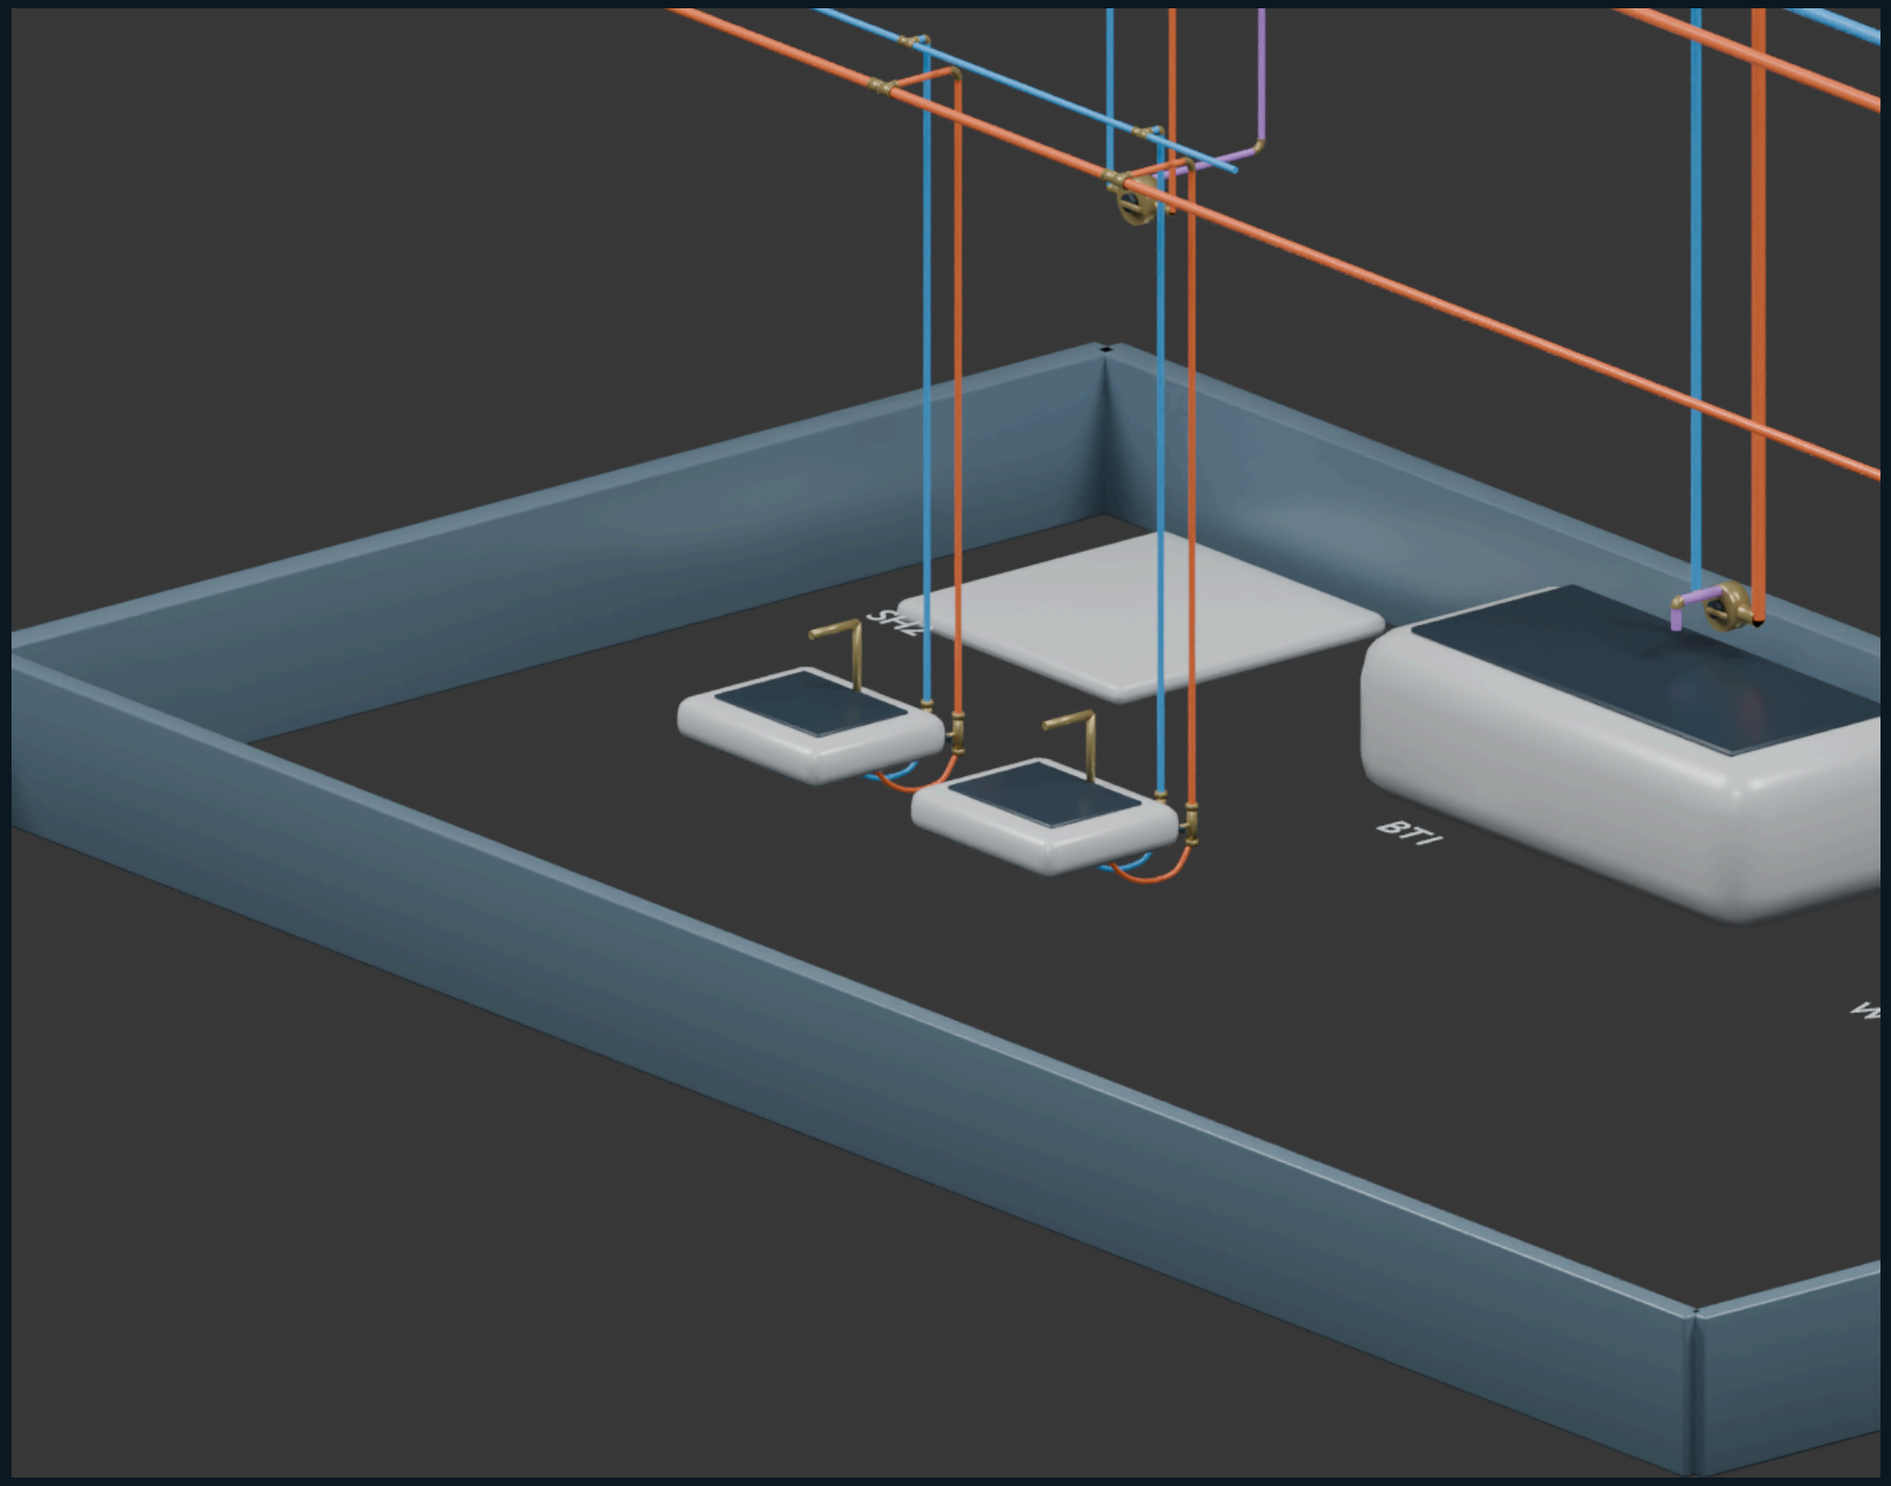

MODEL STUDY | Unit XY provisionally calibrated; pipe heights and envelopes assumed. Not an as-built.