


1/P2.02 ENLARGED MECHANICAL ROOM PLAN

SCALE: ¼" = 1'0"

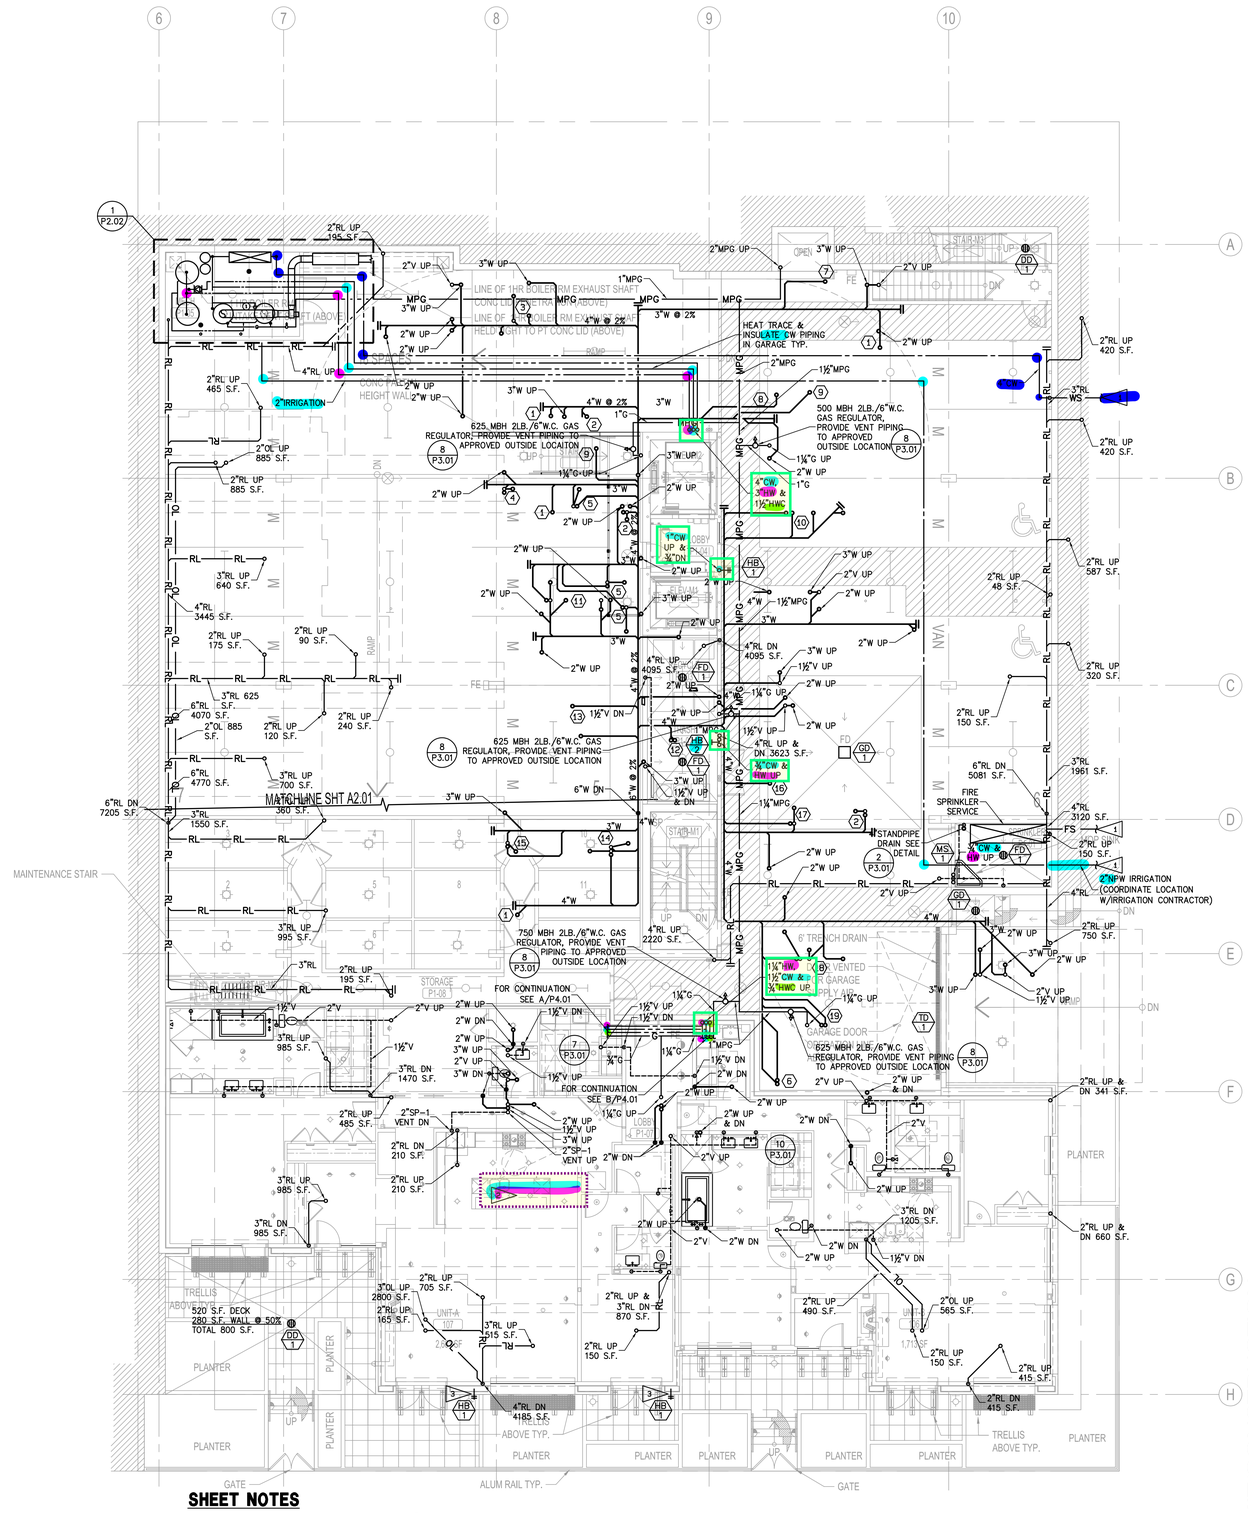

SHEET NOTES

1. 2"V DN TERMINATE 12" DN FROM CEILING WITH STUDOR VENT.

GENERAL NOTES

1. HEAT TRACE AND INSULATE ALL EXPOSED P-TRAPS IN GARAGE.
2. RL SLOPED @ ¼"/FT. UNLESS NOTED OTHERWISE.

1/P2.02 LEVEL P1 PLUMBING PLAN

SCALE: 1/8" = 1'0"

Continuous Riser or Riser Going Up

Cold Water

Hot Water

Hot Water Circulation

REUSE OF DOCUMENTS

THIS DOCUMENT, AND THE IDEAS AND DESIGNS INCORPORATED HEREIN, AS AN INSTRUMENT OF PROFESSIONAL SERVICE, IS THE PROPERTY OF HV ENGINEERING, INC. AND IS NOT TO BE USED, IN WHOLE OR IN PART, FOR ANY OTHER PROJECT WITHOUT THE WRITTEN AUTHORIZATION OF HV ENGINEERING.

COPYRIGHT, HV ENGINEERING, INC.

VERIFY SCALE

BAR MEASURES ONE INCH ON ORIGINAL DRAWING

0" 1"

IF NOT ONE INCH ON THIS DRAWING, ADJUST SCALES ACCORDINGLY.

HV Engineering, Inc.
Consulting Engineers
7100 Linden Ave. N.
Seattle, Washington, 98103
Phone: (206) 706-9669
Fax: (206) 706-1630
www. hvengineering. biz

Project

200 WEST HIGHLAND DRIVE

Location

202 W. HIGHLAND DRIVE
SEATTLE, WA 98119

Prepared For

SUNRISE Plumbing, Inc.
1415 22nd Street NW
Auburn, WA 98001
(253) 874-4083

THESE DRAWINGS WERE DEVELOPED FOR EXCLUSIVE USE BY SUNRISE PLUMBING, INC. ON A DESIGN BUILD CONCEPT. THEY ARE TO BE USED ONLY WITH WRITTEN PERMISSION OF SUNRISE PLUMBING, INC.. FOR INFORMATION CONTACT: DAVID WEST.

NO.	DATE	REVISION

PARTNER IN CHARGE: BWR
PROJECT MANAGER: BWR
PROJECT ENGINEER: BWR
PROJECT TEAM MEMBERS: BWR, SDB
CHECK: TGH

ENGINEERS SEAL

BRIAN W. ROETCISOENDER, STATE OF WASHINGTON, 30321, REGISTERED PROFESSIONAL ENGINEER

EXPIRES 12/01/07

TITLE: LEVEL P1 PLUMBING PLAN

PROJECT NO.: 2006-082


DATE: OCTOBER 29, 2007

PROJECT NETWORK PATH:

SHEET NUMBER: **P2.02**

ISSUED FOR PERMIT/CONSTRUCTION

I:\2006\2006-082 - Highlands Condo\DWG\Plumb\P2.02.dwg Oct 29, 2007 10:51am steve

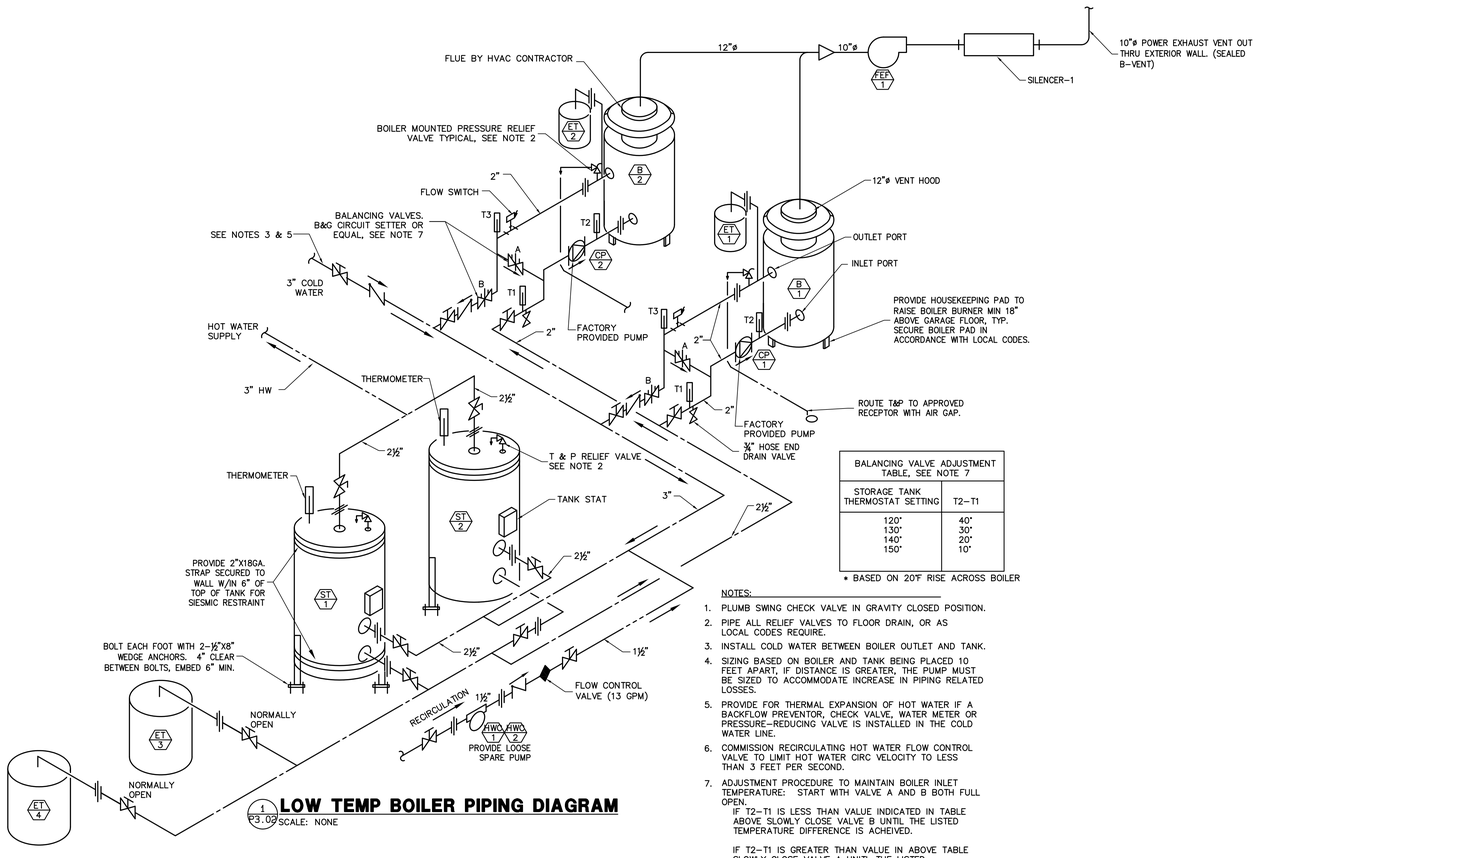

BALANCING VALVE ADJUSTMENT TABLE, SEE NOTE 7	
STORAGE TANK THERMOSTAT SETTING	T2–T1
120° 130° 140° 150°	40° 30° 20° 10°


* BASED ON 20°F RISE ACROSS BOILER

NOTES:

1. PLUMB SWING CHECK VALVE IN GRAVITY CLOSED POSITION.
2. PIPE ALL RELIEF VALVES TO FLOOR DRAIN, OR AS LOCAL CODES REQUIRE.
3. INSTALL COLD WATER BETWEEN BOILER OUTLET AND TANK.
4. SIZING BASED ON BOILER AND TANK BEING PLACED 10 FEET APART, IF DISTANCE IS GREATER, THE PUMP MUST BE SIZED TO ACCOMMODATE INCREASE IN PIPING RELATED LOSSES.
5. PROVIDE FOR THERMAL EXPANSION OF HOT WATER IF A BACKFLOW PREVENTOR, CHECK VALVE, WATER METER OR PRESSURE-REDUCING VALVE IS INSTALLED IN THE COLD WATER LINE.
6. COMMISSION RECIRCULATING HOT WATER FLOW CONTROL VALVE TO LIMIT HOT WATER CIRC VELOCITY TO LESS THAN 3 FEET PER SECOND.
7. ADJUSTMENT PROCEDURE TO MAINTAIN BOILER INLET TEMPERATURE: START WITH VALVE A AND B BOTH FULL OPEN.
   IF T2–T1 IS LESS THAN VALUE INDICATED IN TABLE ABOVE SLOWLY CLOSE VALVE B UNTIL THE LISTED TEMPERATURE DIFFERENCE IS ACHEIVED.
   IF T2–T1 IS GREATER THAN VALUE IN ABOVE TABLE SLOWLY CLOSE VALVE A UNITL THE LISTED TEMPERATURE DIFFERENCE IS ACHEIVED.
   CONFIRM T3–T2 = 20°F. AS STORED WATER REACHES THERMOSTAT SET POINT, THE TEMPERATURE INDICATED ON THERMOSTAT T3 APPROACHES 180°F.

1 P3.02 LOW TEMP BOILER PIPING DIAGRAM

SCALE: NONE

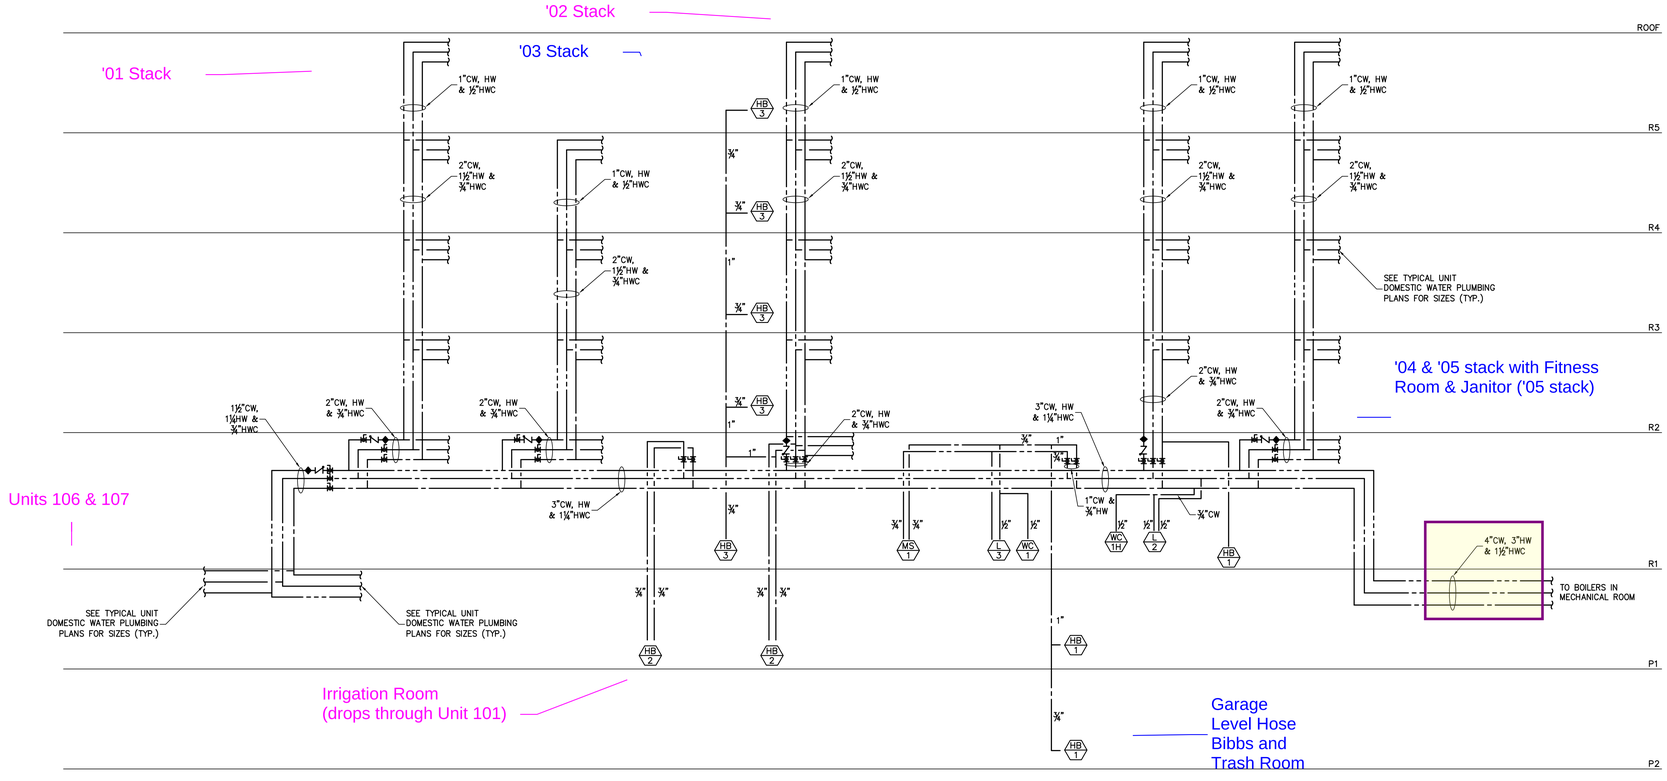

DOMESTIC WATER RISER DIAGRAMS

REUSE OF DOCUMENTS

THIS DOCUMENT, AND THE IDEAS AND DESIGNS INCORPORATED HEREIN, AS AN INSTRUMENT OF PROFESSIONAL SERVICE, IS THE PROPERTY OF HV ENGINEERING, INC. AND IS NOT TO BE USED, IN WHOLE OR IN PART, FOR ANY OTHER PROJECT WITHOUT THE WRITTEN AUTHORIZATION OF HV ENGINEERING.

COPYRIGHT, HV ENGINEERING, INC.

VERIFY SCALE

BAR MEASURES ONE INCH ON ORIGINAL DRAWING.
0" 1"
IF NOT ONE INCH ON THIS DRAWING, ADJUST SCALES ACCORDINGLY.

HV Engineering, Inc.
Consulting Engineers
7100 Linden Ave. N.
Seattle, Washington, 98103
Phone: (206) 706-9689
Fax: (206) 706-1630
www. hvengineering. biz

Project

200 WEST HIGHLAND DRIVE

Location

202 W. HIGHLAND DRIVE
SEATTLE, WA 98119

Prepared For

SUNRISE Plumbing, Inc.
1415 22nd Street NW
Auburn, WA 98001
(253) 874-4083

THESE DRAWINGS WERE DEVELOPED FOR EXCLUSIVE USE BY SUNRISE PLUMBING, INC. ON A DESIGN BUILD CONCEPT. THEY ARE TO BE USED ONLY WITH WRITTEN PERMISSION OF SUNRISE PLUMBING, INC. FOR INFORMATION CONTACT: DAVID WEST.

NO.	DATE	REVISION

PARTNER IN CHARGE: BWR
PROJECT MANAGER: BWR
PROJECT ENGINEER: BWR
PROJECT TEAM MEMBERS: BWR, SDB
CHECK: TGH

ENGINEERS SEAL

BRIAN W. ROETCISOENDER — STATE OF WASHINGTON — 20321 — REGISTERED PROFESSIONAL ENGINEER

EXPIRES 12/01/07


TITLE: DETAILS & RISER DIAGRAMS

PROJECT NO.: 2006-082
DATE: OCTOBER 29, 2007
PROJECT NETWORK PATH:


SHEET NUMBER: **P3.02**

ISSUED FOR PERMIT/CONSTRUCTION

I:\2006\2006-082 - Highlands Condo\DWGS\Plumb\P0.01.dwg Oct 29, 2007 10:53am steve

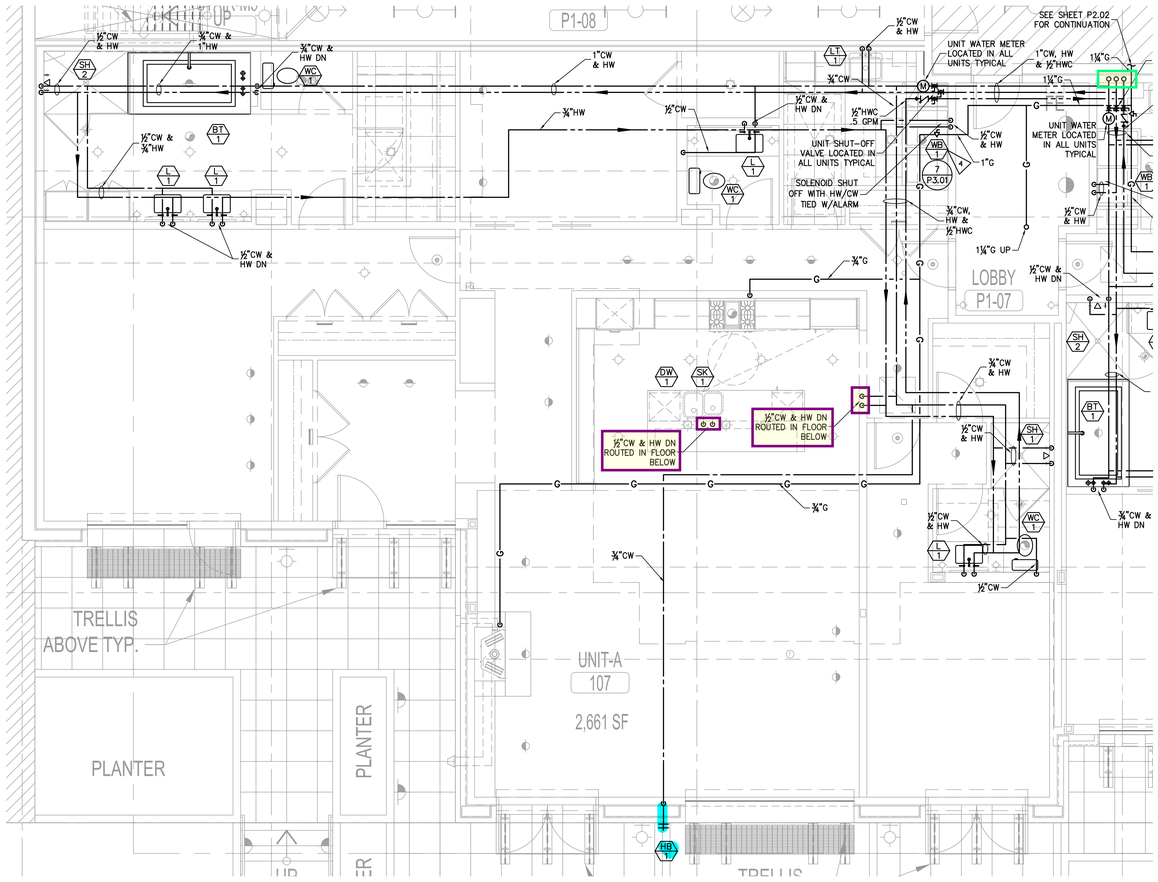

A **UNIT A DOMESTIC WATER PLAN**
SCALE: ¼" = 1'0"

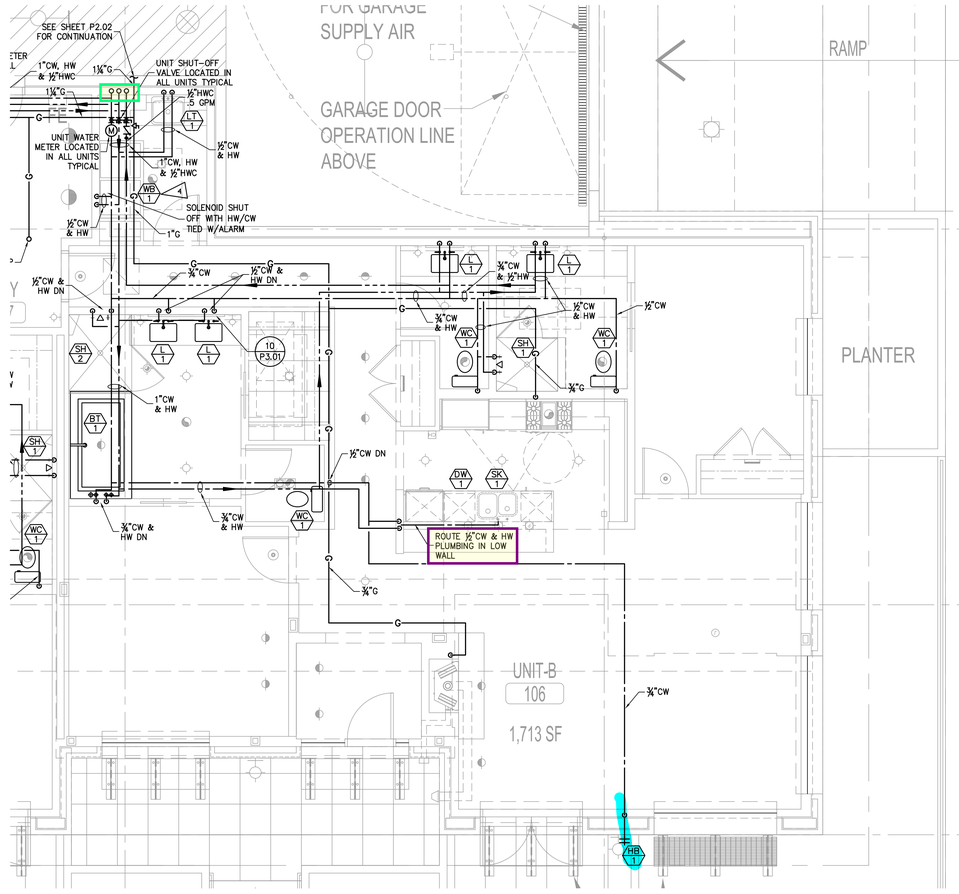

B **UNIT B DOMESTIC WATER PLAN**
SCALE: ¼" = 1'0"

REUSE OF DOCUMENTS

THIS DOCUMENT, AND THE IDEAS AND DESIGNS INCORPORATED HEREIN, AS AN INSTRUMENT OF PROFESSIONAL SERVICE, IS THE PROPERTY OF HV ENGINEERING, INC. AND IS NOT TO BE USED, IN WHOLE OR IN PART, FOR ANY OTHER PROJECT WITHOUT THE WRITTEN AUTHORIZATION OF HV ENGINEERING.

COPYRIGHT, HV ENGINEERING, INC.

VERIFY SCALE

BAR MEASURES ONE INCH ON ORIGINAL DRAWING
0" 1"
IF NOT ONE INCH ON THIS DRAWING, ADJUST SCALES ACCORDINGLY.

HV Engineering, Inc.
Consulting Engineers
7100 Linden Ave. N.
Seattle, Washington, 98103
Phone: (206) 706-9669
Fax: (206) 706-1630
www. hvengineering. biz

Project
200 WEST HIGHLAND DRIVE

Location
202 W. HIGHLAND DRIVE
SEATTLE, WA 98119

Prepared For
SUNRISE Plumbing, Inc.
1415 22nd Street NW
Auburn, WA 98001
(253) 874-4083

THESE DRAWINGS WERE DEVELOPED FOR EXCLUSIVE USE BY SUNRISE PLUMBING, INC. ON A DESIGN BUILD CONCEPT. THEY ARE TO BE USED ONLY WITH WRITTEN PERMISSION OF SUNRISE PLUMBING, INC.. FOR INFORMATION CONTACT: DAVID WEST.

NO.	DATE	REVISION

PARTNER IN CHARGE: BWR
PROJECT MANAGER: BWR
PROJECT ENGINEER: BWR
PROJECT TEAM MEMBERS: BWR, SDB
CHECK: TGH

ENGINEERS SEAL
BRIAN W. ROETCISOENDER — STATE OF WASHINGTON — 20321 — REGISTERED PROFESSIONAL ENGINEER
EXPIRES 12/01/07


TITLE
TYPICAL UNIT
DOMESTIC WATER
PLUMBING PLANS

PROJECT NO. 2006-082
DATE OCTOBER 29, 2007
PROJECT NETWORK PATH

SHEET NUMBER
P4.01

ISSUED FOR PERMIT/CONSTRUCTION

I:\2006\2006-082 - Highlands Condo\DWGS\Plumb\P4.01.dwg Oct. 29, 2007 10:54am steve

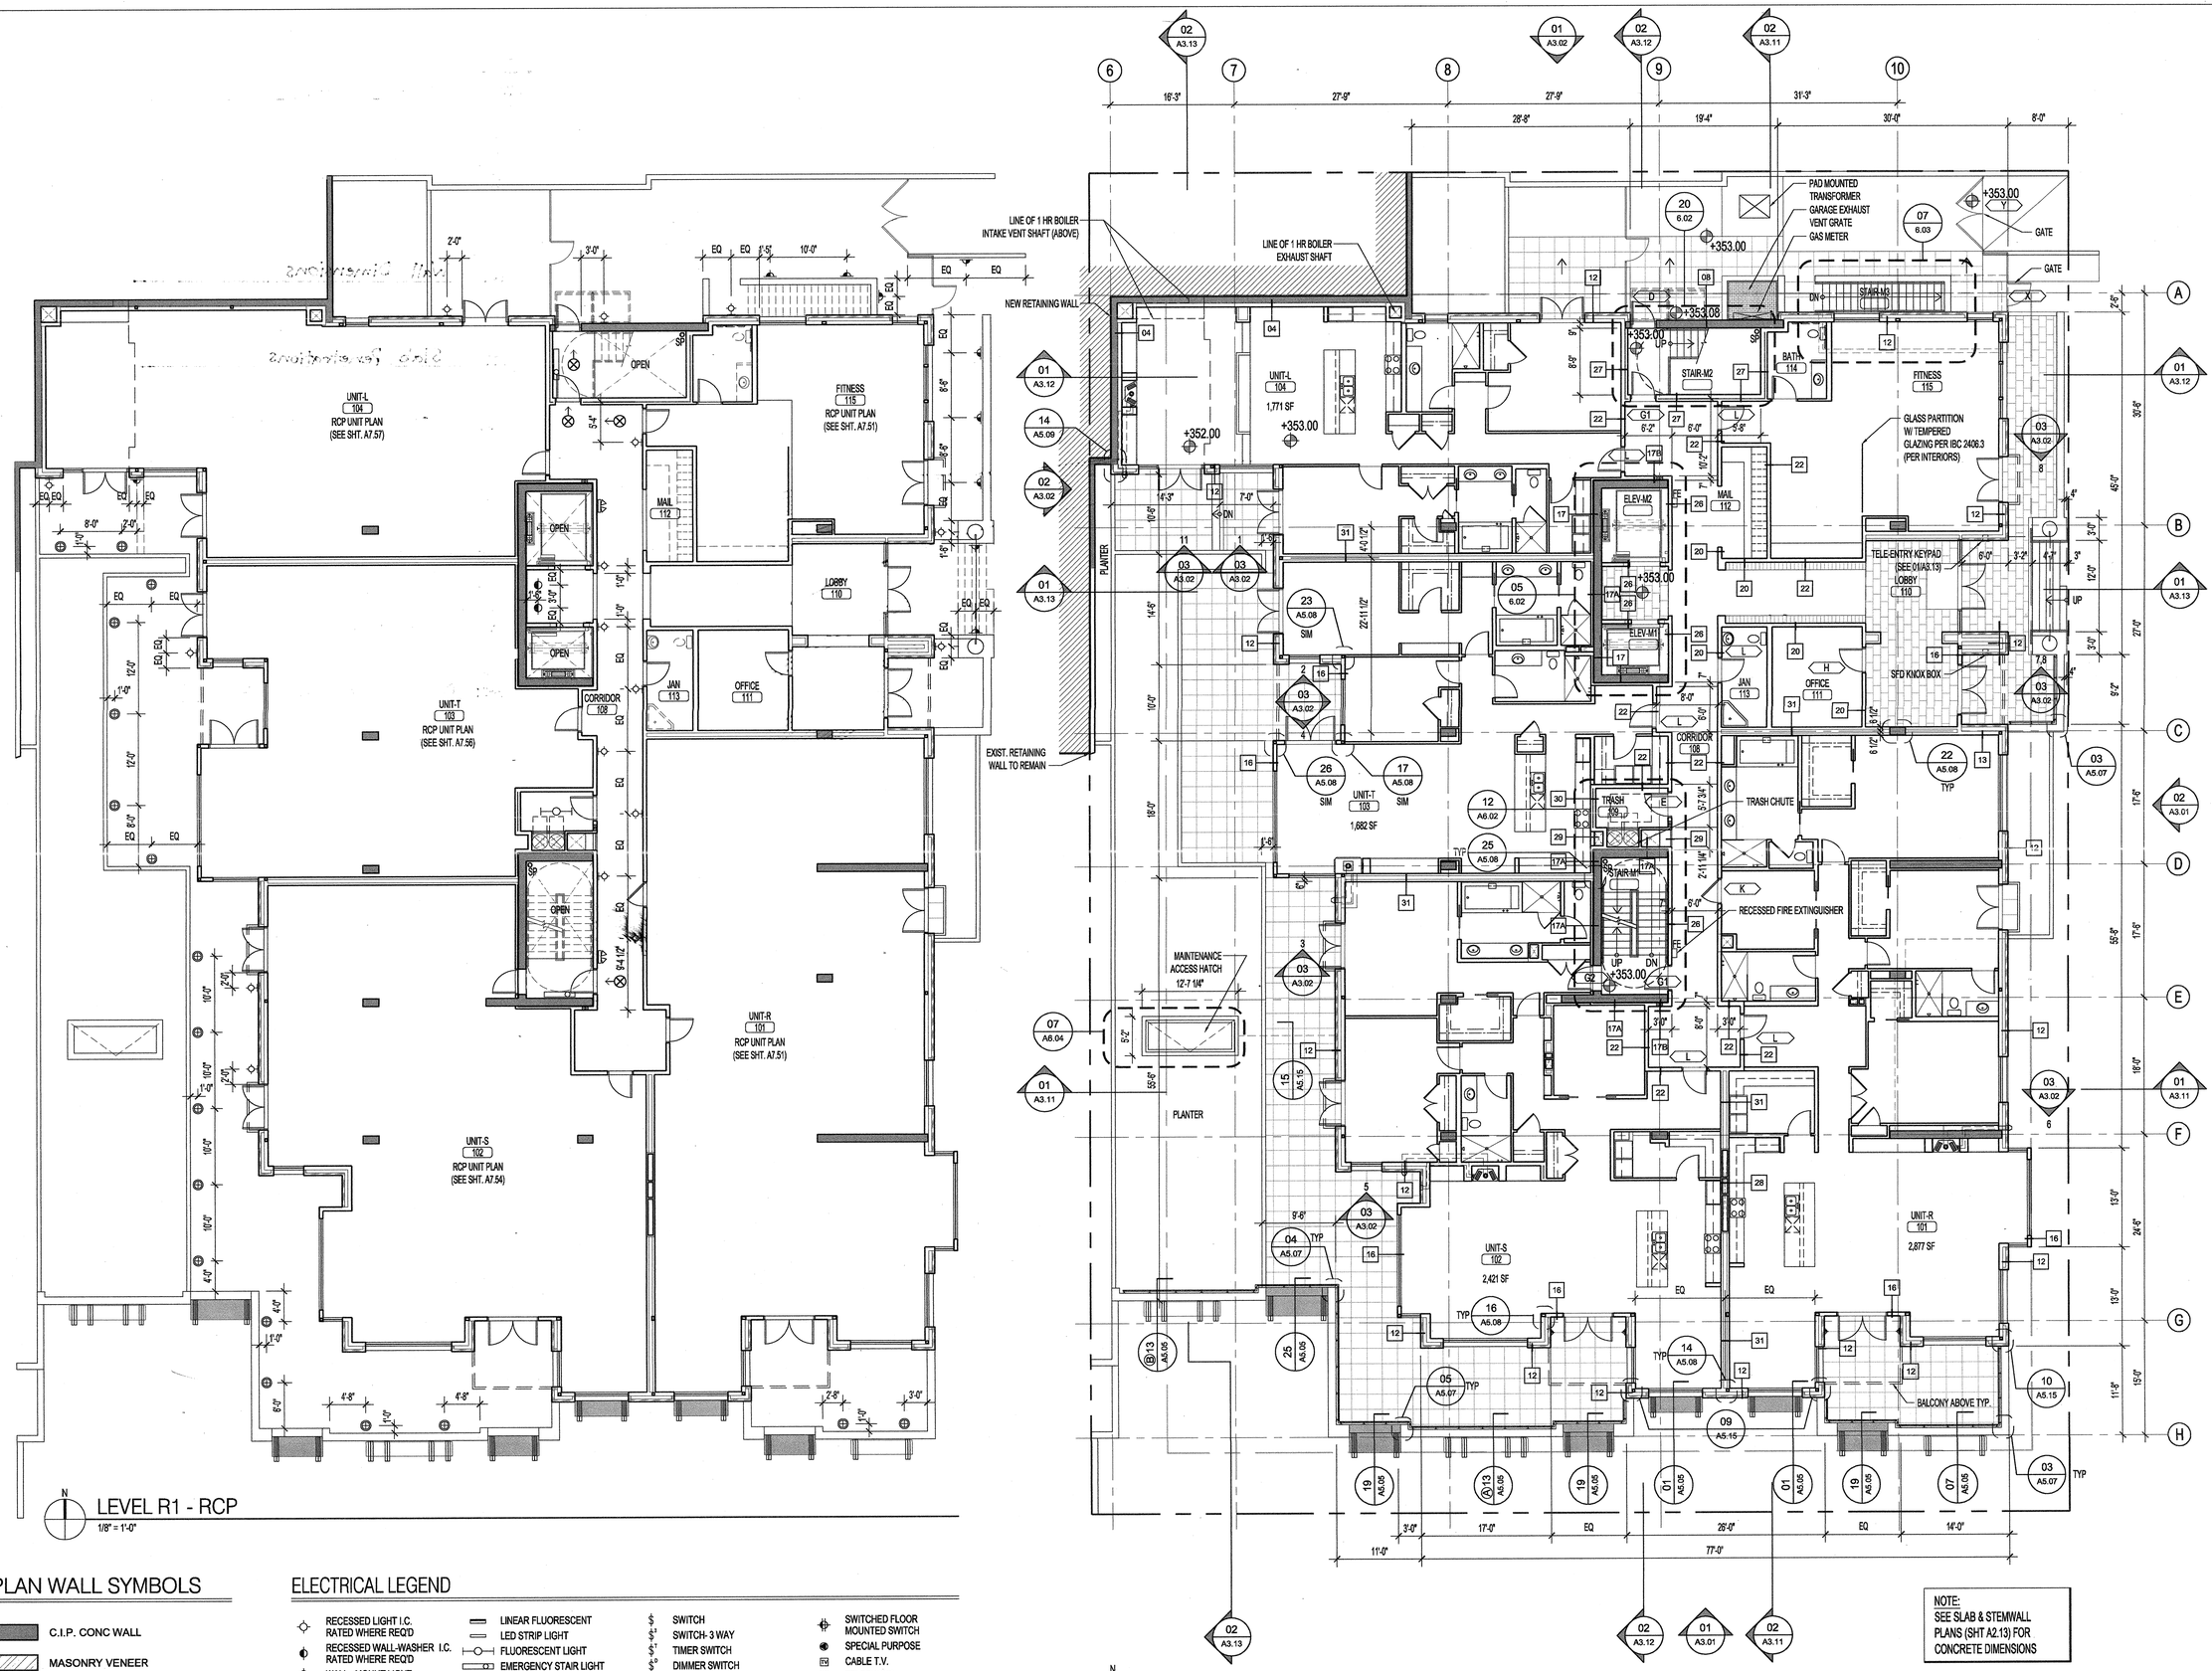

N

LEVEL R1 - RCP

1/8" = 1'-0"

N

LEVEL R1 - FLOOR PLAN (RESIDENTIAL)

1/8" = 1'-0"

NOTE:
SEE SLAB & STEMWALL PLANS (SHT A2.13) FOR CONCRETE DIMENSIONS

PLAN WALL SYMBOLS

- C.I.P. CONC WALL
- MASONRY VENEER
- PRECAST PANELS (ASSEMBLY 1)
- PRECAST PANELS (ASSEMBLY 2)
- MTL FRAMING

ELECTRICAL LEGEND

- RECESSED LIGHT I.C. RATED WHERE REQ'D
- RECESSED WALL-WASHER I.C. RATED WHERE REQ'D
- WALL - MOUNT LIGHT
- STEP LIGHT
- CEILING - MOUNT LIGHT
- PENDANT LIGHT
- LOW VOLTAGE TRACK LIGHTING
- FLOOR MOUNTED UP-LIGHT
- LOW VOLTAGE MONOPOINT
- LINEAR FLUORESCENT
- LED STRIP LIGHT
- FLUORESCENT LIGHT
- EMERGENCY STAIR LIGHT
- EMERGENCY CORRIDOR LIGHT
- FAN / LIGHT
- BULB HEATER
- JUNCTION BOX
- EXHAUST FAN - V.T.O.S.
- SMOKE DETECTOR W/ BATTERY BACKUP
- SWITCH
- SWITCH- 3 WAY
- TIMER SWITCH
- DIMMER SWITCH
- 110v OUTLET
- 220v HEAVY DUTY OUTLET
- GFI OUTLET
- WATERPROOF GFI OUTLET
- SWITCHED OUTLET
- FLOOR MOUNTED SWITCH
- SWITCHED FLOOR MOUNTED SWITCH
- SPECIAL PURPOSE
- CABLE T.V.
- TELEPHONE
- DATA
- DOORBELL CHIME
- DOORBELL
- THERMOSTAT

MITHUN
Architects+Designers+Planners
Pier 56
1201 Alaskan Way
Suite 200
Seattle, WA 98101
TEL 206 623.3344
FAX 206 623.7005

202 west highland

PROJECT:
200 W. Highland Drive

LOCATION:
202 W. Highland Drive
Seattle, WA 98119

PREPARED FOR:
Lorig Associates, LLC
2025 First Avenue, Suite 420
Seattle WA. 98121
T= 206.728.7660

RFI #

NO.	DATE	REVISION

PROJECT DIRECTOR: JB
PROJECT MANAGER: EMD
PROJECT ARCHITECT: BB
PROJECT TEAM MEMBERS: ML, ML
CHECK:

ARCHITECT SEAL


3689 REGISTERED ARCHITECT BRUCE L. WILLIAMS STATE OF WASHINGTON

TITLE
LEVEL R1 - PLAN & RCP

PROJECT NO.: 04470.00
DATE: 04-02-07
PROJECT NETWORK PATH: S:\ 2005\0447000\Cadd\
A\SHEETS
SHEET NUMBER
A2.03

CONTRACT DOCUMENTS


© 2004 MITHUN, INC.

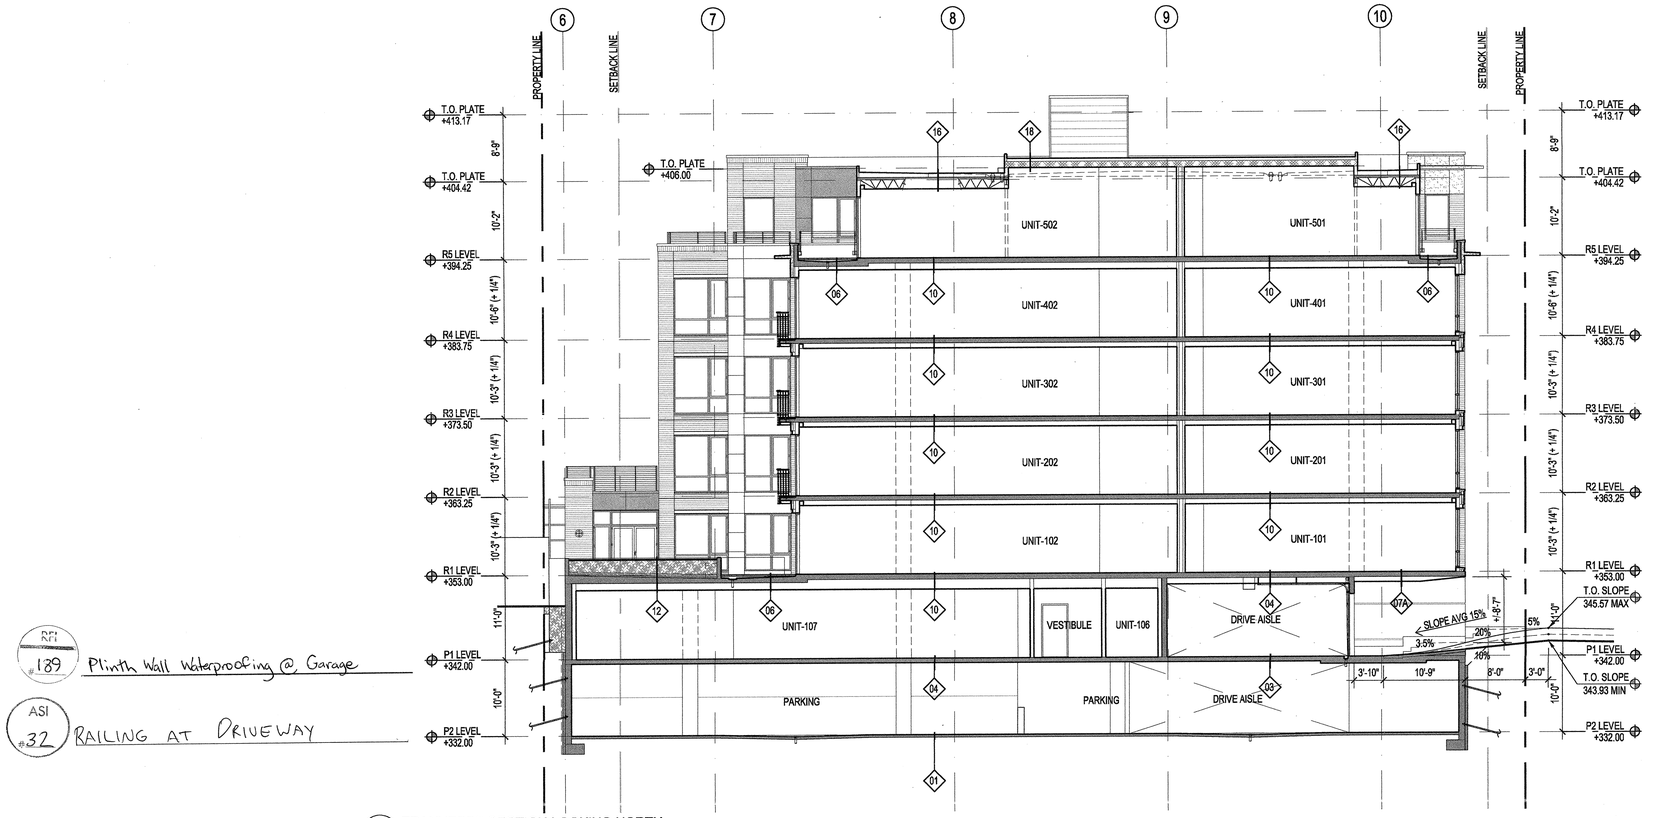

01 TRANVERSE SECTION LOOKING NORTH
1/8" = 1'-0"

ASI #189 Plinth Wall Waterproofing @ Garage

ASI #32 RAILING AT DRIVEWAY

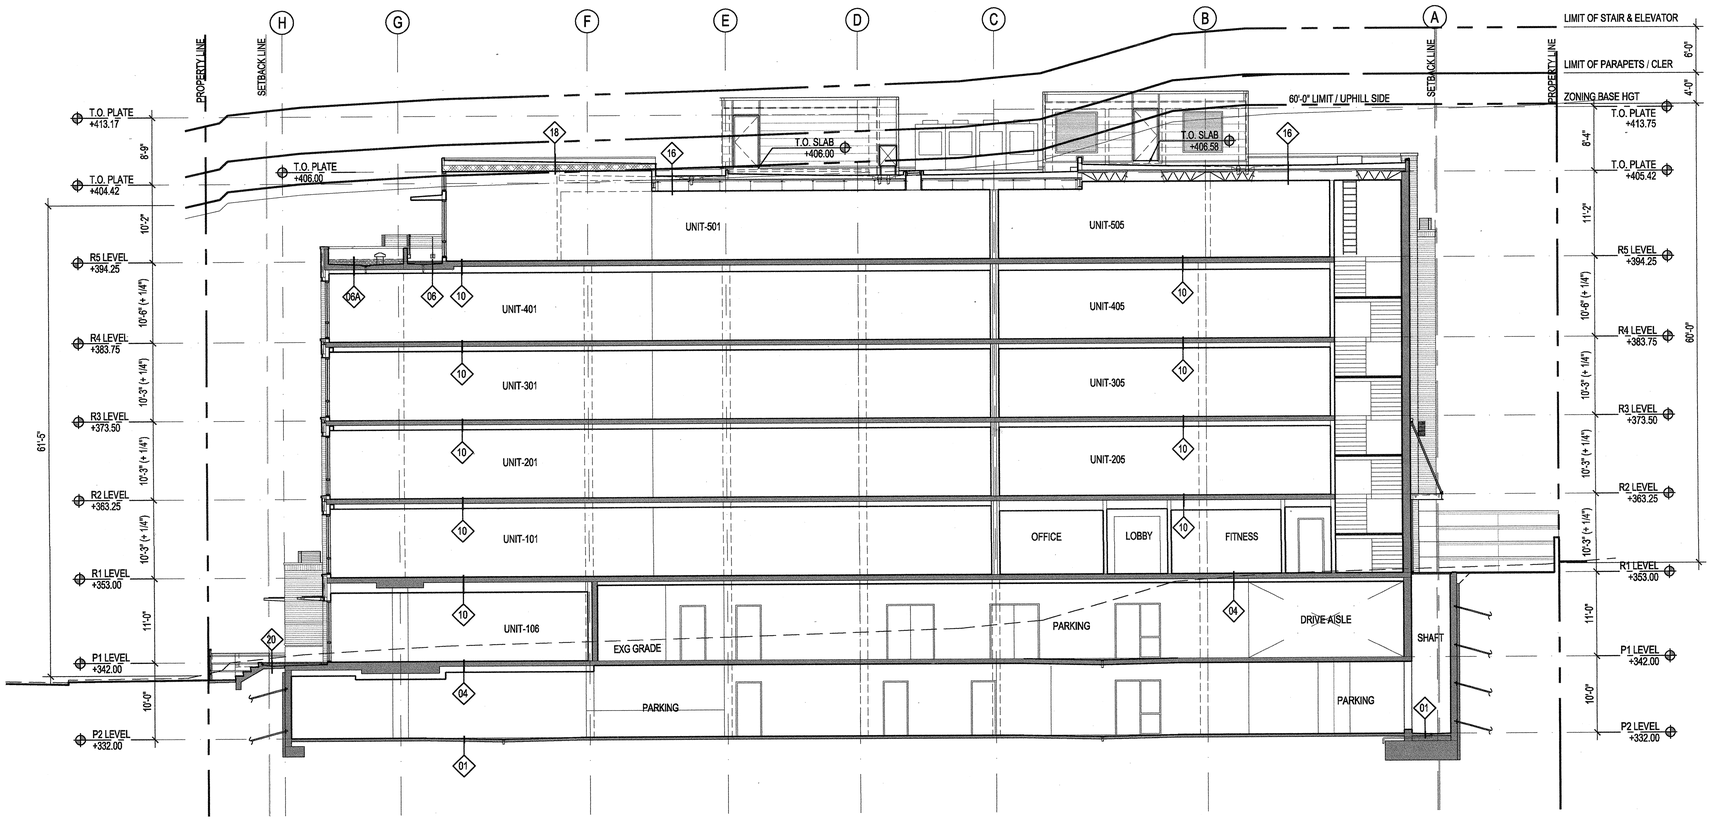

02 LONGITUDINAL SECTION LOOKING WEST
1/8" = 1'-0"

NOTE:
SEE SHT. A5.02 FOR FLOOR AND ROOF ASSEMBLIES

SECTION MATERIALS

- CAST IN PLACE (CIP) CONCRETE
- BRICK VENEER
- PRE-CAST CONCRETE PANEL (ASSEMBLY 1)
- PRE-CAST CONCRETE PANEL (ASSEMBLY 2)
- LIGHT-GAUGE METAL FRAMING

MITHUN
Architects+Designers+Planners

Pier 56
1201 Alaskan Way
Suite 200
Seattle, WA 98101
TEL 206 623.3344
FAX 206 623.7005

PROJECT:
200 W. Highland Drive

LOCATION:
202 W. Highland Drive
Seattle, WA 98119

PREPARED FOR:
Lorig Associates, LLC
2025 First Avenue, Suite 420
Seattle WA. 98121
T= 206.728.7660

NO.	DATE	REVISION

PROJECT DIRECTOR
JB
PROJECT MANAGER
EMD
PROJECT ARCHITECT
BB
PROJECT TEAM MEMBERS
ML, ML
CHECK

ARCHITECT SEAL:
3689 REGISTERED ARCHITECT
BRUCE L. WILLIAMS
STATE OF WASHINGTON

TITLE
BLDG SECTIONS

PROJECT NO.
04470.00
DATE
04-02-07
PROJECT NETWORK PATH
S:\ 2005\0447000\Cadd\
A\SHEETS
SHEET NUMBER
A3.11

CONTRACT DOCUMENTS

© 2004 MITHUN, INC.